

PT. CHANDRA ASRI ALKALI – CAA-1 PROJECT
PACKAGE CE & CA/EDC PLANT
Restricted

DOCUMENT TITLE:
PIPING ISOMETRIC DRAWING FOR 7 # PIPE RACK

DOCUMENT NO:
CAA-CE-1-ED-00-PIP-ISO-E-17001~17020

Document Review Result	
☐ Approved	
☐ Approved with Comments	
☐ Review with Comments	
☒ No Comment	
☐ Rejected	
CAA:	
By: <u>YULIAN</u>	Sign: <u>[Signature]</u> Date: <u>14 May 2026</u>

ISSUE FOR REVIEW

Contractor Name:
CHINA CHENGDA ENGINEERING CO., LTD

Contractor PO No.:
CD-2024-EP-607-00

Contractor Doc. No.:
00-42-0207-26-001~020

THE INFORMATION CONTAINED IN THIS DOCUMENT IS CONFIDENTIAL AND/OR RESTRICTED, PRIVILEGED, AND ONLY FOR THE SOLE USE OF THE INTENDED RECIPIENT AND INTENDED PURPOSE. ANY FORM OF REPRODUCTION, DISSEMINATION, COPYING, DISCLOSURE, MODIFICATION AND/OR PUBLICATION IS STRICTLY PROHIBITED WITHOUT PRIOR WRITTEN CONSENT FROM PT CHANDRA ASRI ALKALI AND/OR FROM THE RELEVANT OWNER OF SUCH INFORMATION.

OA	6/5/2026	Issue for Construction	XZS <u>[Signature]</u>	PJ <u>[Signature]</u>	ZWT <u>[Signature]</u>	WKY <u>[Signature]</u>
0	23/3/2026	Issue for Construction	XZS	PJ	ZWT	WKY
A	17/12/2025	Issue for Review	XZS	PJ	ZWT	WKY
Rev	Date Issued	Issue Purpose	Prepared	Checked	Approved	Authorized

China Chengda Engineering Co., Ltd	PT. CHANDRA ASRI ALKALI		
Issue for review	PIPING ISOMETRIC DRAWING FOR 7 # PIPE RACK		Restricted
Page 3 of 26	PROJECT DOC NO.: CAA-CE-1-ED-00-PIP-ISO-E-17001~17020	CONTRACTOR DOC NO.: 00-42-0207-26-001~020.	Rev 0A

GENERAL NOTES

- All dimensions, elevations and coordinates are in millimeters.
- EL. 0 corresponds to datum elevation +2.8 m (above mean sea level).
- All elevation data in ISO drawing indicate the center elevation of pipe.
- The coordinates (E, N) is adopted for design coordinate system.
- The (E=0, N=0) coordinates for general pipe rack is equivalent to (X=600000.000, Y=9330000.000)
- The conversion formula between (E,N) coordinate system and (X,Y) coordinate system (true coordinate system) is as follow:

$$N = (Y - 9330000) * 1000$$

$$E = (X - 600000) * 1000$$

E/N (mm)
X/Y (m)
- Dashed line in drawing means
 - the piping material is NOT indicated in MTO list due to hold items.
 - the connected item is not provided by piping MTO
 - connected drawing reference.
 - Piping insulation
- Shop weld means the welding work will be done in Chinese fabrication factory. Field weld means the welding work will be done at site.
- "Prefabricator" in drawing list means part of the pipeline will be prefabricated in Chinese fabrication factory.
- The data in isometric note table sources from line list document. If there is a discrepancy in data between ISO and line list, the relevant work at site shall refer to line list.
- Regarding the safety relief piping, a 10mm minimum weep hole shall be provided at the low point of the discharge piping when discharging to ATM.
- Regarding the pipe required personal protection, if there is not enough space to install wired mesh contractor can use thermal insulation material for personal protection material and must be approved by company.
- The abbreviation meaning of specialty.


PIPING SPECIAL ITEM	CODE
PRESSURE SAFETY VALVE	PSV
RUPTURE DISC	RD
PRESSURE REDUCING REGULATOR	PCV
PRESSURE RELIEF VALVE	PRV
VACUUM RELIEF VALVE	VRV
PRESSURE & VACUUM RELIEF VALVE	PVRV
EMERGENCY VENT MANHOLE	EV
FLEXIBLE HOSE	HS
EXPANSION JOINT	EX

DISCLAIMER: THE INFORMATION CONTAINED IN THIS DOCUMENT IS CONFIDENTIAL AND/OR RESTRICTED, PRIVILEGED, AND ONLY FOR THE SOLE USE OF THE INTENDED RECIPIENT AND INTENDED PURPOSE. ANY FORM OF REPRODUCTION, DISSEMINATION, COPYING, DISCLOSURE, MODIFICATION AND/OR PUBLICATION IS STRICTLY PROHIBITED WITHOUT PRIOR WRITTEN CONSENT FROM PT CHANDRA ASRI ALKALI AND/OR FROM THE RELEVANT OWNER OF SUCH INFORMATION.

China Chengda Engineering Co., Ltd	PT. CHANDRA ASRI ALKALI		
Issue for review	PIPING ISOMETRIC DRAWING FOR 7 # PIPE RACK		Restricted
Page 4 of 26	PROJECT DOC NO.: CAA-CE-1-ED-00-PIP-ISO-E-17001~17020	CONTRACTOR DOC NO.: 00-42-0207-26-001~020.	Rev 0A

SIGHT GLASS	SG
SILENCER	SIL
RESTRICTION ORIFICE	RO
STEAM TRAP	ST
STRAINER	STR
SUCTION BELL MOUTH AND BRACKET	SF
FLAME ARRESTOR	FA
SAFETY SHOWER & EYE WASHER	EW
QUICK-OPEN BLIND	ROV
MISCELLANEOUS SPECIAL PART	SP
STATIC LINE MIXER	MX
AIR FILTER	AF
MIST SEPARATOR	MS
INSERT PIPE	IP
DESUPERHEATER	BH
EJECTOR	EE
AUTOMATIC EXHAUST VALVE	AEV
NET SCREEN	S
STOPLOG VALVE	GA
AUTOMATIC RECIRCULATION VALVE	ARV
COUPLING	CP


14. Regarding the hose connection of Utility Station, refer to below typical drawing. After the connection is purchased, it will be indicated.

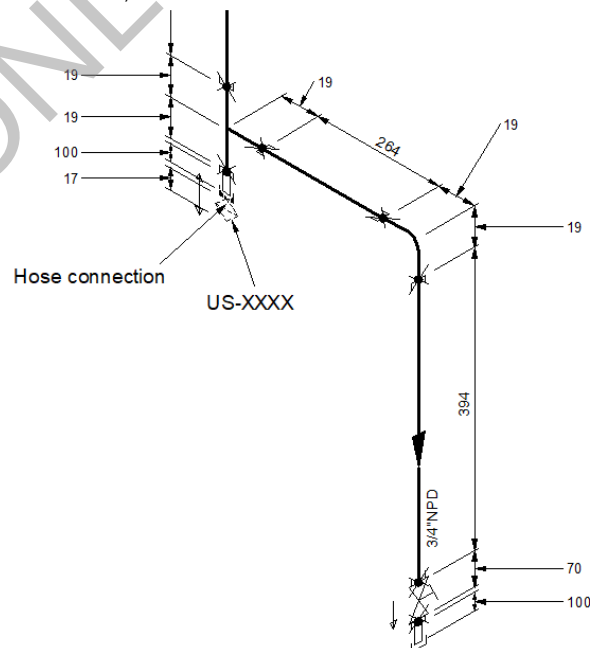

DISCLAIMER: THE INFORMATION CONTAINED IN THIS DOCUMENT IS CONFIDENTIAL AND/OR RESTRICTED, PRIVILEGED, AND ONLY FOR THE SOLE USE OF THE INTENDED RECIPIENT AND INTENDED PURPOSE. ANY FORM OF REPRODUCTION, DISSEMINATION, COPYING, DISCLOSURE, MODIFICATION AND/OR PUBLICATION IS STRICTLY PROHIBITED WITHOUT PRIOR WRITTEN CONSENT FROM PT CHANDRA ASRI ALKALI AND/OR FROM THE RELEVANT OWNER OF SUCH INFORMATION.

China Chengda Engineering Co., Ltd	PT. CHANDRA ASRI ALKALI		
Issue for review	PIPING ISOMETRIC DRAWING FOR 7 # PIPE RACK		Restricted
Page 5 of 26	PROJECT DOC NO.: CAA-CE-1-ED-00-PIP-ISO-E-17001~17020	CONTRACTOR DOC NO.: 00-42-0207-26-001~020.	Rev 0A

15. Regarding all the Nozzle related pipeline, if the pipeline has welds, RT/PT is applicated. If the pipeline is entirely flange connected without any weld, RT/PT is not applicabile.
16. Regarding all the nozzle related pipeline, if the pipeline has welds, the pressure test will be conducted. It the pipeline is entirely flange connected without any weld, the pressure test will not be conducted.
17. Regarding the welds between small size pipe and blind with hole, please refer to the below fig. for the detail.

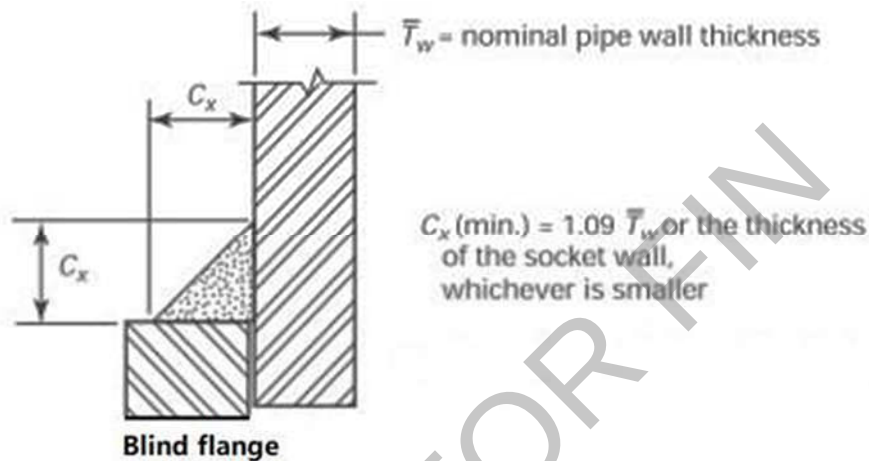

NOTE


HOLD


DISCLAIMER: THE INFORMATION CONTAINED IN THIS DOCUMENT IS CONFIDENTIAL AND/OR RESTRICTED, PRIVILEGED, AND ONLY FOR THE SOLE USE OF THE INTENDED RECIPIENT AND INTENDED PURPOSE. ANY FORM OF REPRODUCTION, DISSEMINATION, COPYING, DISCLOSURE, MODIFICATION AND/OR PUBLICATION IS STRICTLY PROHIBITED WITHOUT PRIOR WRITTEN CONSENT FROM PT CHANDRA ASRI ALKALI AND/OR FROM THE RELEVANT OWNER OF SUCH INFORMATION.

China Chengda Engineering Co., Ltd	PT. CHANDRA ASRI ALKALI		
Issue for review	PIPING ISOMETRIC DRAWING FOR 7 # PIPE RACK		Restricted
Page 6 of 26	PROJECT DOC NO.: CAA-CE-1-ED-00-PIP-ISO-E-17001~17020	CONTRACTOR DOC NO.: 00-42-0207-26-001~020.	Rev 0A

NO.	Contractor/Licenser Doc No.	Isometric drawing No:	Dwg. Size	Sheets	Rev.	Remark	Prefabrication
1	0.75"-NG-3518U-C01-01	00-42-0207-26-NG-3518U-01	A3	1	0A		
2	0.75"-NG-3518U-C01-02	00-42-0207-26-NG-3518U-02	A3	1	0A		
3	0.75"-NG-3518U-C01-03	00-42-0207-26-NG-3518U-03	A3	1	0A		
4	0.75"-NG-3518U-C01-04	00-42-0207-26-NG-3518U-04	A3	1	0A		
5	0.75"-NG-3518U-C01-05	00-42-0207-26-NG-3518U-05	A3	1	0A		
6	1"-NG-3518U-C01-06	00-42-0207-26-NG-3518U-06	A3	1	0A		
7	0.75"-PA-3519U-1C2-01	00-42-0207-26-PA-3519U-01	A3	1	0A		
8	0.75"-PA-3519U-1C2-02	00-42-0207-26-PA-3519U-02	A3	1	0A		
9	0.75"-PA-3519U-1C2-03	00-42-0207-26-PA-3519U-03	A3	1	0A		
10	0.75"-PA-3519U-1C2-04	00-42-0207-26-PA-3519U-04	A3	1	0A		
11	0.75"-PA-3519U-1C2-05	00-42-0207-26-PA-3519U-05	A3	1	0A		
12	1"-PA-3519U-1C2-06	00-42-0207-26-PA-3519U-06	A3	1	0A		
13	2"-PW-0003-1C6-HC-01	00-42-0207-26-PW-0003-01	A3	1	0A		
14	2"-PW-0003-1C6-HC-02	00-42-0207-26-PW-0003-02	A3	1	0A		
15	0.75"-WV-3520U-C01-01	00-42-0207-26-WV-3520U-01	A3	1	0A		
16	0.75"-WV-3520U-C01-02	00-42-0207-26-WV-3520U-02	A3	1	0A		
17	0.75"-WV-3520U-C01-03	00-42-0207-26-WV-3520U-03	A3	1	0A		
18	0.75"-WV-3520U-C01-04	00-42-0207-26-WV-3520U-04	A3	1	0A		
19	0.75"-WV-3520U-C01-05	00-42-0207-26-WV-3520U-05	A3	1	0A		
20	1"-WV-3520U-C01-06	00-42-0207-26-WV-3520U-06	A3	1	0A		

DISCLAIMER: THE INFORMATION CONTAINED IN THIS DOCUMENT IS CONFIDENTIAL AND/OR RESTRICTED, PRIVILEGED, AND ONLY FOR THE SOLE USE OF THE INTENDED RECIPIENT AND INTENDED PURPOSE. ANY FORM OF REPRODUCTION, DISSEMINATION, COPYING, DISCLOSURE, MODIFICATION AND/OR PUBLICATION IS STRICTLY PROHIBITED WITHOUT PRIOR WRITTEN CONSENT FROM PT CHANDRA ASRI ALKALI AND/OR FROM THE RELEVANT OWNER OF SUCH INFORMATION.

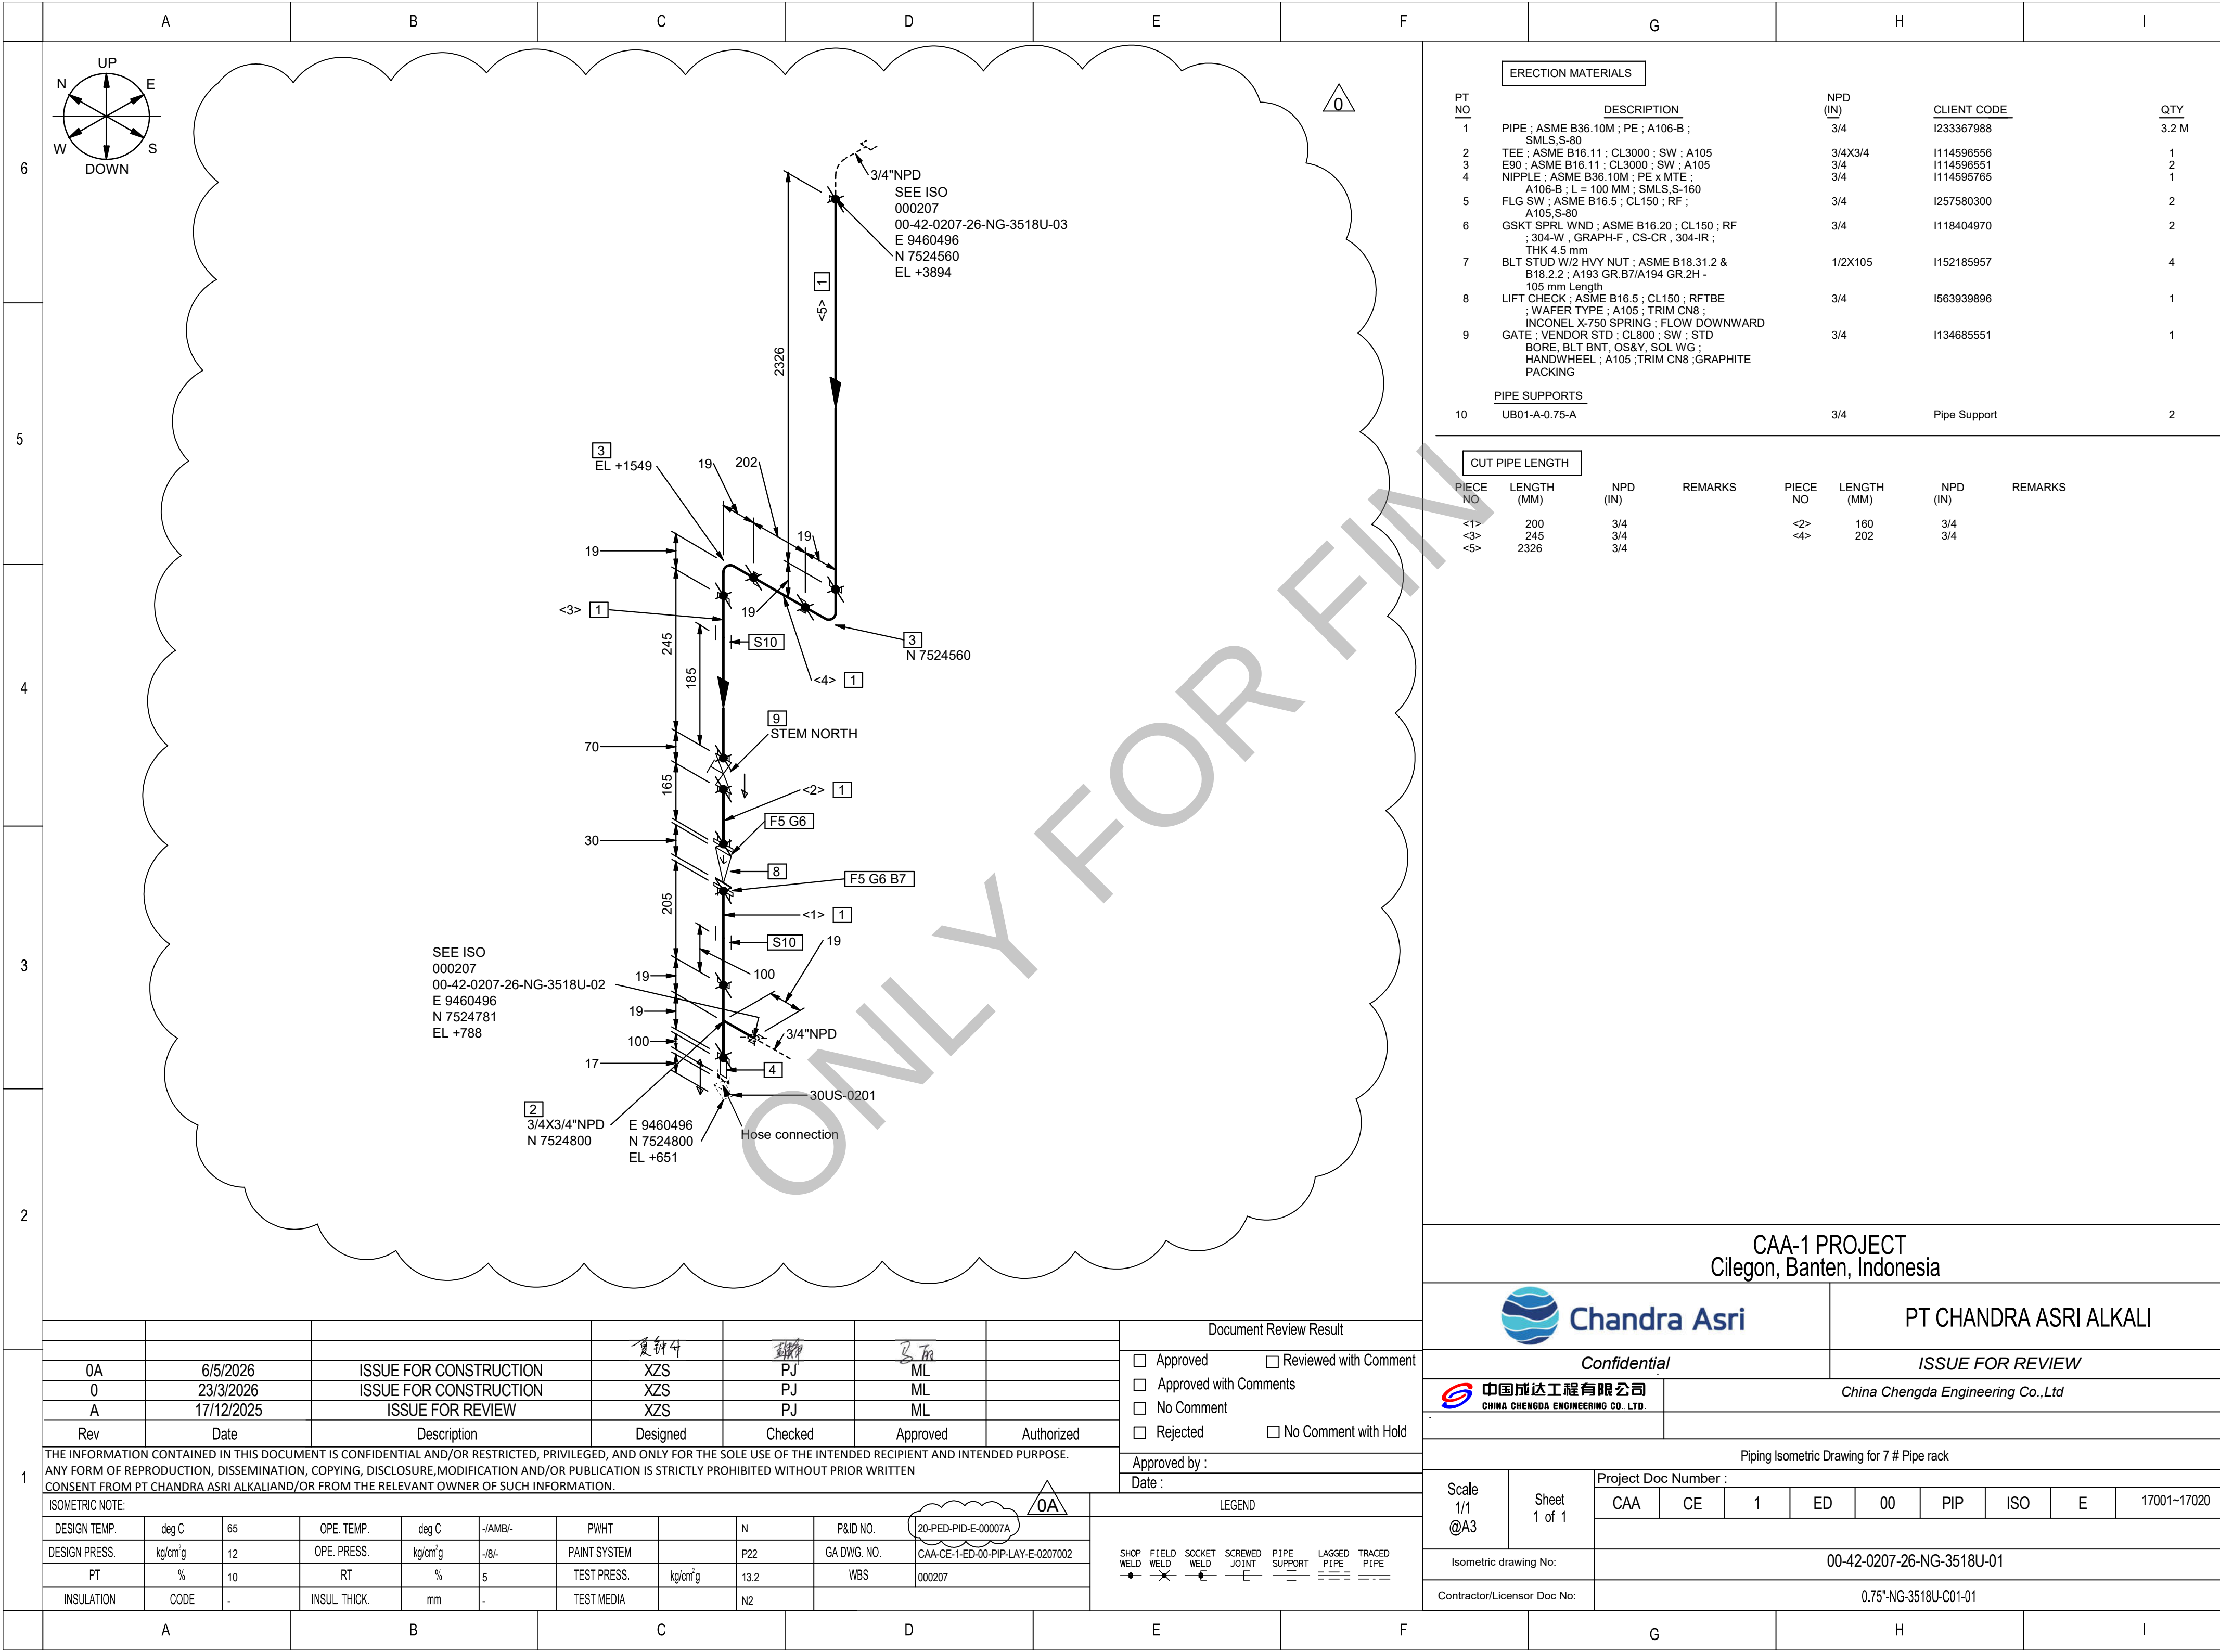

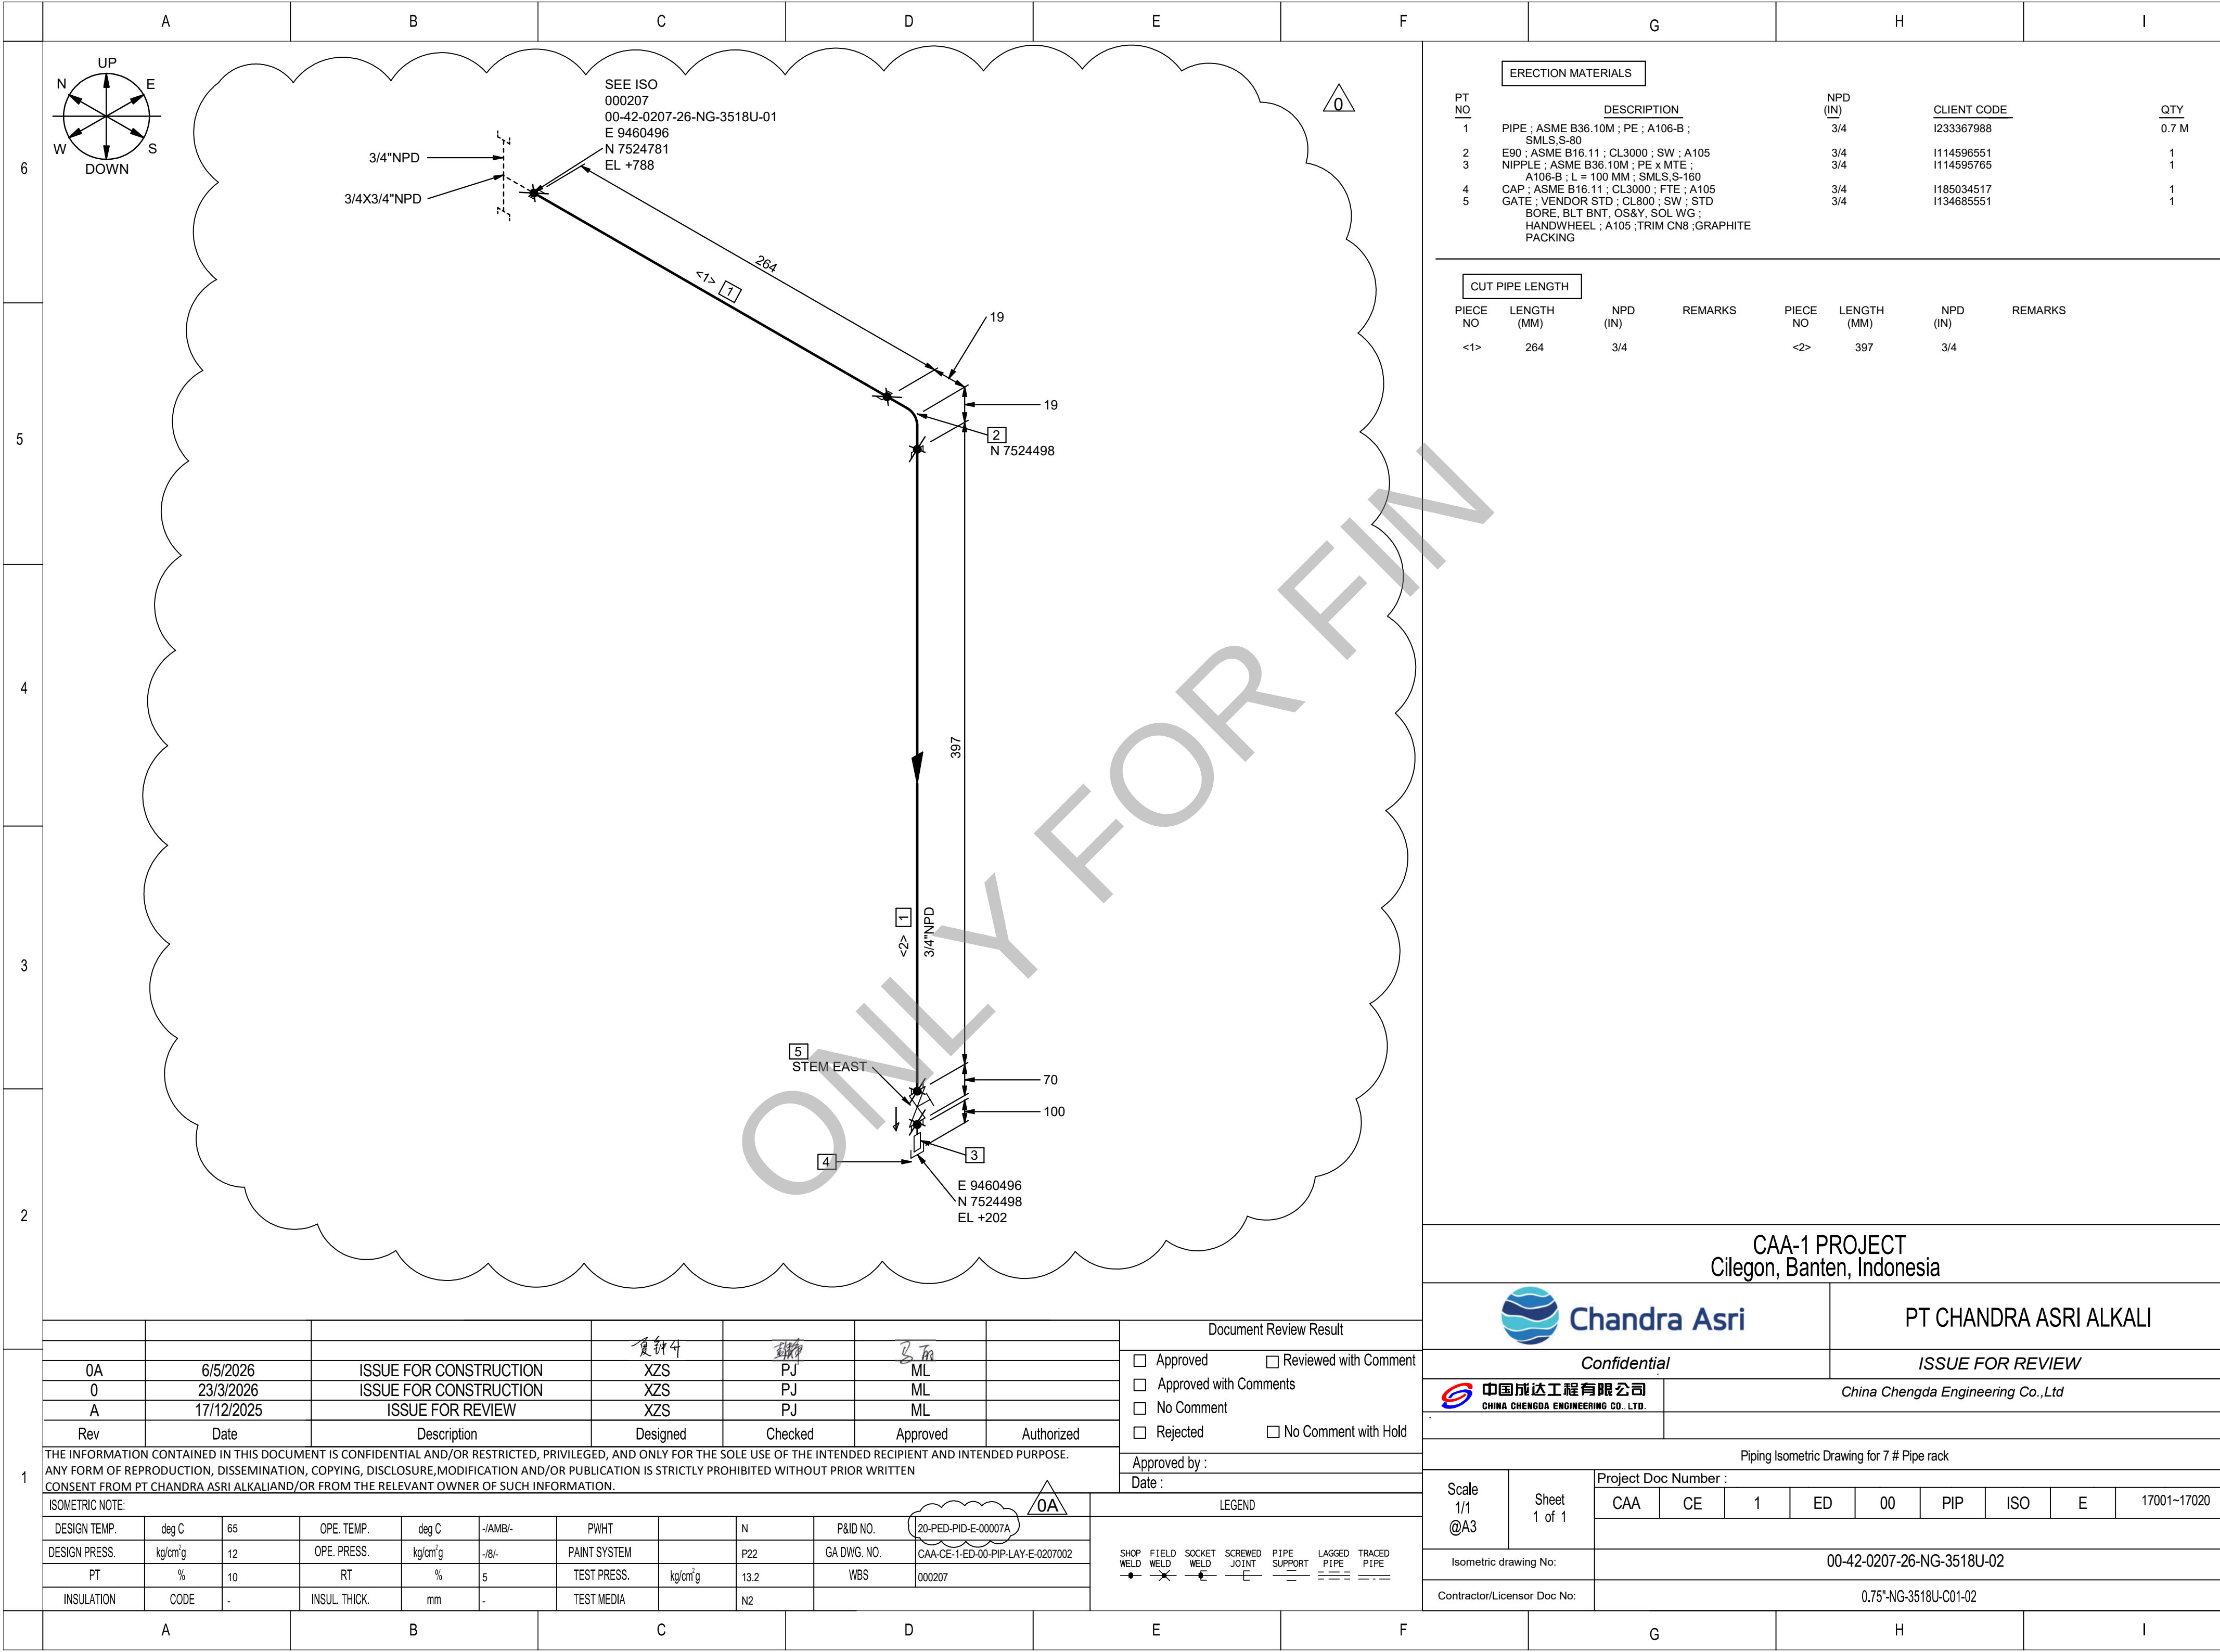

ERECTION MATERIALS				
PT NO	DESCRIPTION	NPD (IN)	CLIENT CODE	QTY
1	PIPE ; ASME B36.10M ; PE ; A106-B ; SMLS,S-80	3/4	I233367988	0.7 M
2	E90 ; ASME B16.11 ; CL3000 ; SW ; A105	3/4	I114596551	1
3	NIPPLE ; ASME B36.10M ; PE x MTE ; A106-B ; L = 100 MM ; SMLS,S-160	3/4	I114595765	1
4	CAP ; ASME B16.11 ; CL3000 ; FTE ; A105	3/4	I185034517	1
5	GATE ; VENDOR STD ; CL800 ; SW ; STD BORE, BLT BNT, OS&Y, SOL WG ; HANDWHEEL ; A105 ;TRIM CN8 ;GRAPHITE PACKING	3/4	I134685551	1

CUT PIPE LENGTH							
PIECE NO	LENGTH (MM)	NPD (IN)	REMARKS	PIECE NO	LENGTH (MM)	NPD (IN)	REMARKS
<1>	264	3/4		<2>	397	3/4	

Document Review Result						
☐ Approved ☐ Reviewed with Comment						
☐ Approved with Comments						
☐ No Comment						
☐ Rejected ☐ No Comment with Hold						
Approved by :						
Date :						
LEGEND						
SHOP WELD	FIELD WELD	SOCKET WELD	SCREWED JOINT	PIPE SUPPORT	LAGGED PIPE	TRACED PIPE
—●—	—X—	—E—	—E—	—	—	—

DESIGN TEMP.	deg C	65	OPE. TEMP.	deg C	-/AMB/-	PWHT		N	P&ID NO.	20-PED-PIE-E-00007A
DESIGN PRESS.	kg/cm ² g	12	OPE. PRESS.	kg/cm ² g	-/8/-	PAINT SYSTEM		P22	GA DWG. NO.	CAA-CE-1-ED-00-PIP-LAY-E-0207002
PT	%	10	RT	%	5	TEST PRESS.	kg/cm ² g	13.2	WBS	000207
INSULATION	CODE	-	INSUL THICK.	mm	-	TEST MEDIA		N2		

CAA-1 PROJECT
Cilegon, Banten, Indonesia

Chandra Asri

PT CHANDRA ASRI ALKALI

Confidential

ISSUE FOR REVIEW

中国成达工程有限公司
CHINA CHENGDA ENGINEERING CO., LTD.

China Chengda Engineering Co.,Ltd

Piping Isometric Drawing for 7 # Pipe rack


Scale 1/1 @A3

Sheet 1 of 1

Project Doc Number : CAA CE 1 ED 00 PIP ISO E 17001-17020

Isometric drawing No: 00-42-0207-26-NG-3518U-02

Contractor/Licensor Doc No: 0.75"-NG-3518U-C01-02

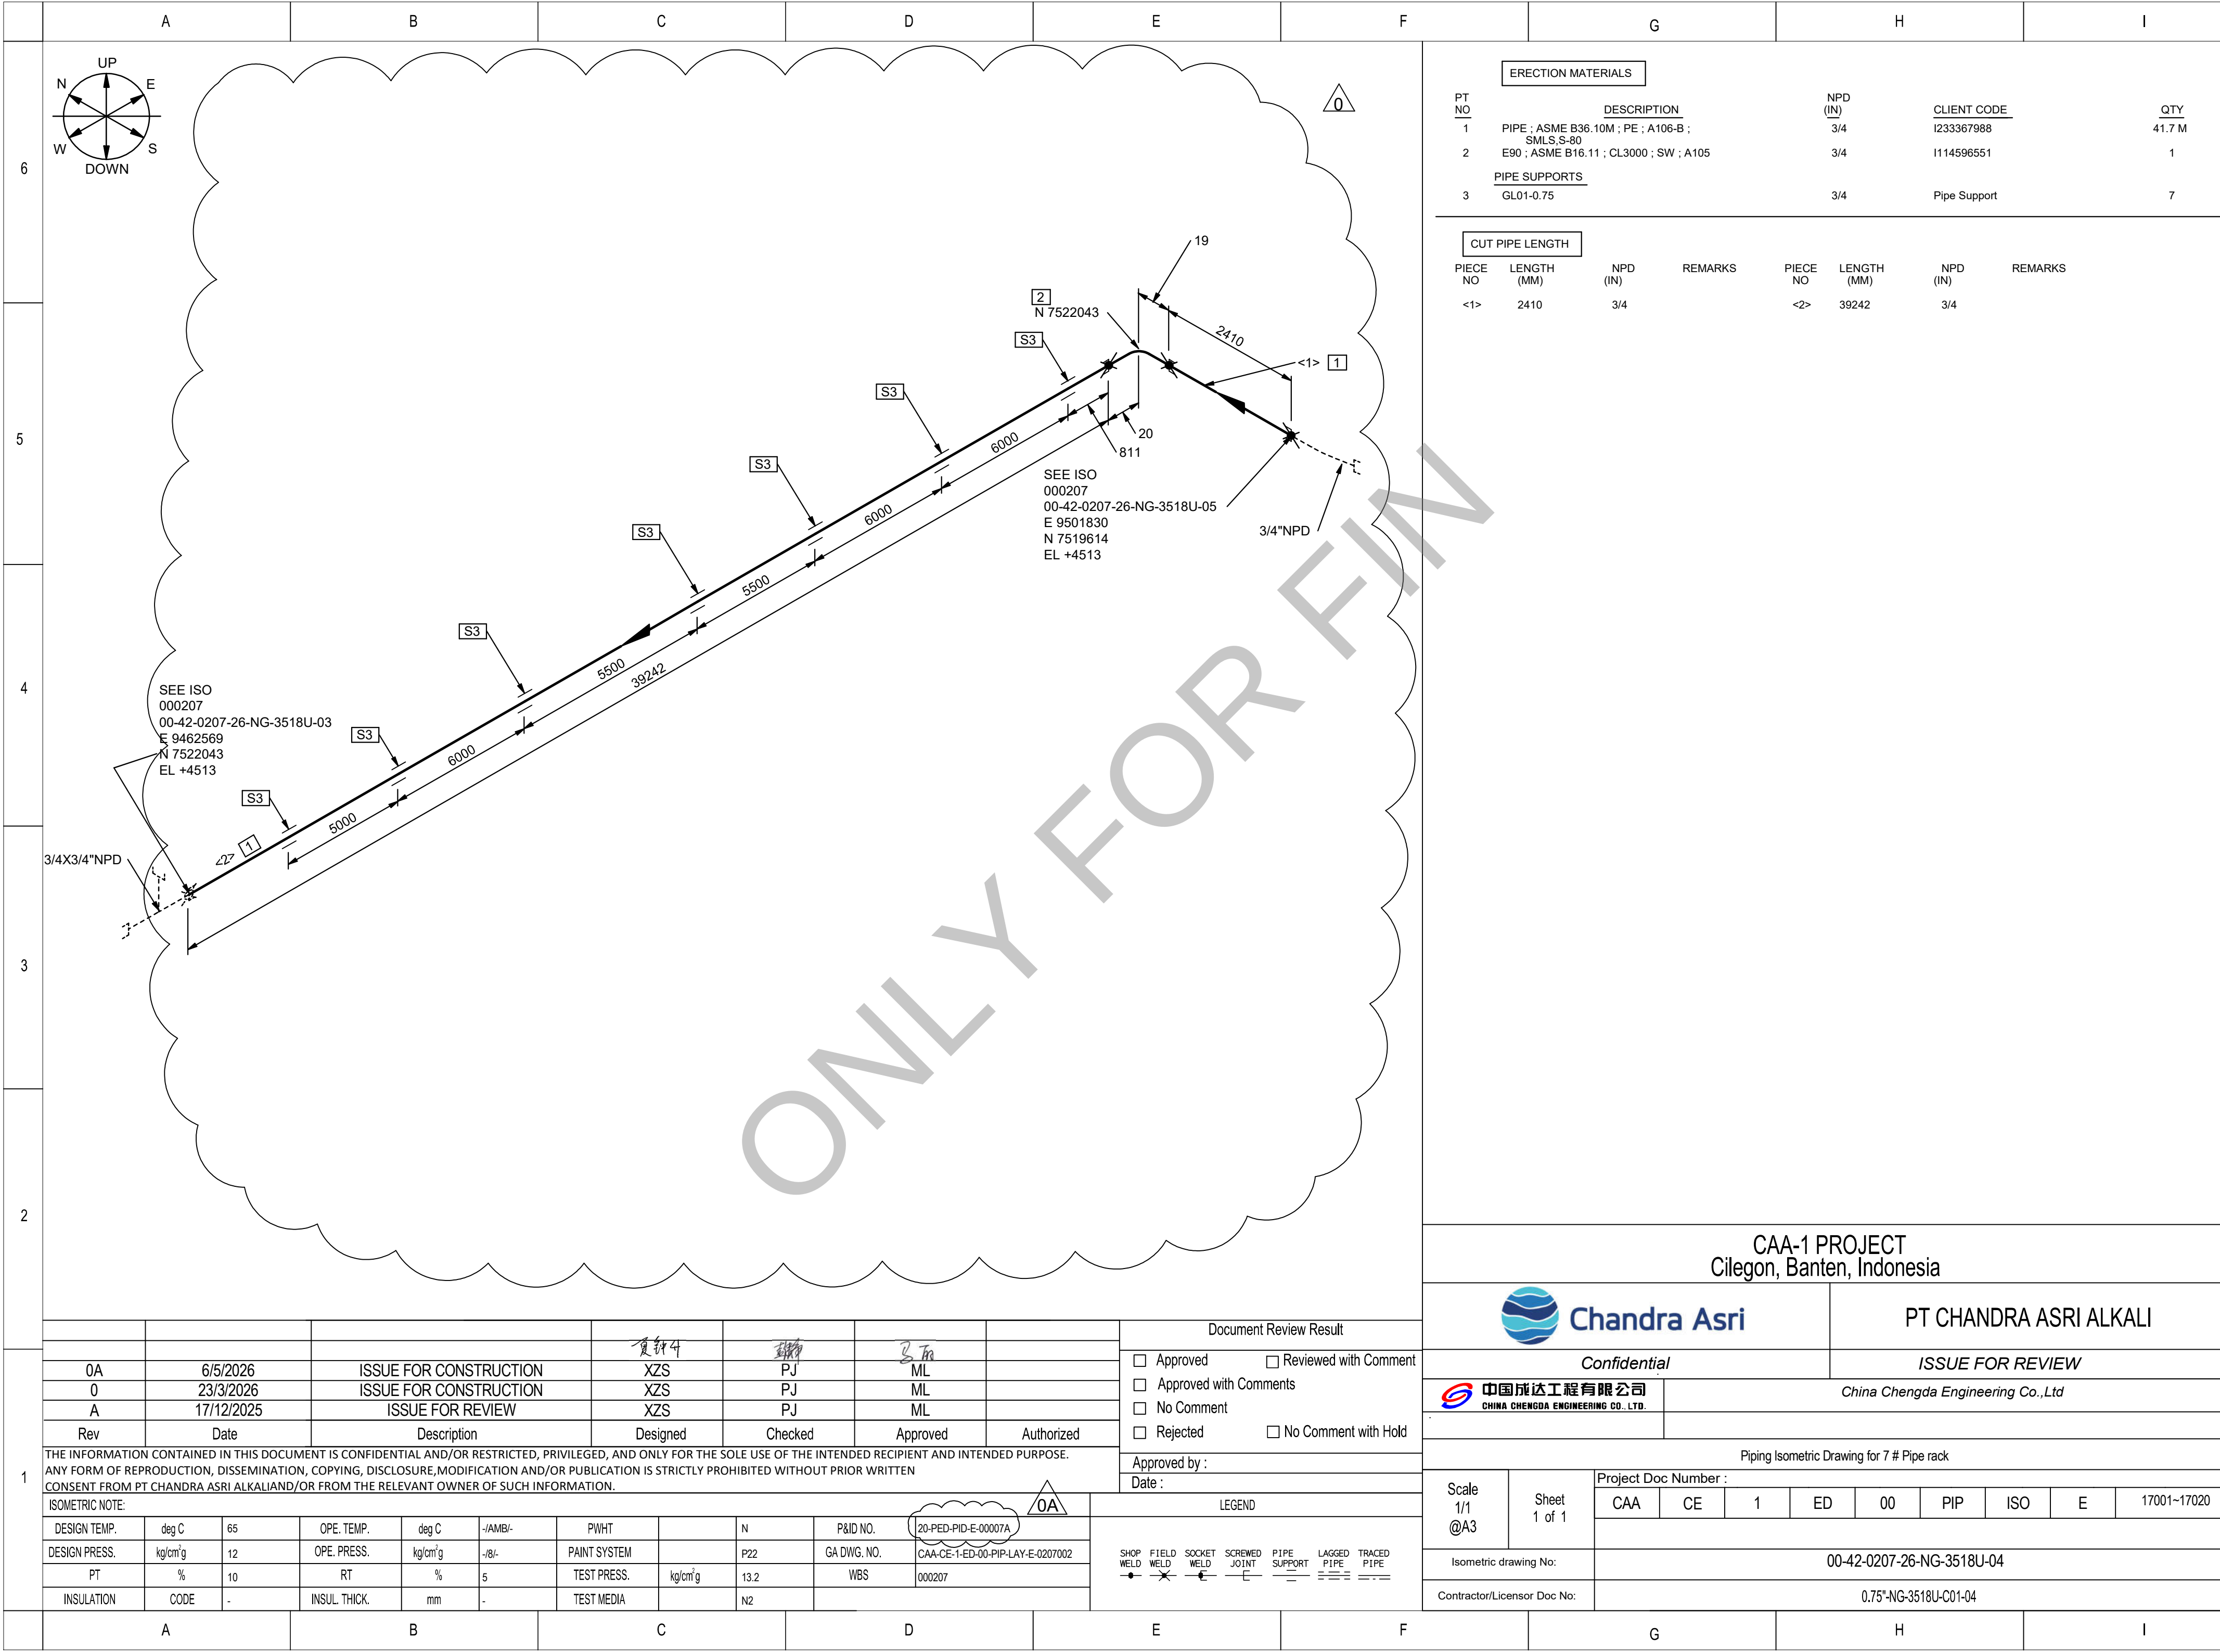

ERECTION MATERIALS				
PT NO	DESCRIPTION	NPD (IN)	CLIENT CODE	QTY
1	PIPE ; ASME B36.10M ; PE ; A106-B ; SMLS,S-80	3/4	I233367988	41.7 M
2	E90 ; ASME B16.11 ; CL3000 ; SW ; A105	3/4	I114596551	1
PIPE SUPPORTS				
3	GL01-0.75	3/4	Pipe Support	7

CUT PIPE LENGTH							
PIECE NO	LENGTH (MM)	NPD (IN)	REMARKS	PIECE NO	LENGTH (MM)	NPD (IN)	REMARKS
<1>	2410	3/4		<2>	39242	3/4	

CAA-1 PROJECT
Cilegon, Banten, Indonesia

Chandra Asri

PT CHANDRA ASRI ALKALI

Confidential

ISSUE FOR REVIEW

中国成达工程有限公司
CHINA CHENGDA ENGINEERING CO., LTD.

China Chengda Engineering Co.,Ltd

Piping Isometric Drawing for 7 # Pipe rack


Scale 1/1 @A3

Sheet 1 of 1

Project Doc Number : CAA CE 1 ED 00 PIP ISO E 17001~17020

Isometric drawing No: 00-42-0207-26-NG-3518U-04

Contractor/Licensor Doc No: 0.75"-NG-3518U-C01-04

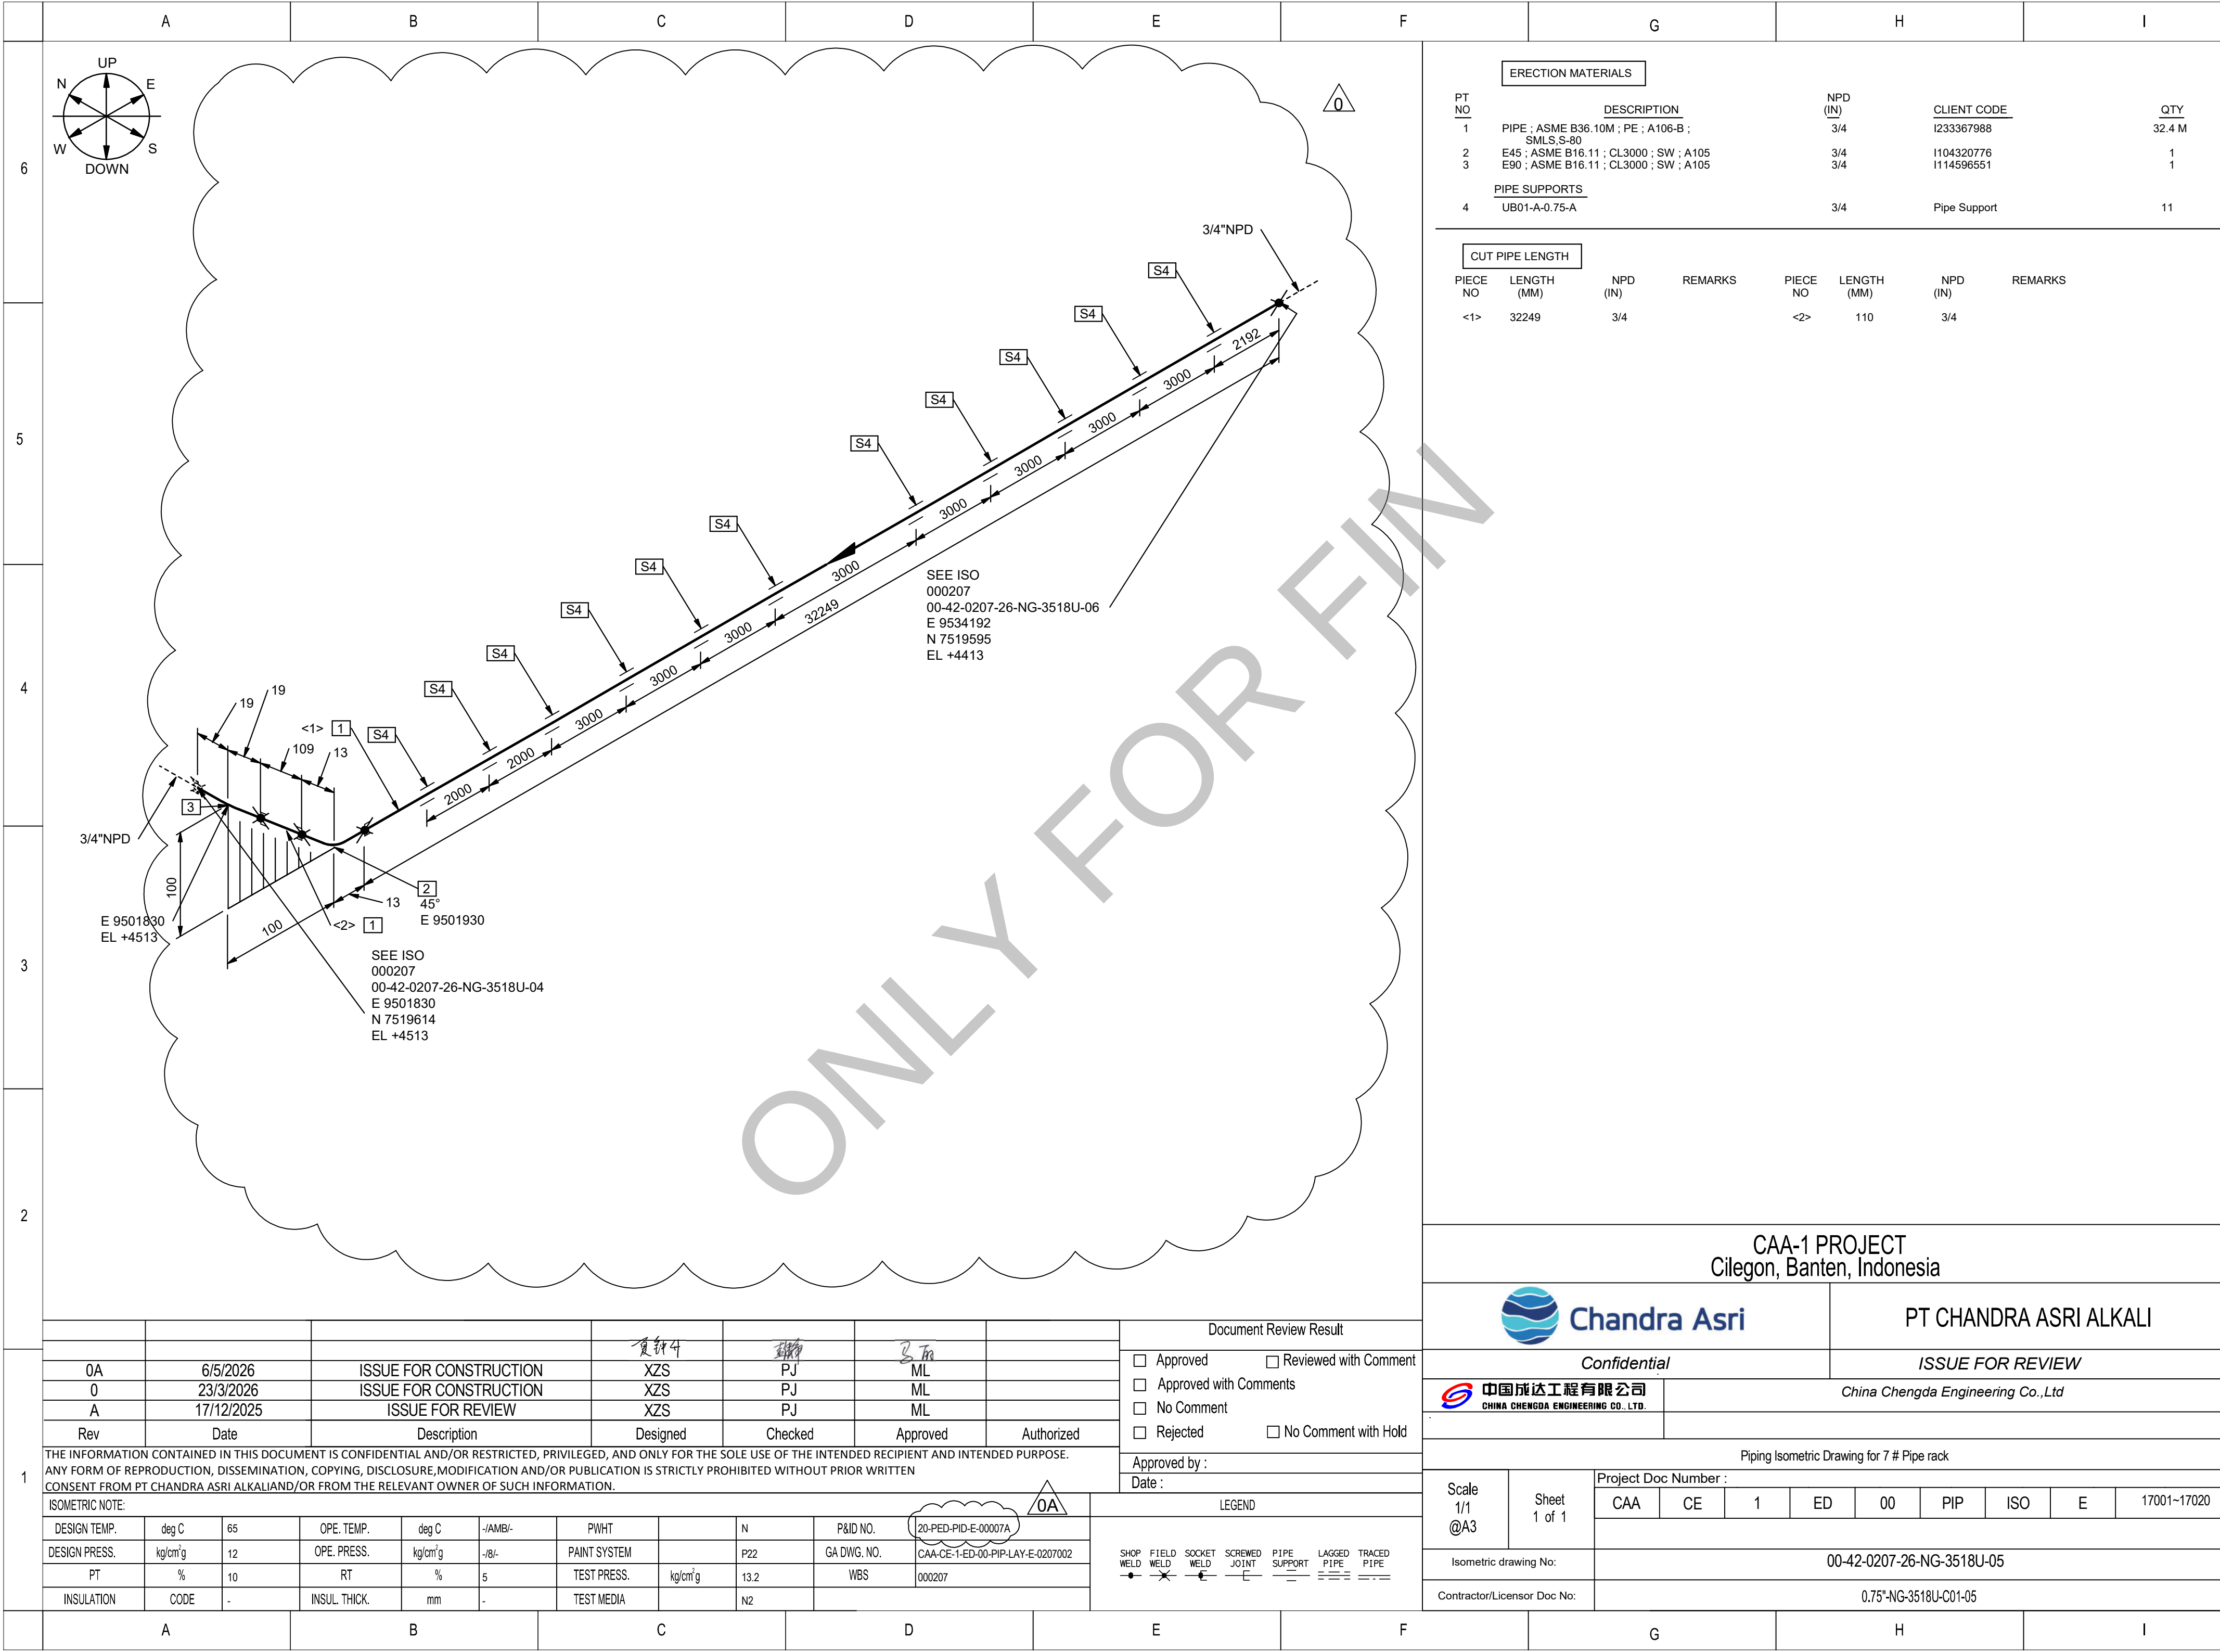

ERECTION MATERIALS				
PT NO	DESCRIPTION	NPD (IN)	CLIENT CODE	QTY
1	PIPE ; ASME B36.10M ; PE ; A106-B ; SMLS,S-80	3/4	I233367988	32.4 M
2	E45 ; ASME B16.11 ; CL3000 ; SW ; A105	3/4	I104320776	1
3	E90 ; ASME B16.11 ; CL3000 ; SW ; A105	3/4	I114596551	1
PIPE SUPPORTS				
4	UB01-A-0.75-A	3/4	Pipe Support	11

CUT PIPE LENGTH							
PIECE NO	LENGTH (MM)	NPD (IN)	REMARKS	PIECE NO	LENGTH (MM)	NPD (IN)	REMARKS
<1>	32249	3/4		<2>	110	3/4	


CAA-1 PROJECT
Cilegon, Banten, Indonesia

 Chandra Asri		PT CHANDRA ASRI ALKALI	
Confidential		ISSUE FOR REVIEW	
 中国成达工程有限公司 CHINA CHENGDA ENGINEERING CO., LTD.		China Chengda Engineering Co.,Ltd	

Document Review Result						
☐ Approved ☐ Reviewed with Comment						
☐ Approved with Comments						
☐ No Comment						
☐ Rejected ☐ No Comment with Hold						
Approved by :						
Date :						
LEGEND						
SHOP WELD	FIELD WELD	SOCKET WELD	SCREWED JOINT	PIPE SUPPORT	LAGGED PIPE	TRACED PIPE
						

DESIGN TEMP.	deg C	65	OPE. TEMP.	deg C	-/AMB/-	PWHT		N	P&ID NO.	20-PED-PID-E-00007A
DESIGN PRESS.	kg/cm²g	12	OPE. PRESS.	kg/cm²g	-/8/-	PAINT SYSTEM		P22	GA DWG. NO.	CAA-CE-1-ED-00-PIP-LAY-E-0207002
PT	%	10	RT	%	5	TEST PRESS.	kg/cm²g	13.2	WBS	000207
INSULATION	CODE	-	INSUL THICK.	mm	-	TEST MEDIA		N2		

THE INFORMATION CONTAINED IN THIS DOCUMENT IS CONFIDENTIAL AND/OR RESTRICTED, PRIVILEGED, AND ONLY FOR THE SOLE USE OF THE INTENDED RECIPIENT AND INTENDED PURPOSE. ANY FORM OF REPRODUCTION, DISSEMINATION, COPYING, DISCLOSURE,MODIFICATION AND/OR PUBLICATION IS STRICTLY PROHIBITED WITHOUT PRIOR WRITTEN CONSENT FROM PT CHANDRA ASRI ALKALIAND/OR FROM THE RELEVANT OWNER OF SUCH INFORMATION.										
ISOMETRIC NOTE:										
DESIGN TEMP.	deg C	65	OPE. TEMP.	deg C	-/AMB/-	PWHT		N	P&ID NO.	20-PED-PID-E-00007A
DESIGN PRESS.	kg/cm²g	12	OPE. PRESS.	kg/cm²g	-/8/-	PAINT SYSTEM		P22	GA DWG. NO.	CAA-CE-1-ED-00-PIP-LAY-E-0207002
PT	%	10	RT	%	5	TEST PRESS.	kg/cm²g	13.2	WBS	000207
INSULATION	CODE	-	INSUL THICK.	mm	-	TEST MEDIA		N2		

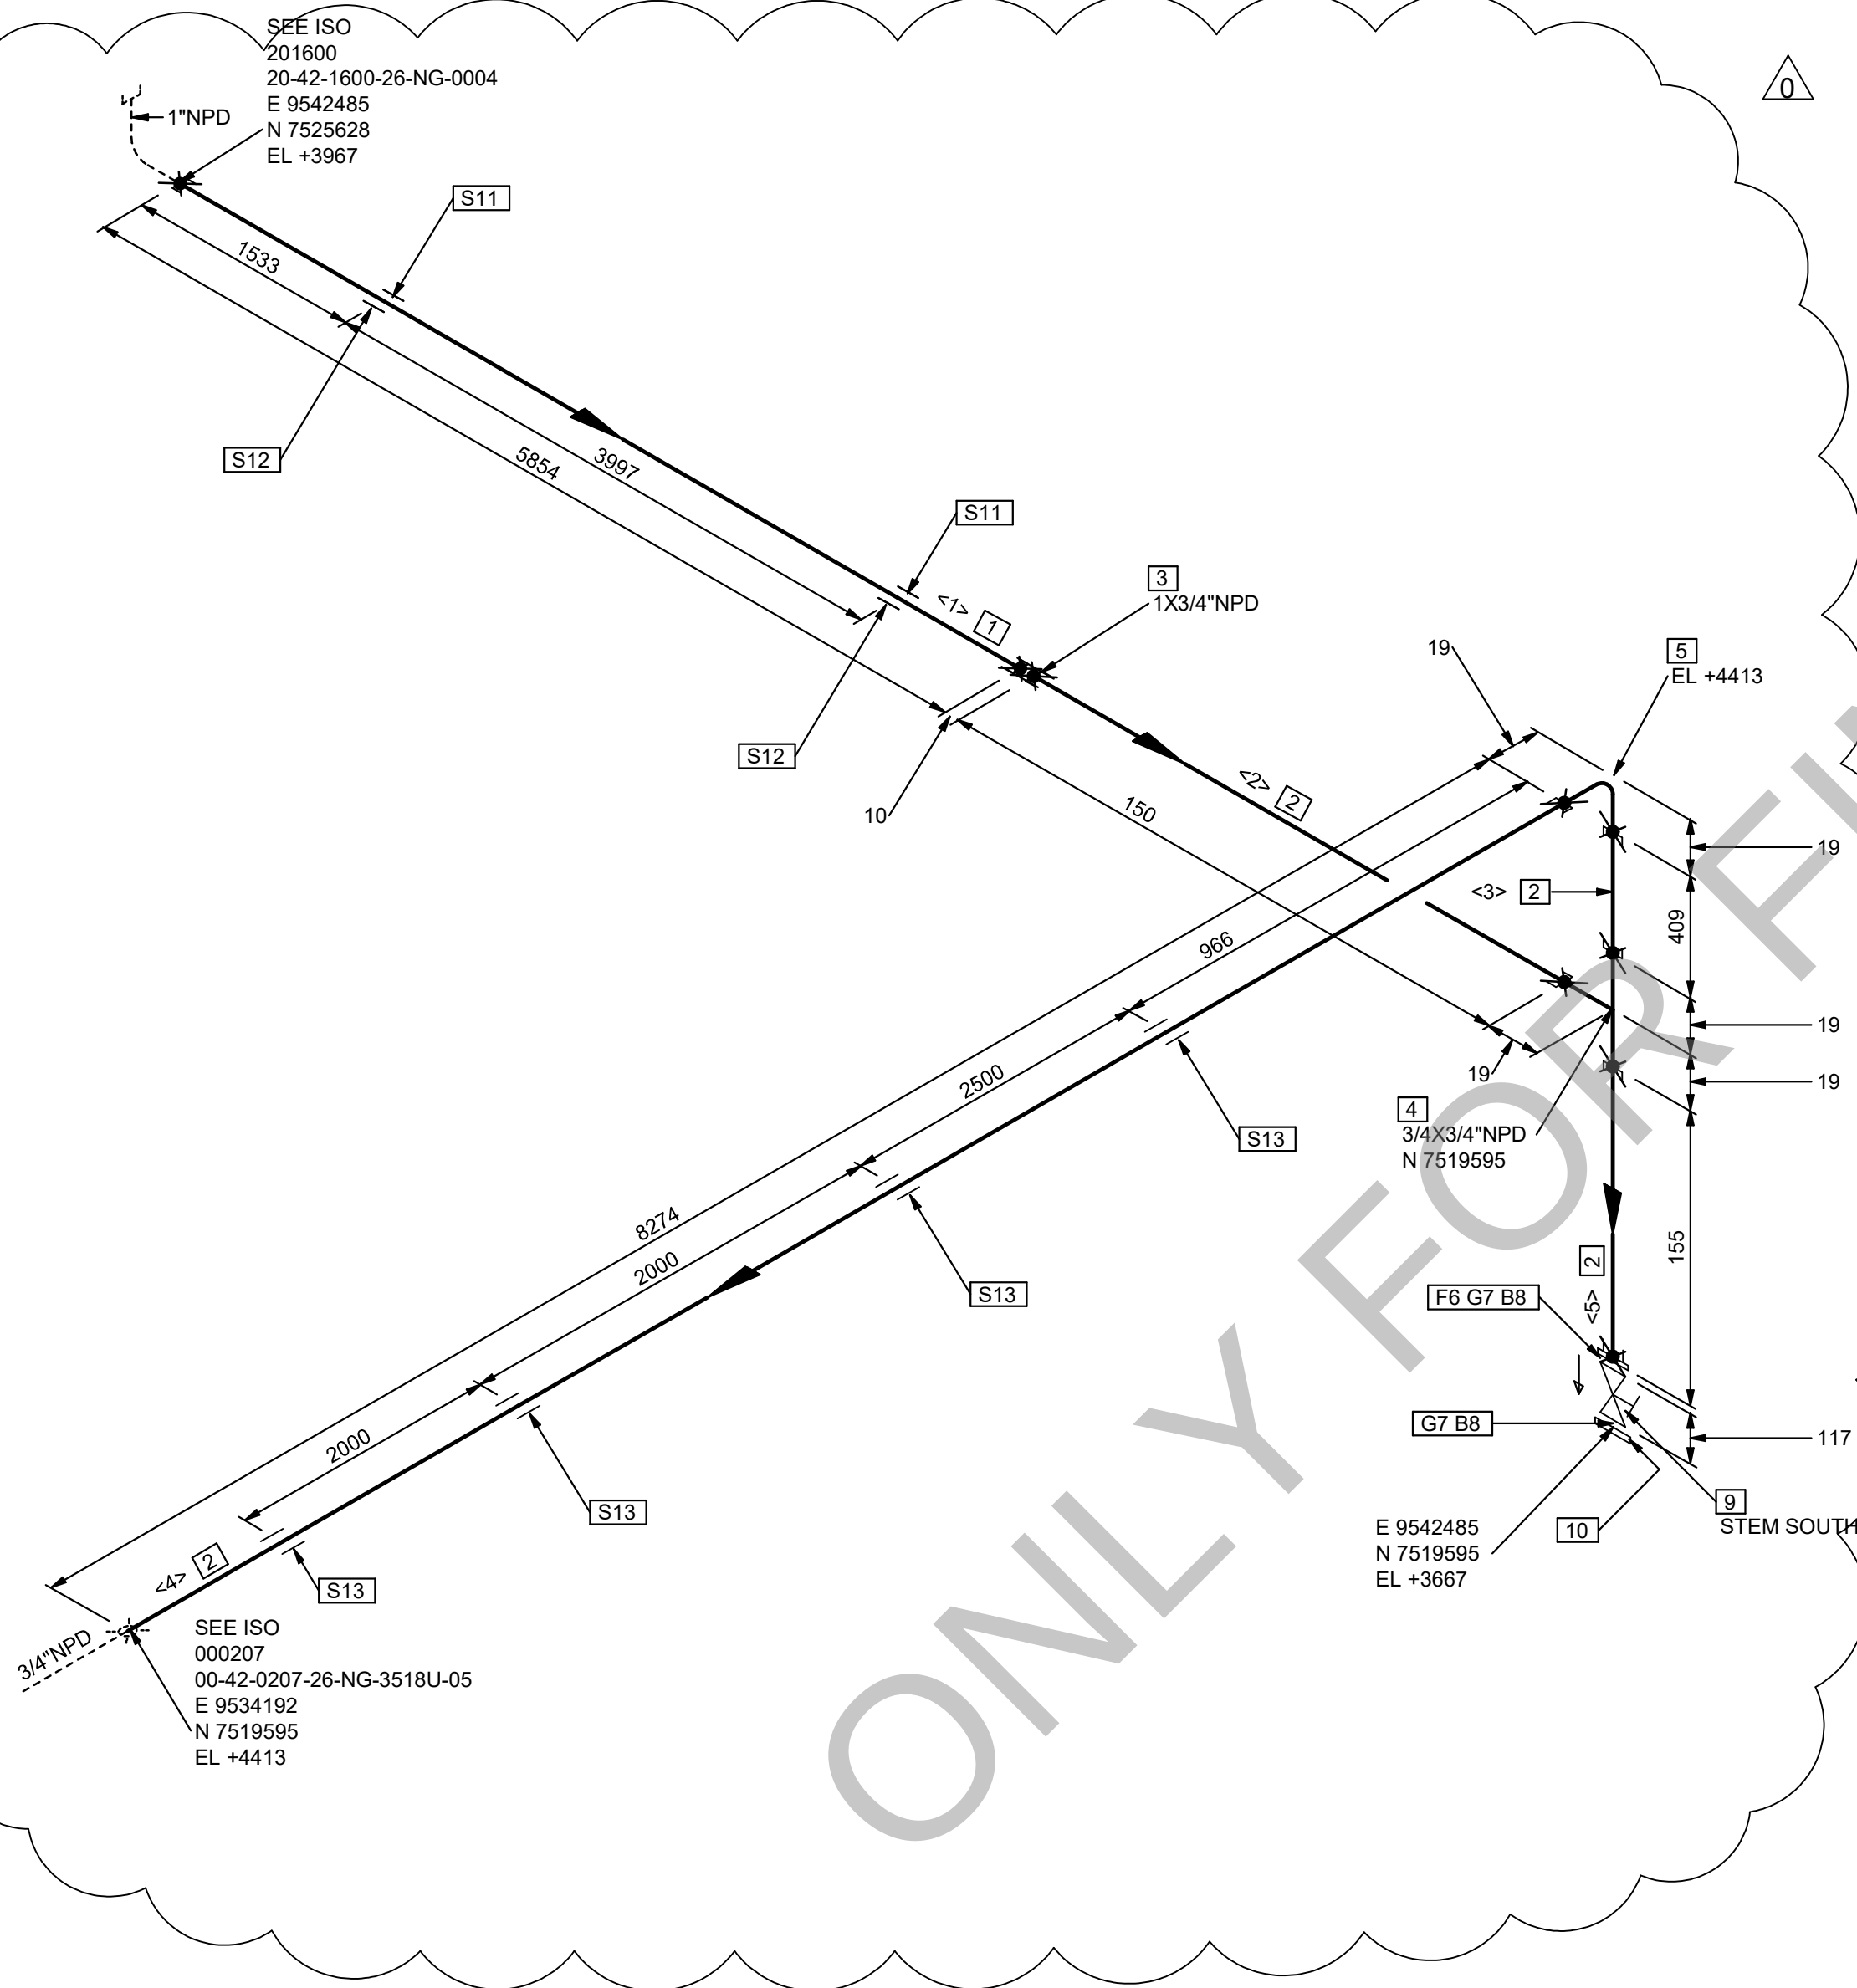


CUT PIPE LENGTH							
PIECE NO	LENGTH (MM)	NPD (IN)	REMARKS	PIECE NO	LENGTH (MM)	NPD (IN)	REMARKS
<1>	5854	1		<2>	150	3/4	
<3>	409	3/4		<4>	8274	3/4	
<5>	150	3/4					

1"-NG-3518U-C01-06

0A


LEGEND						
SHOP WELD	FIELD WELD	SOCKET WELD	SCREWED JOINT	PIPE SUPPORT	LAGGED PIPE	TRACED PIPE

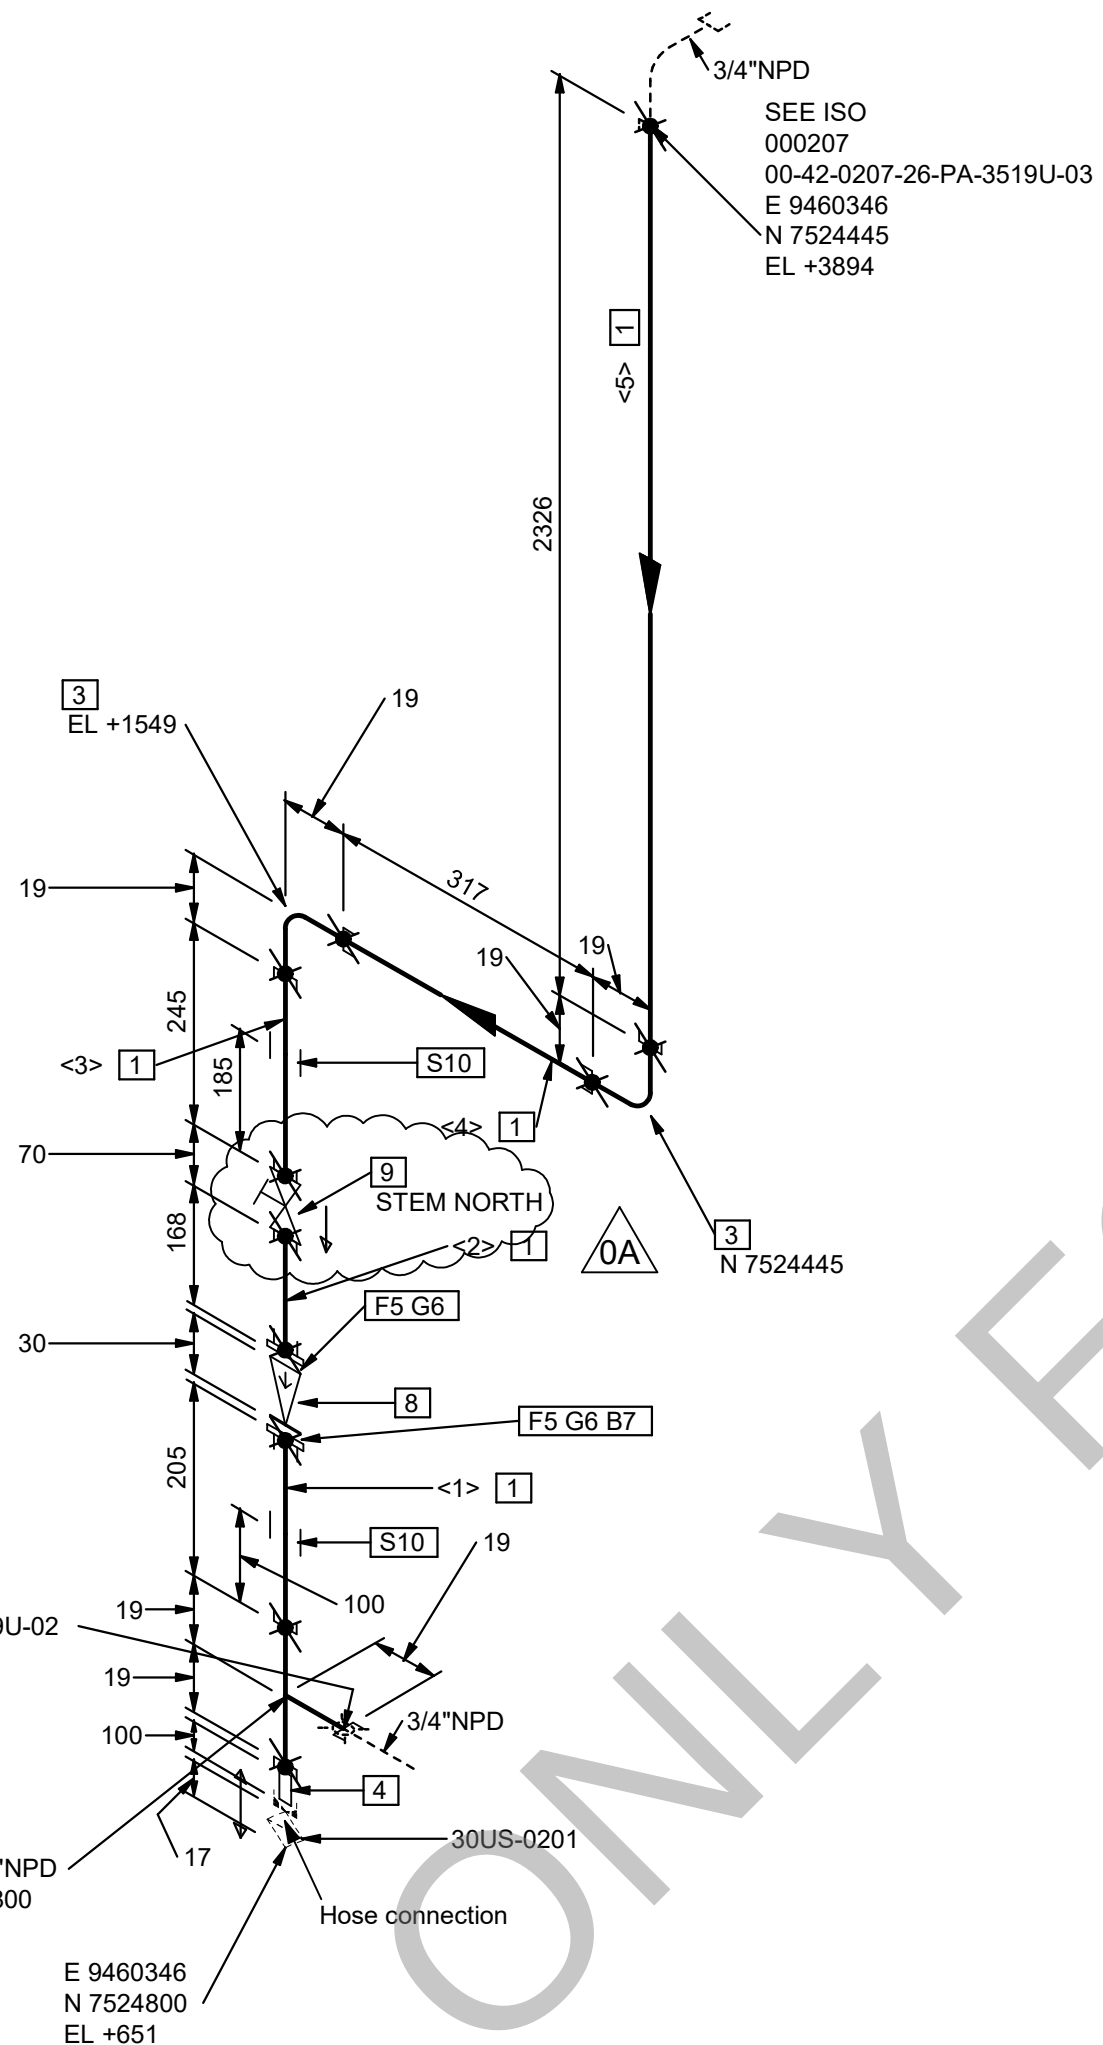

CUT PIPE LENGTH							
PIECE NO	LENGTH (MM)	NPD (IN)	REMARKS	PIECE NO	LENGTH (MM)	NPD (IN)	REMARKS
<1>	200	3/4		<2>	163	3/4	
<3>	245	3/4		<4>	317	3/4	
<5>	2326	3/4					

0.75"-PA-3519U-1C2-01

ISOMETRIC NOTE:										
DESIGN TEMP.	deg C	65	OPE. TEMP.	deg C	-/AMB/-	PWHT		N	P&ID NO.	20-PED-PID-E-00009
DESIGN PRESS.	kg/cm ² g	10.5	OPE. PRESS.	kg/cm ² g	-/7.5/-	PAINT SYSTEM		P22	GA DWG. NO.	CAA-CE-1-ED-00-PIP-LAY-E-0207002
PT	%	-	RT	%	2	TEST PRESS.	kg/cm ² g	15.75	WBS	000207
INSULATION	CODE	-	INSUL. THICK.	mm	-	TEST MEDIA		WATER		

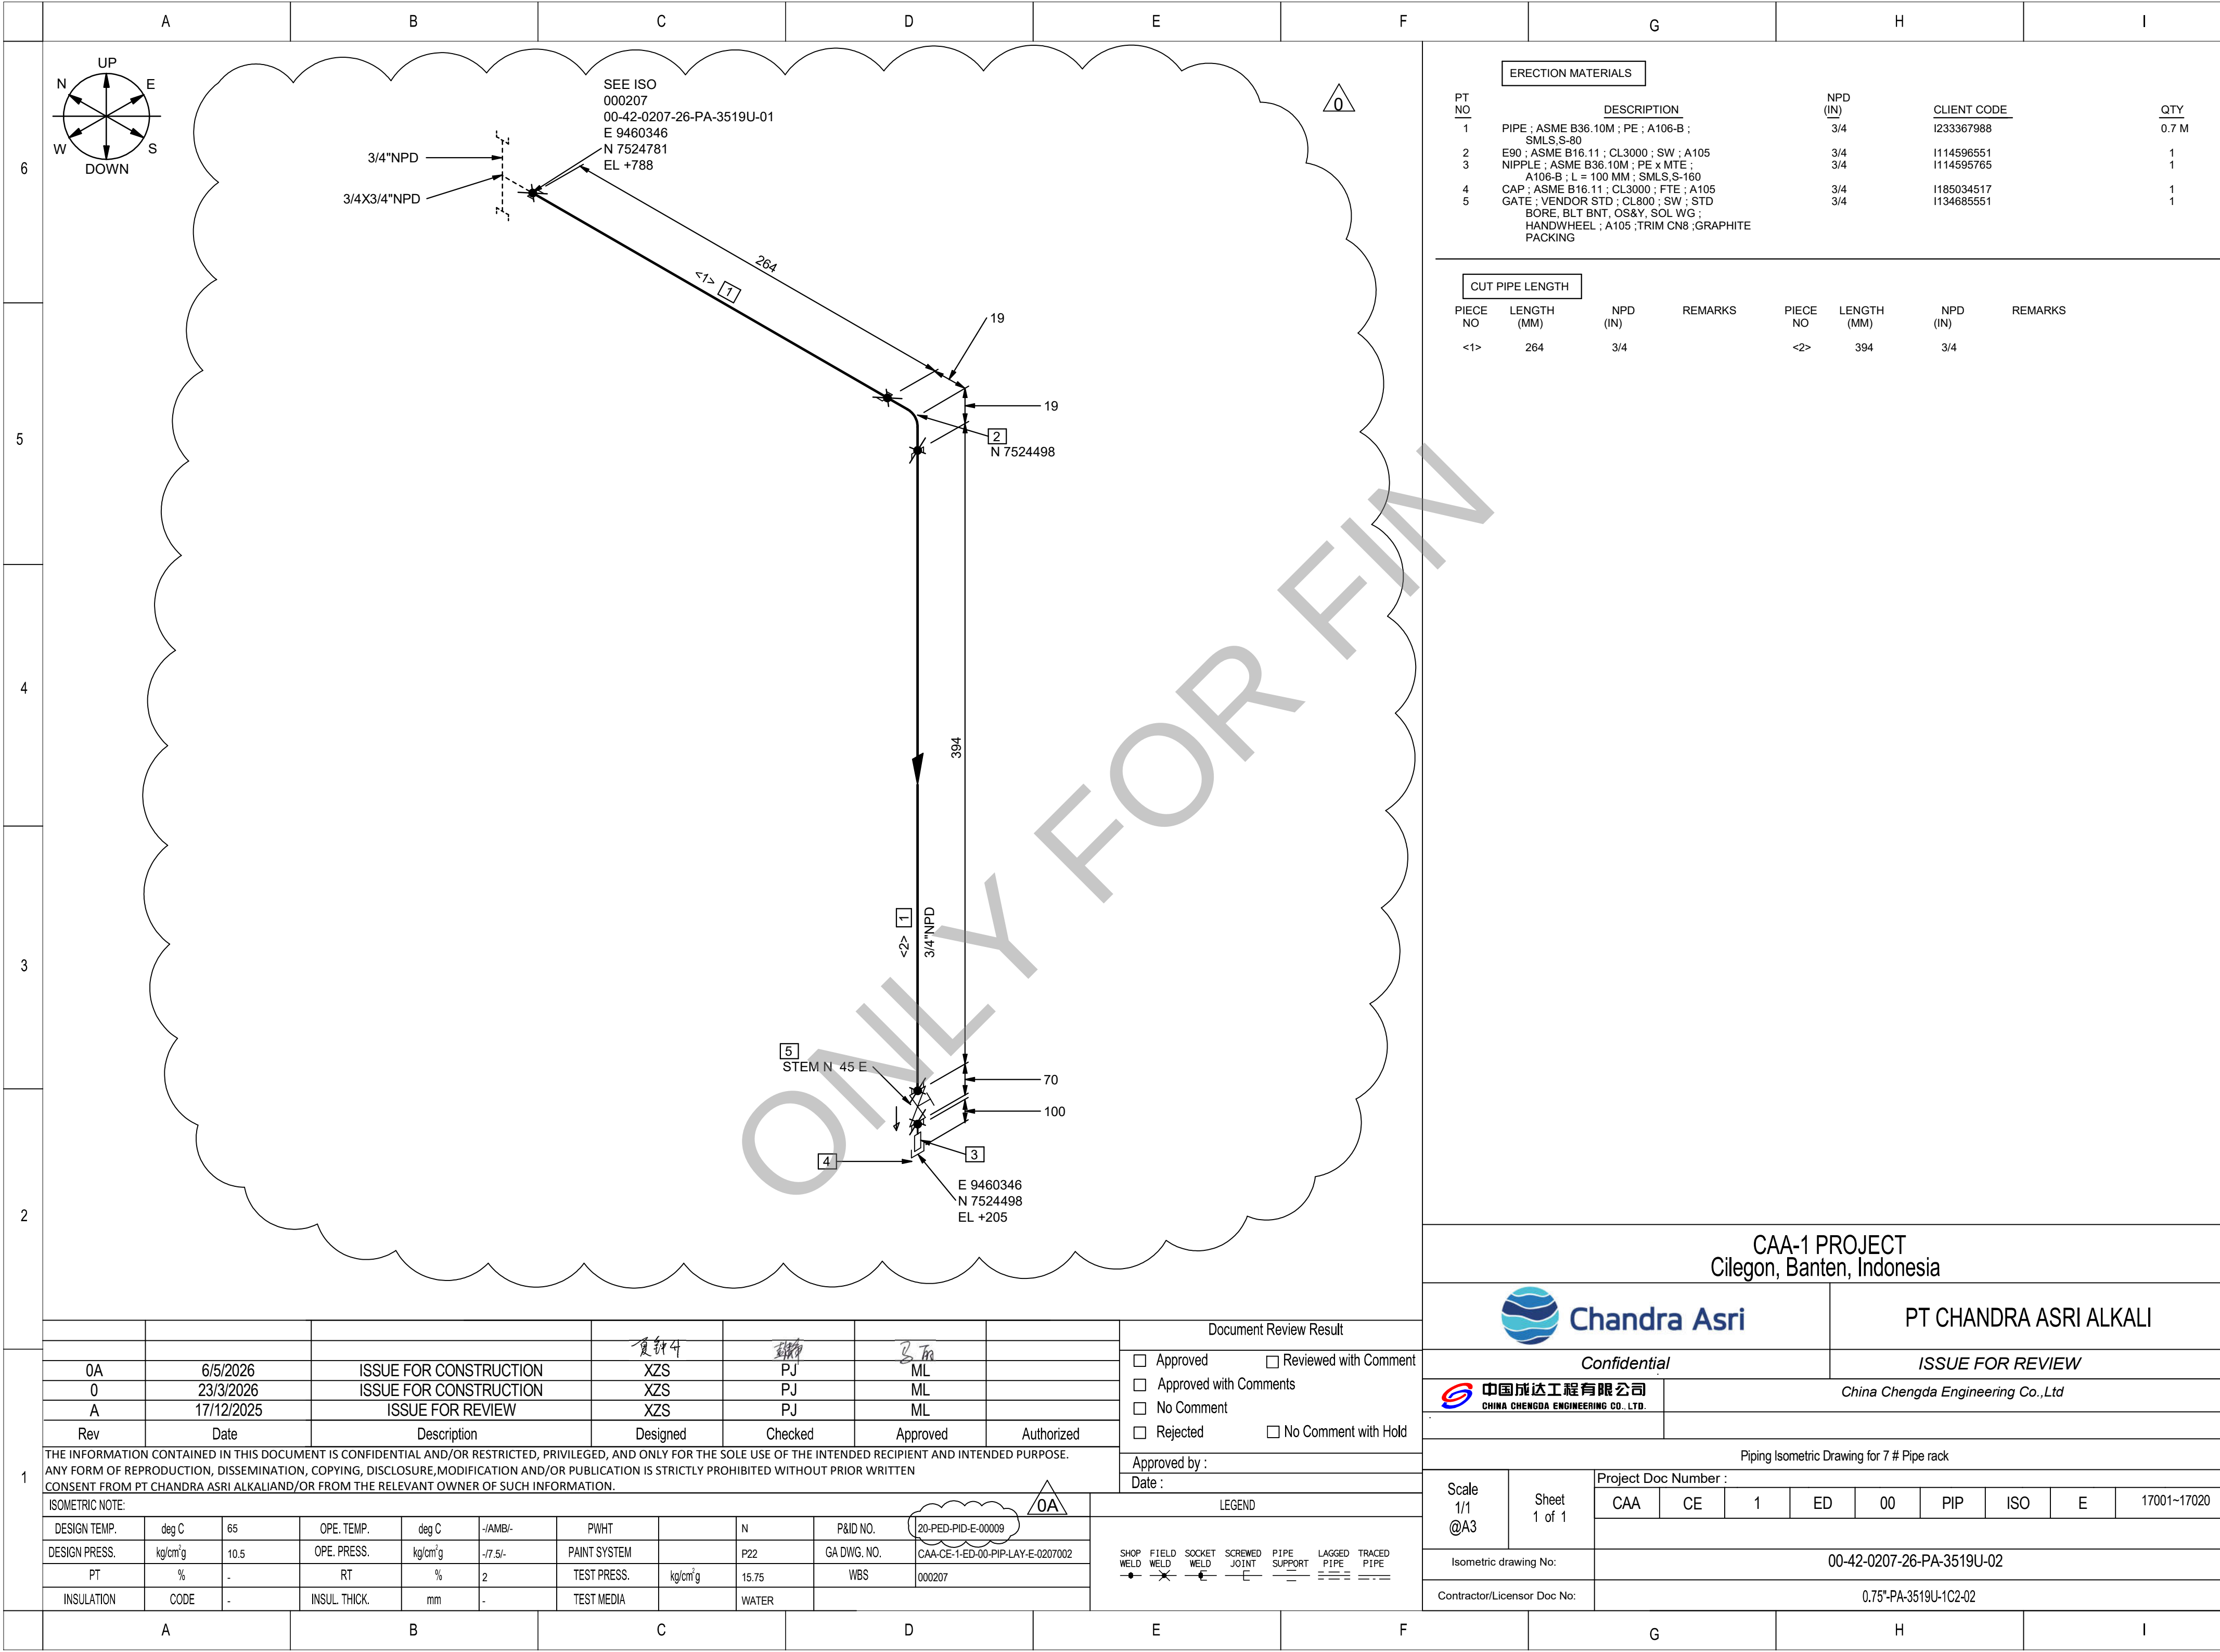

ERECTION MATERIALS				
PT NO	DESCRIPTION	NPD (IN)	CLIENT CODE	QTY
1	PIPE ; ASME B36.10M ; PE ; A106-B ; SMLS,S-80	3/4	I233367988	0.7 M
2	E90 ; ASME B16.11 ; CL3000 ; SW ; A105	3/4	I114596551	1
3	NIPPLE ; ASME B36.10M ; PE x MTE ; A106-B ; L = 100 MM ; SMLS,S-160	3/4	I114595765	1
4	CAP ; ASME B16.11 ; CL3000 ; FTE ; A105	3/4	I185034517	1
5	GATE ; VENDOR STD ; CL800 ; SW ; STD BORE, BLT BNT, OS&Y, SOL WG ; HANDWHEEL ; A105 ;TRIM CN8 ;GRAPHITE PACKING	3/4	I134685551	1

CUT PIPE LENGTH							
PIECE NO	LENGTH (MM)	NPD (IN)	REMARKS	PIECE NO	LENGTH (MM)	NPD (IN)	REMARKS
<1>	264	3/4		<2>	394	3/4	

CAA-1 PROJECT
Cilegon, Banten, Indonesia

Chandra Asri

PT CHANDRA ASRI ALKALI

Confidential

ISSUE FOR REVIEW

中国成达工程有限公司
CHINA CHENGDA ENGINEERING CO., LTD.

China Chengda Engineering Co.,Ltd

Piping Isometric Drawing for 7 # Pipe rack

Scale
1/1
@A3

Sheet
1 of 1


Project Doc Number :
CAA CE 1 ED 00 PIP ISO E 17001~17020

Isometric drawing No:

00-42-0207-26-PA-3519U-02

Contractor/Licensor Doc No:

0.75°-PA-3519U-1C2-02

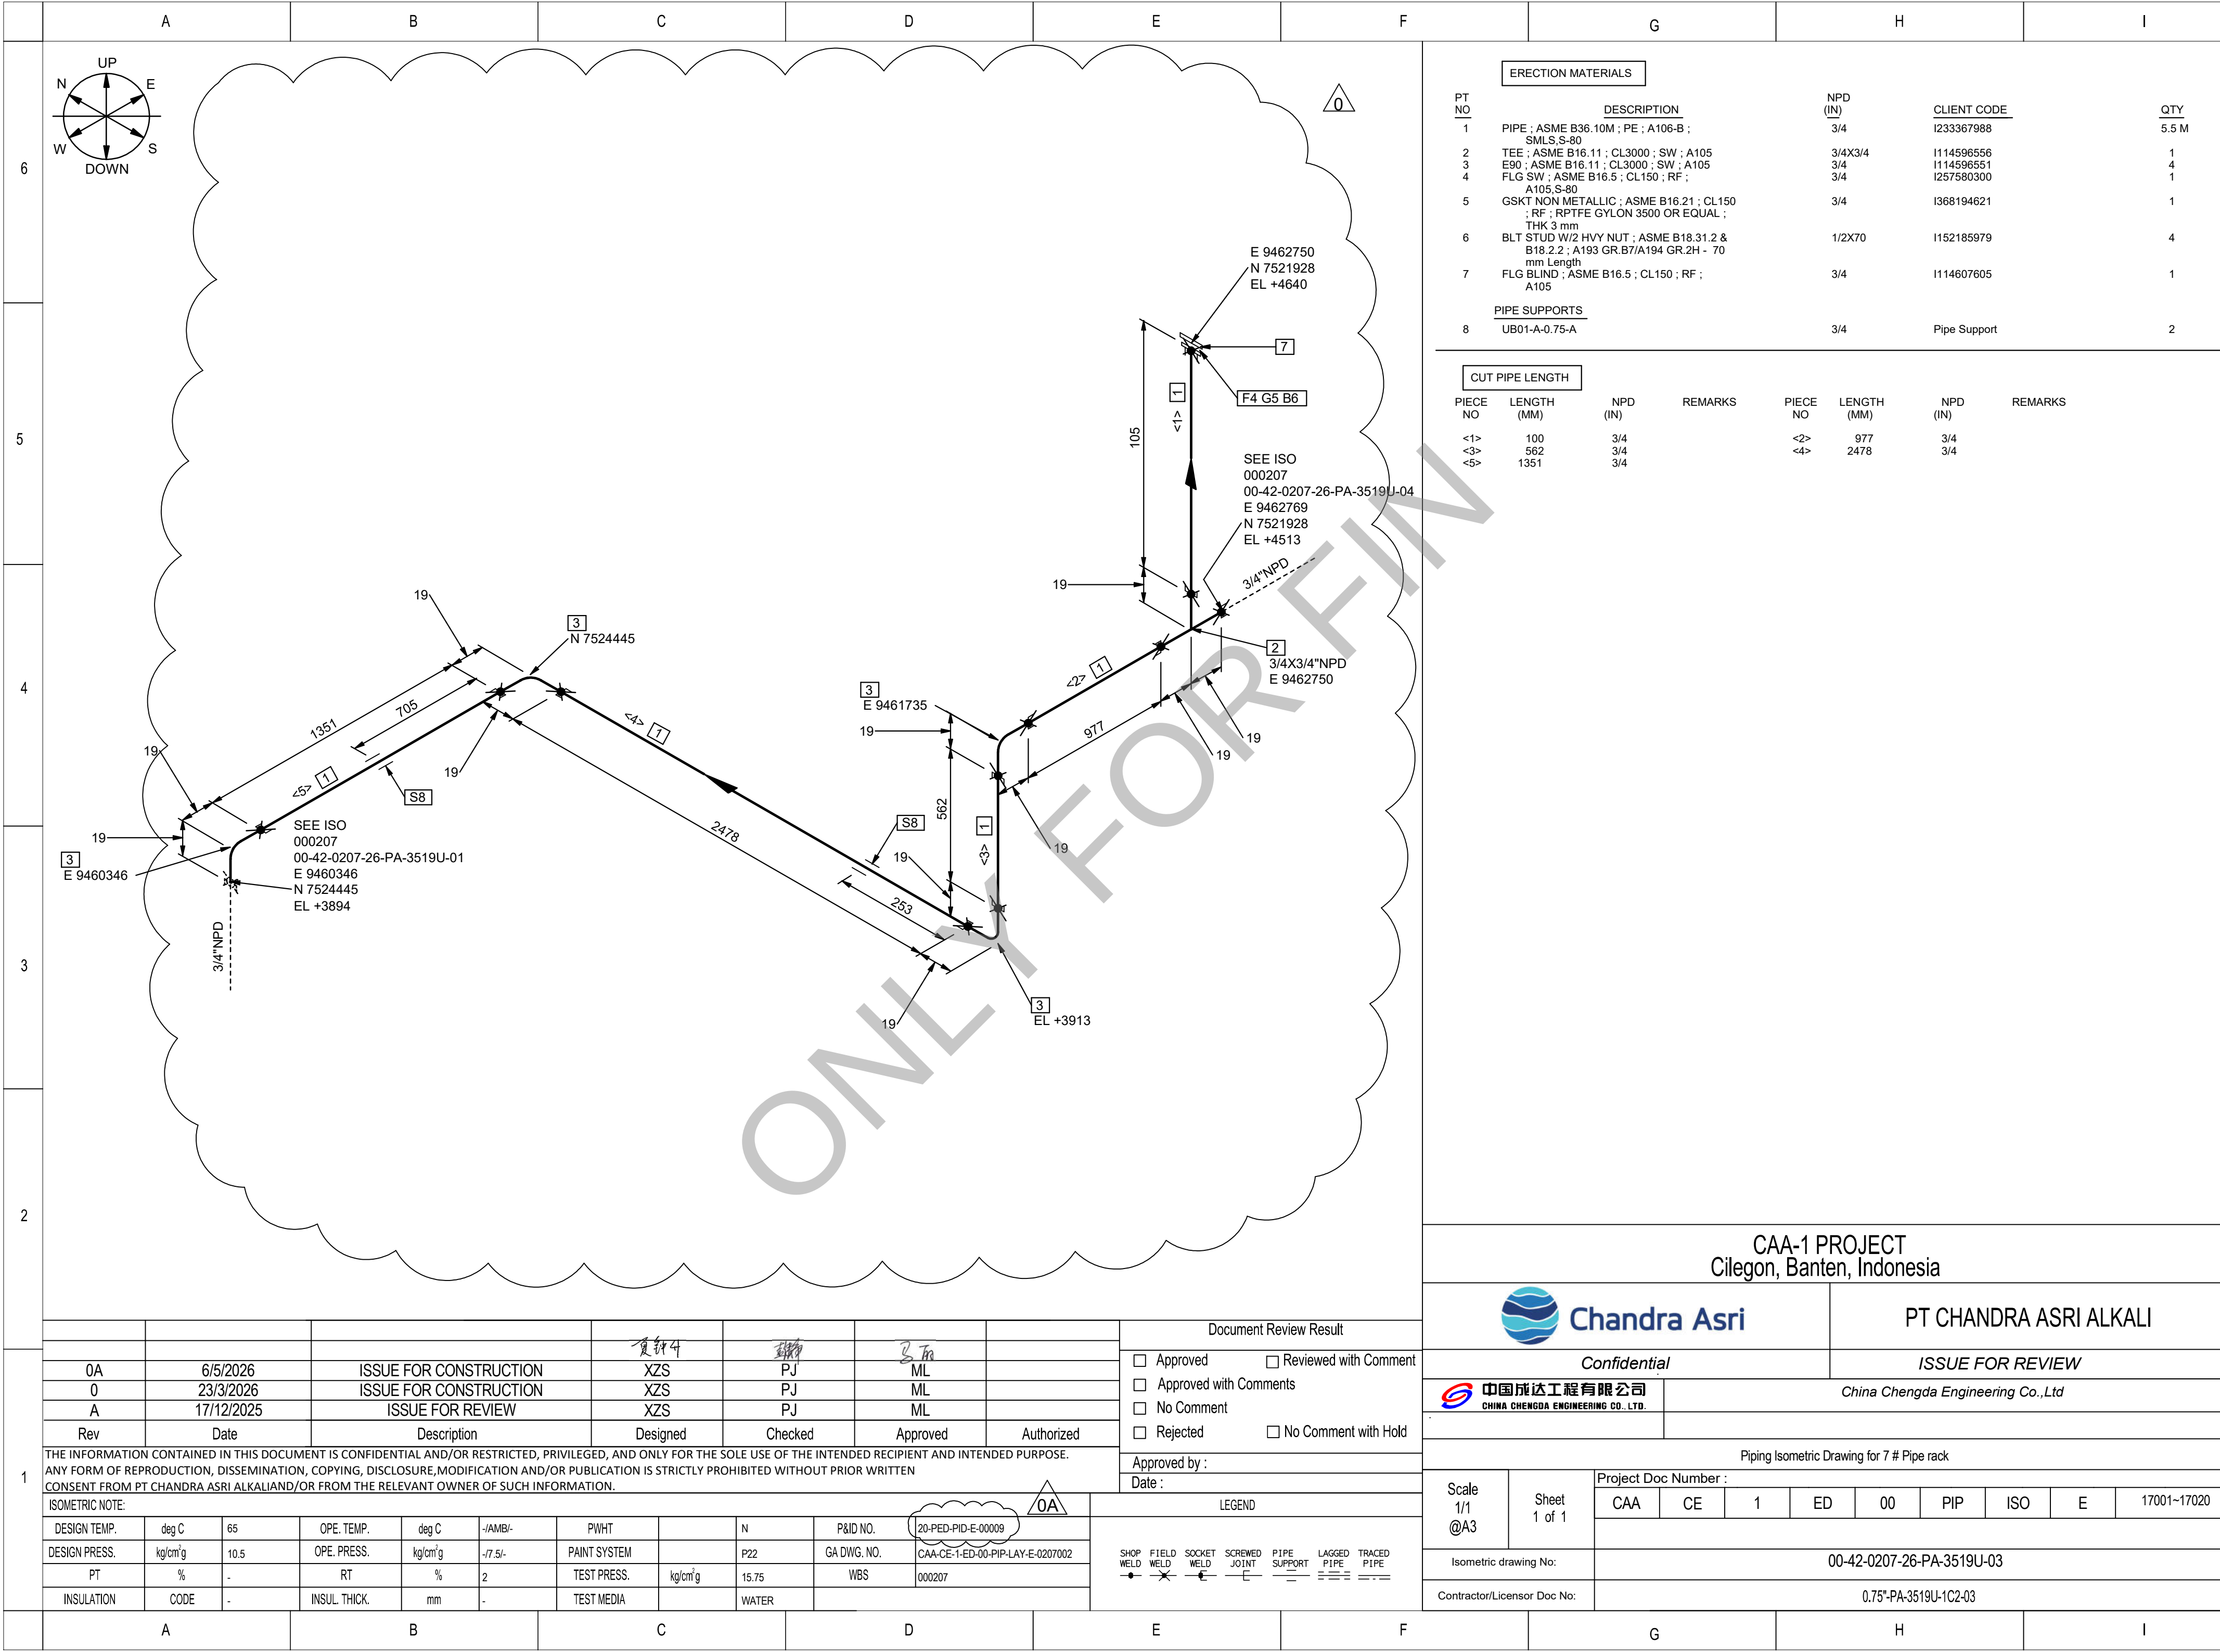

ERECTION MATERIALS				
PT NO	DESCRIPTION	NPD (IN)	CLIENT CODE	QTY
1	PIPE ; ASME B36.10M ; PE ; A106-B ; SMLS,S-80	3/4	I233367988	5.5 M
2	TEE ; ASME B16.11 ; CL3000 ; SW ; A105	3/4X3/4	I114596556	1
3	E90 ; ASME B16.11 ; CL3000 ; SW ; A105	3/4	I114596551	4
4	FLG SW ; ASME B16.5 ; CL150 ; RF ; A105,S-80	3/4	I257580300	1
5	GSKT NON METALLIC ; ASME B16.21 ; CL150 ; RF ; RPTFE GYLON 3500 OR EQUAL ; THK 3 mm	3/4	I368194621	1
6	BLT STUD W/2 HVY NUT ; ASME B18.31.2 & B18.2.2 ; A193 GR.B7/A194 GR.2H - 70 mm Length	1/2X70	I152185979	4
7	FLG BLIND ; ASME B16.5 ; CL150 ; RF ; A105	3/4	I114607605	1
PIPE SUPPORTS				
8	UB01-A-0.75-A	3/4	Pipe Support	2

CUT PIPE LENGTH							
PIECE NO	LENGTH (MM)	NPD (IN)	REMARKS	PIECE NO	LENGTH (MM)	NPD (IN)	REMARKS
<1>	100	3/4		<2>	977	3/4	
<3>	562	3/4		<4>	2478	3/4	
<5>	1351	3/4					

CAA-1 PROJECT
Cilegon, Banten, Indonesia



PT CHANDRA ASRI ALKALI

Confidential

ISSUE FOR REVIEW



China Chengda Engineering Co.,Ltd

Piping Isometric Drawing for 7 # Pipe rack

Scale
1/1
@A3

Sheet
1 of 1

Project Doc Number :


CAA CE 1 ED 00 PIP ISO E 17001-17020

Isometric drawing No:

00-42-0207-26-PA-3519U-03

Contractor/Licensor Doc No:

0.75"-PA-3519U-1C2-03

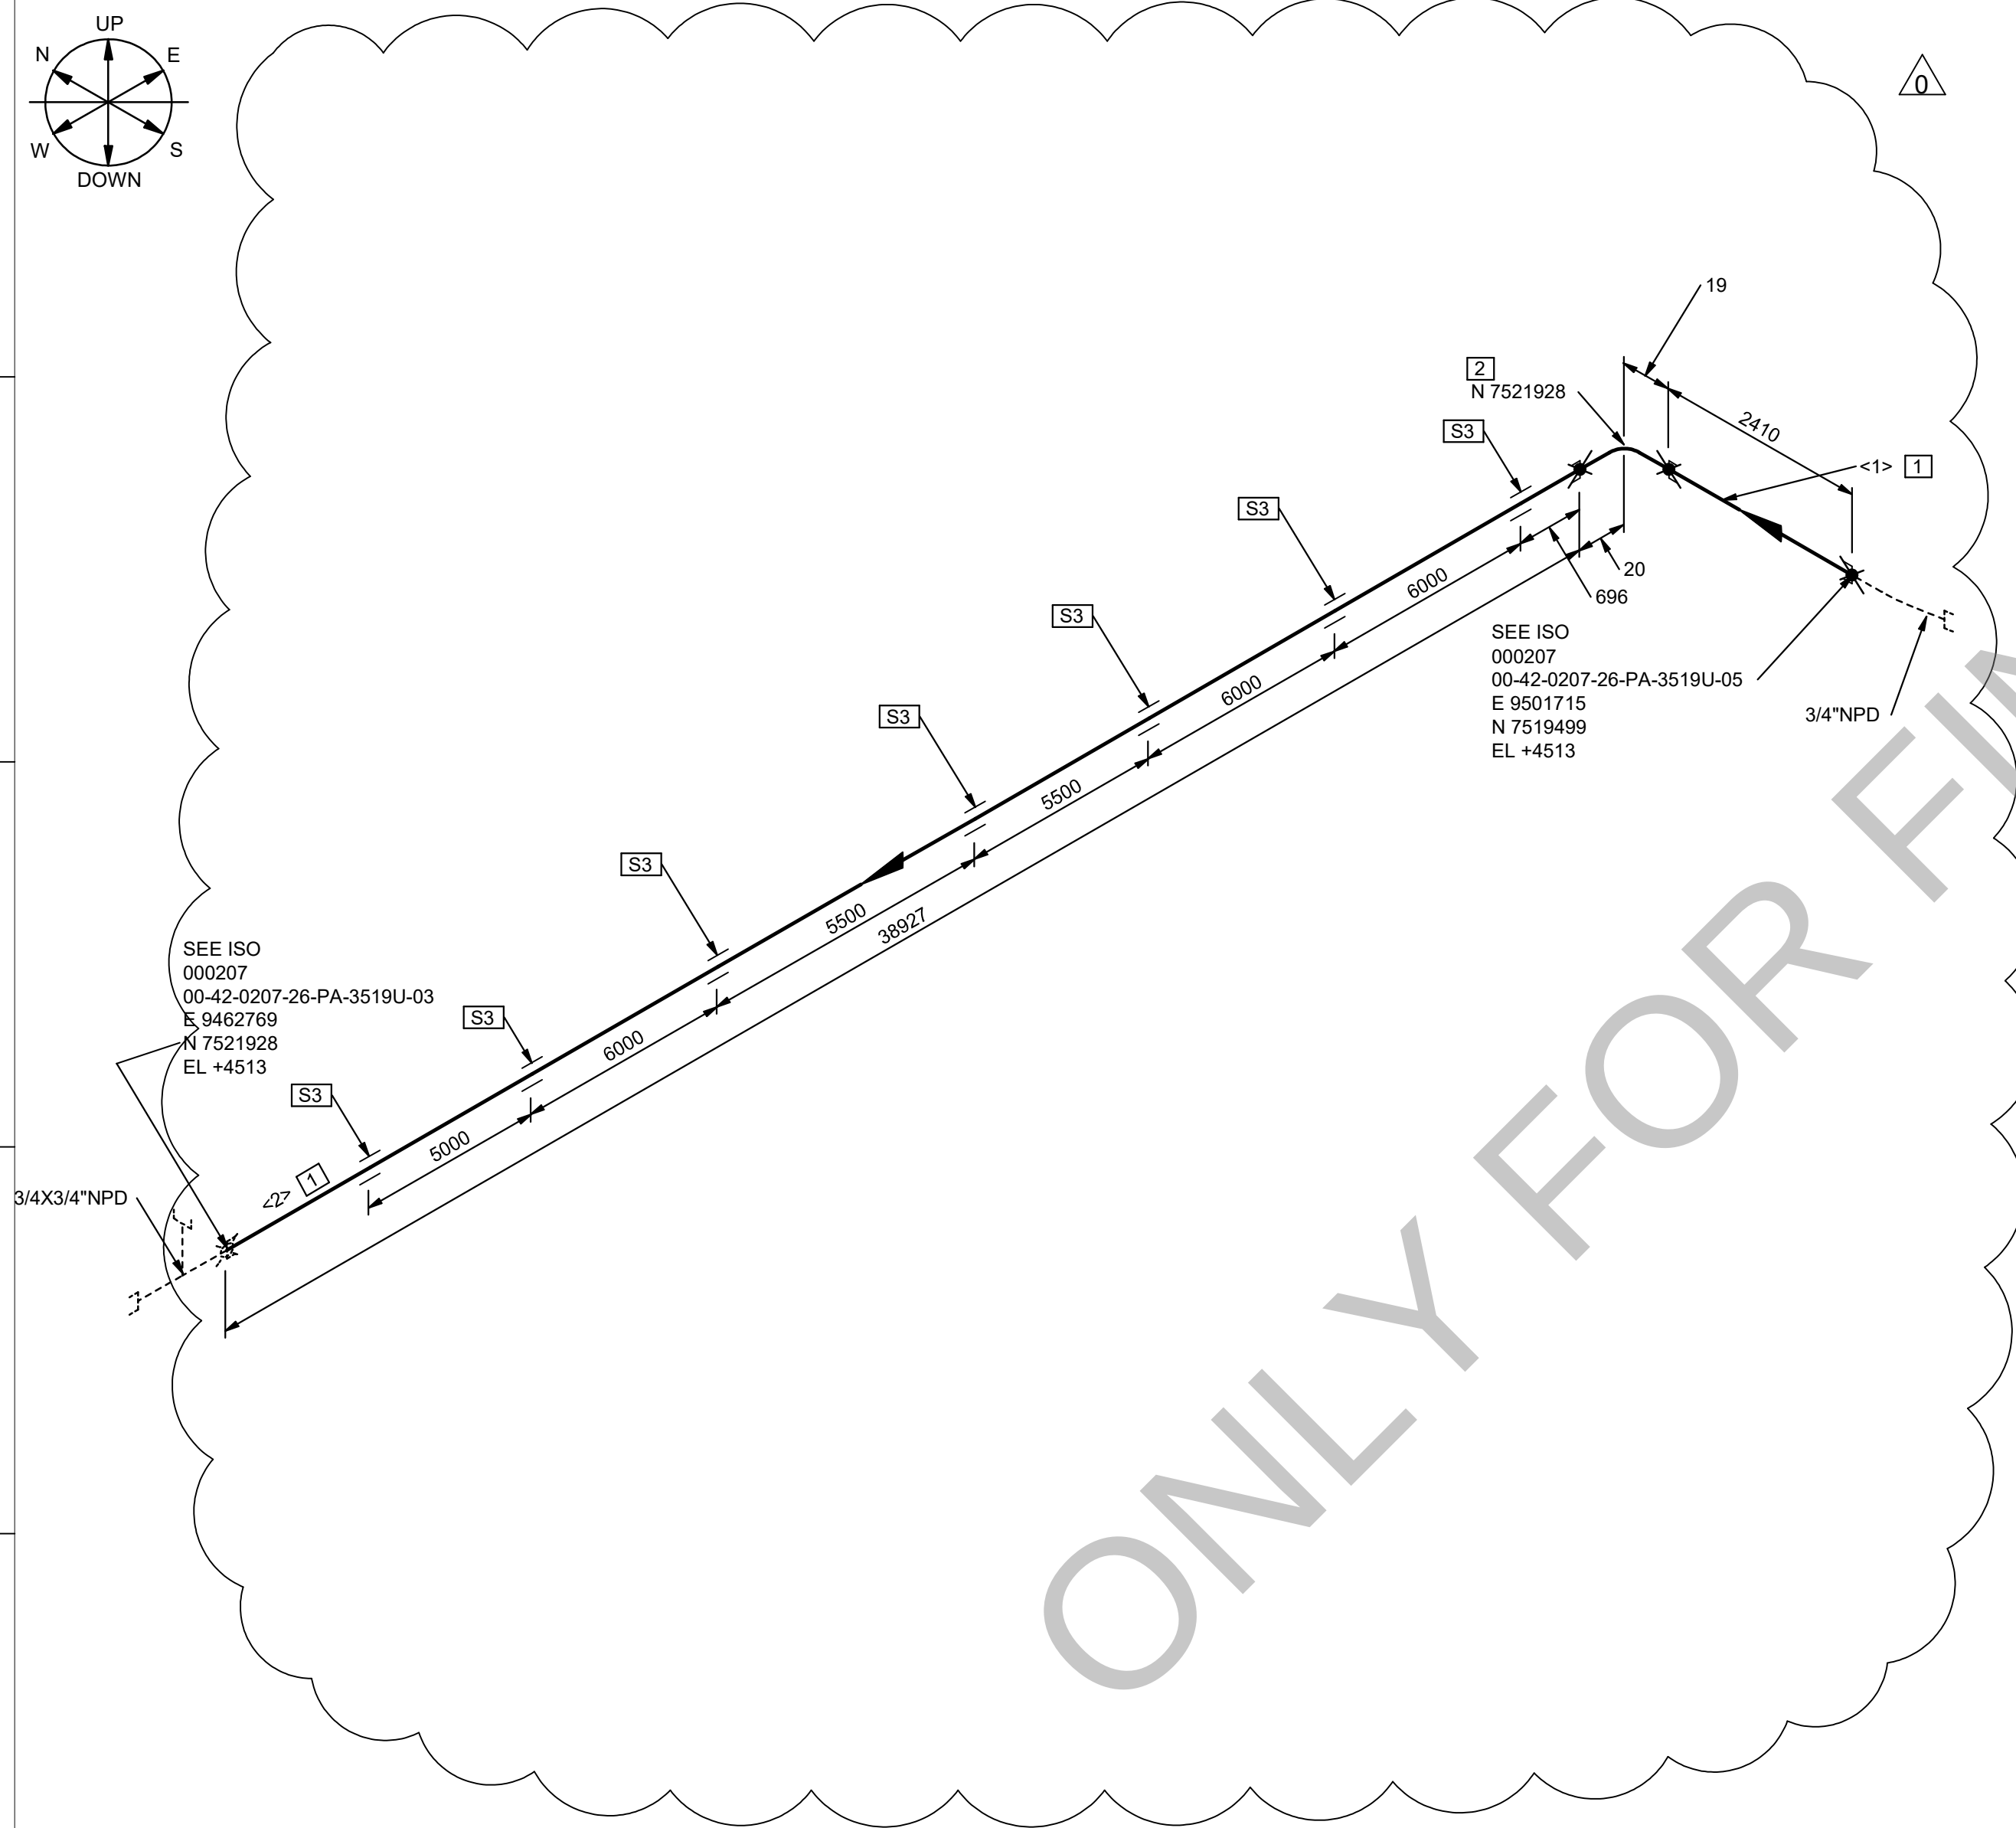

CUT PIPE LENGTH							
PIECE NO	LENGTH (MM)	NPD (IN)	REMARKS	PIECE NO	LENGTH (MM)	NPD (IN)	REMARKS
<1>	2410	3/4		<2>	38927	3/4	

CAA-1 PROJECT Cilegon, Banten, Indonesia									
 Chandra Asri					PT CHANDRA ASRI ALKALI				
Confidential					ISSUE FOR REVIEW				
 中国成达工程有限公司 CHINA CHENGDA ENGINEERING CO., LTD.		China Chengda Engineering Co.,Ltd							
Piping Isometric Drawing for 7 # Pipe rack									
Scale 1/1 @A3	Sheet 1 of 1	Project Doc Number :							
		CAA	CE	1	ED	00	PIP	ISO	E
Isometric drawing No:		00-42-0207-26-PA-3519U-04							
Contractor/Licensor Doc No:		0.75"-PA-3519U-1C2-04							



CUT PIPE LENGTH

SEE ISO
000207
00-42-0207-26-PA-3519U-06
E 9534216
N 7519480
EL +4413

E 9501715
EL +4513

Document Review Result

Approved by :
Date :

LEGEND

SHOP WELD	FIELD WELD	SOCKET WELD	SCREWED JOINT	PIPE SUPPORT	LAGGED PIPE	TRACED PIPE

 Chandra Asri

Confidential


ISSUE FOR REVIEW





China Chengda Engineering Co.,Ltd

Piping Isometric Drawing for 7 # Pipe rack

Scale 1/1 @A3	Sheet 1 of 1	Project Doc Number :									
		CAA	CE	1	ED	00	PIP	ISO	E	17001~17020	
Isometric drawing No:		00-42-0207-26-PA-3519U-05									
Contractor/Licensor Doc No:		0.75"-PA-3519U-1C2-05									

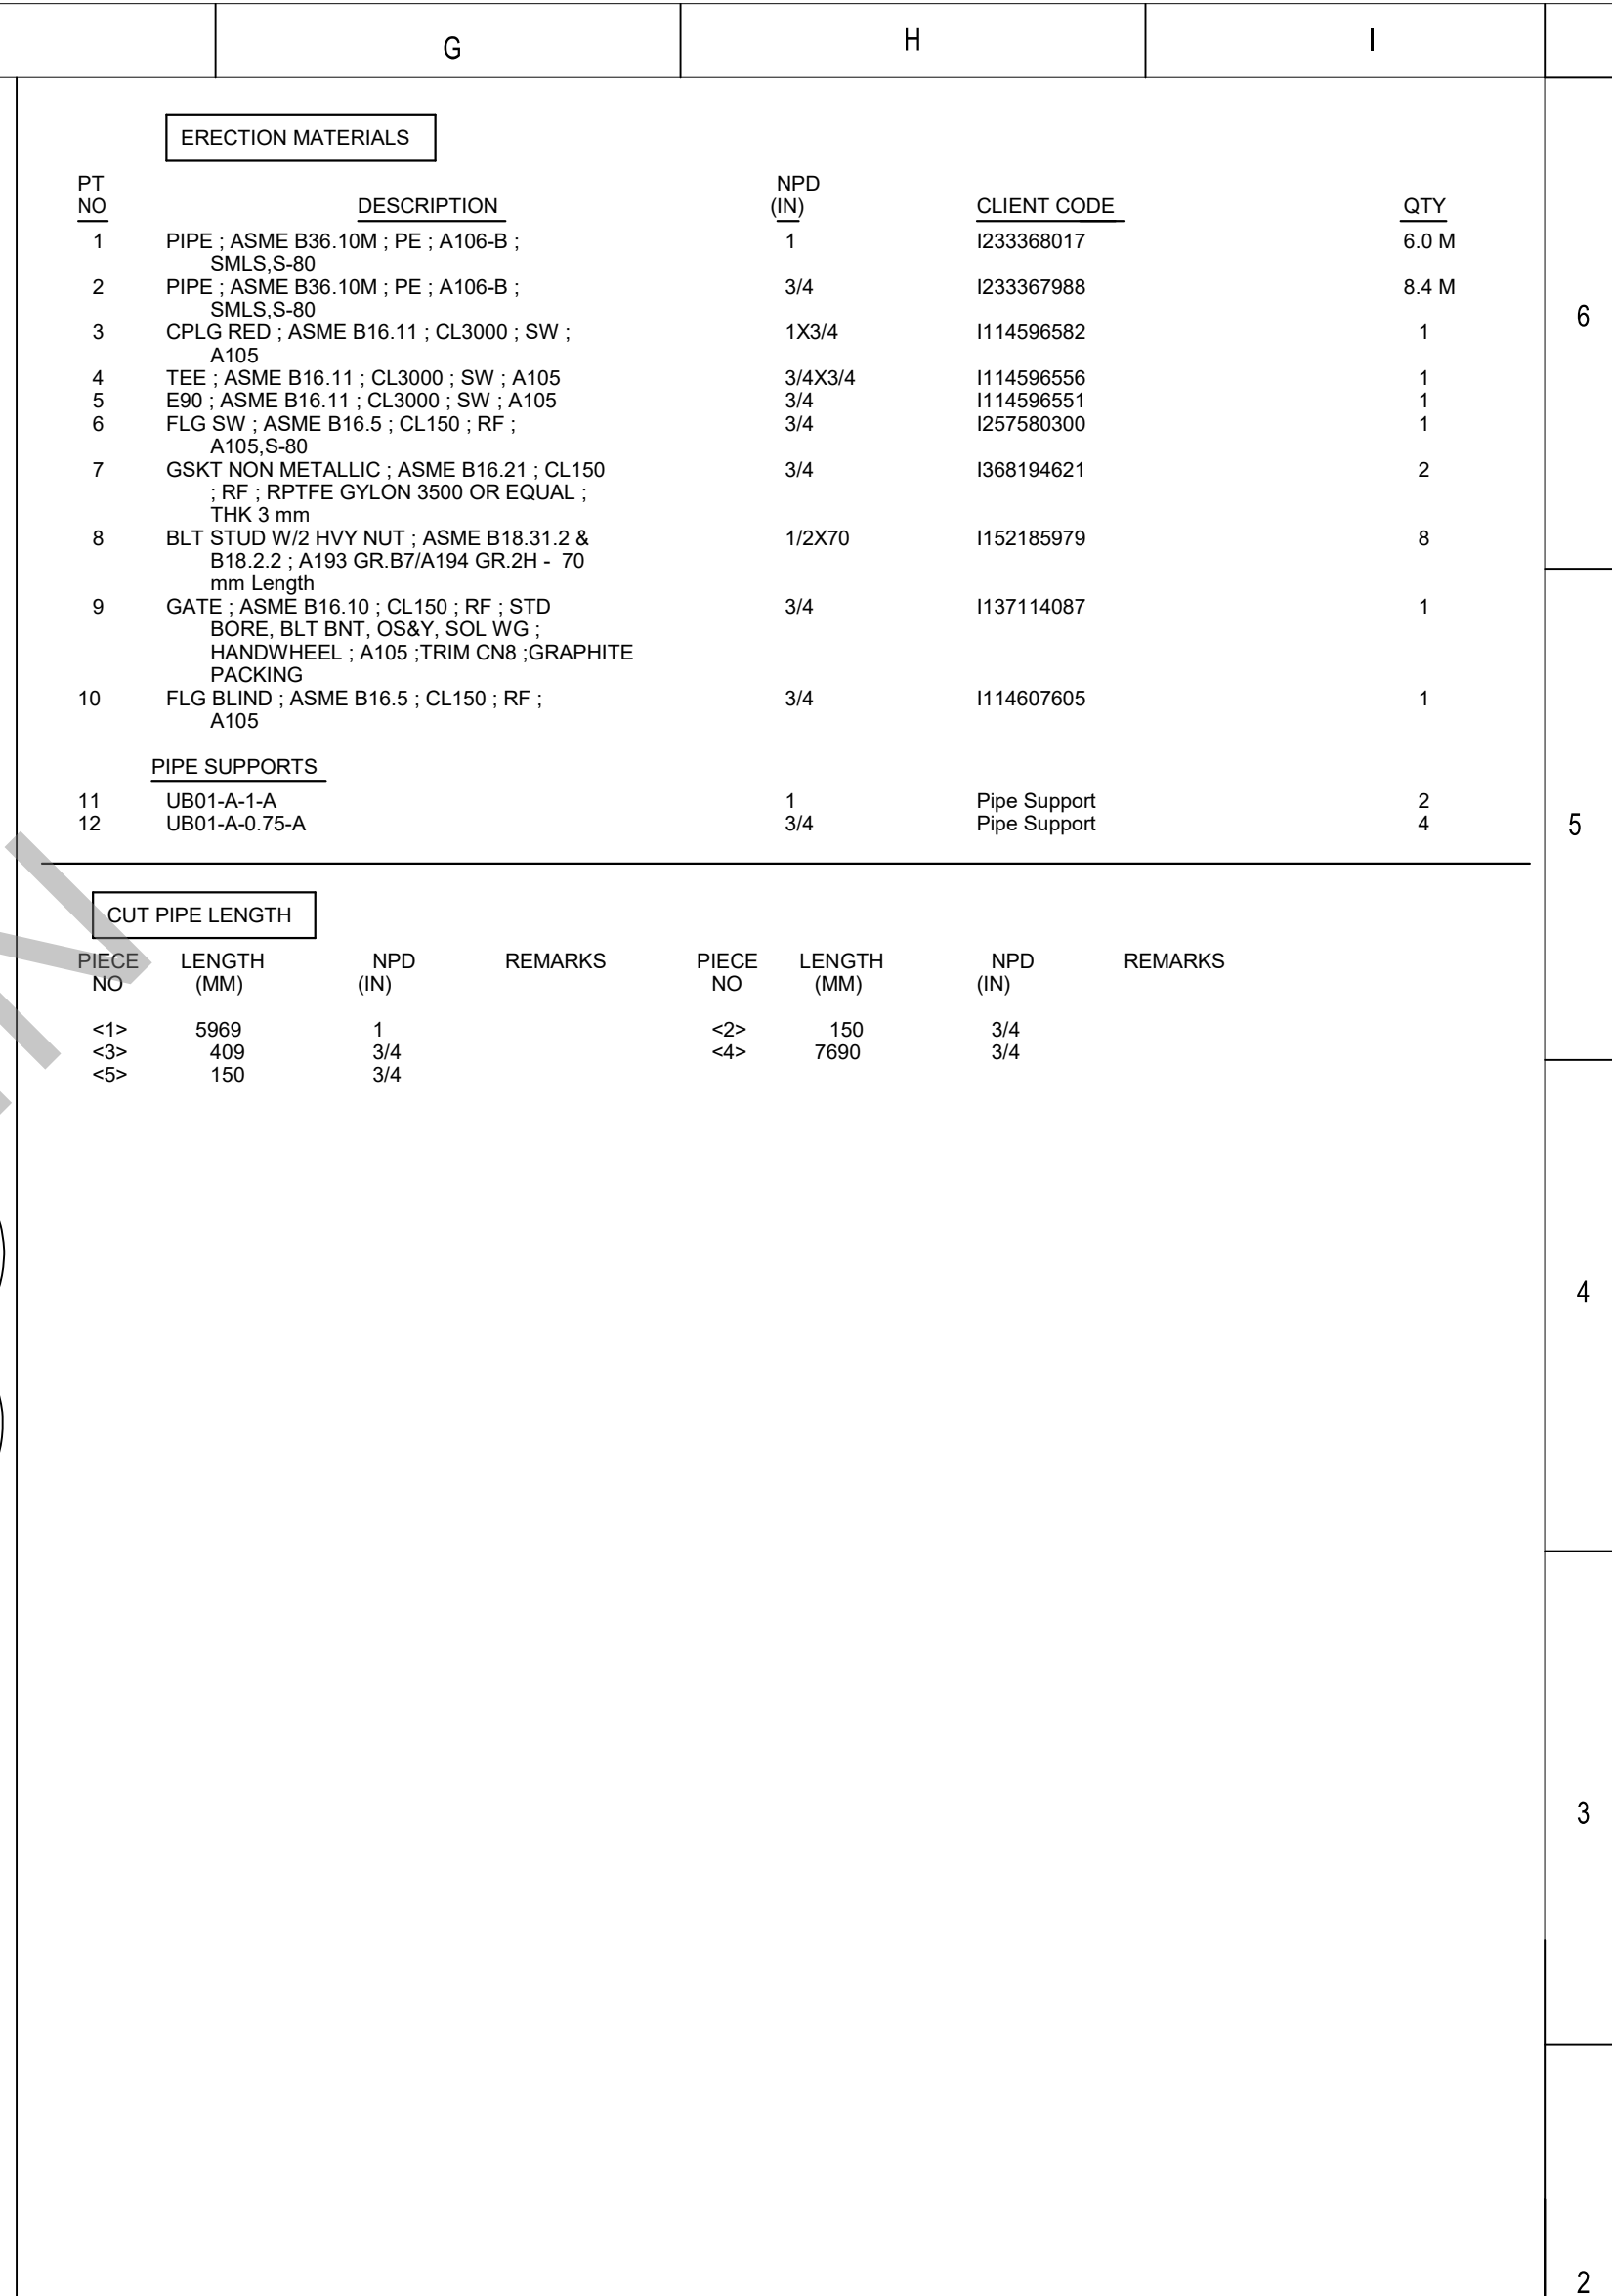

CAA-1 PROJECT Cilegon, Banten, Indonesia												
 Chandra Asri						PT CHANDRA ASRI ALKALI						
Confidential						ISSUE FOR REVIEW						
 中国成达工程有限公司 CHINA CHENGDA ENGINEERING CO., LTD.				China Chengda Engineering Co.,Ltd								
Piping Isometric Drawing for 7 # Pipe rack												
Scale 1/1 @A3		Sheet 1 of 1		Project Doc Number :								
				CAA	CE	1	ED	00	PIP	ISO	E	17001~17020
Isometric drawing No:				00-42-0207-26-PA-3519U-06								
Contractor/Licensors Doc No:				1"-PA-3519U-1C2-06								
			G				H				I	

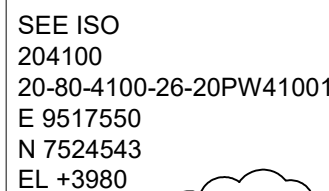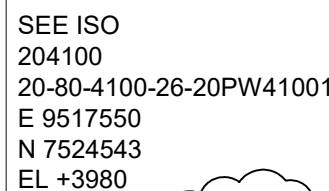

PT NO	DESCRIPTION	UNP (IN)	CLIENT CODE	QTY
1	PIPE ; ASME B36.10M ; BE ; A106-B ; SMLS ; GALV., S-40	2	I155790983	5.6 M
2	TEE RED ; ASME B16.9 ; BE ; A234-WPB-S ; GALV., S-40xS-80	2X3/4	I155794624	1
3	E90LR ; ASME B16.9 ; BE ; A234-WPB-S ; GALV., S-40	2	I155791817	2
4	NIPPLE ; ASME B36.10M ; PE x MTE ; A106-B ; L = 100 MM ; GALV., S-160	3/4	I429704506	1
5	FLG SO ; ASME B16.5 ; CL150 ; RF ; A105 ; GALV.	2	I177619870	1
6	FLG THD ; ASME B16.5 ; CL150 ; RF ; A105 ; GALV.	3/4	I472177256	1
7	GSKT NON METALLIC ; ASME B16.21 ; CL150 ; RF ; RPTFE GYLON 3500 OR EQUAL ; THK 3 mm	3/4	I368194621	2
8	BLT STUD W/2 HVY NUT ; ASME B18.31.2 & B18.2.2 ; A193 GR.B7/A194 GR.2H ; W/2 WASHER ; GALV. - 70 mm Length	1/2X70	I537948375	8
9	GATE ; ASME B16.10 ; CL150 ; RF ; STD BORE, BLT BNT, OS&Y, SOL W/G ; HANDWHEEL ; B62-UNS C83600 ; TRIM SAME AS BODY ; GRAPHITE PACKING	3/4	I560056231	1
10	FLG BLIND ; ASME B16.5 ; CL150 ; RF ; A105 ; GALV.	3/4	I115473122	1
PIPE SUPPORTS				
11	SC01-A-2-250	2	Pipe Support	2
12	FR04-B-250-200-100-A-1	2	Pipe Support	1
13	FR04-B-299-200-100-A-1	2	Pipe Support	1

CUT PIPE LENGTH						
PIECE NO	LENGTH (MM)	NPD (IN)	REMARKS	PIECE NO	LENGTH (MM)	NPD (IN)
<1>	566	2		<2>	398	2
<3>	4575	2				

 Chandra Asri

Confidential

 **中国成达工程有限公司**
CHINA CHENGDA ENGINEERING CO., LTD.

Piping Isometric Drawing for 7 # Pipe rack

Sheet
1 of 1

Contractor/Licensors Doc No

2"-PW-0003-106-HC-01

								Document Review Result			
0A	6/5/2026	ISSUE FOR CONSTRUCTION	XZS	PJ	ML			☐ Approved	☐ Reviewed with Comments		
0	23/3/2026	ISSUE FOR CONSTRUCTION	XZS	PJ	ML			☐ Approved with Comments			
A	17/12/2025	ISSUE FOR REVIEW	XZS	PJ	ML			☐ No Comment			
Rev	Date	Description	Designed	Checked	Approved	Authorized		☐ Rejected	☐ No Comment with Hold		
THE INFORMATION CONTAINED IN THIS DOCUMENT IS CONFIDENTIAL AND/OR RESTRICTED, PRIVILEGED, AND ONLY FOR THE SOLE USE OF THE INTENDED RECIPIENT AND INTENDED PURPOSE. ANY FORM OF REPRODUCTION, DISSEMINATION, COPYING, DISCLOSURE, MODIFICATION AND/OR PUBLICATION IS STRICTLY PROHIBITED WITHOUT PRIOR WRITTEN CONSENT FROM PT CHANDRA ASRI ALKALIAND/OR FROM THE RELEVANT OWNER OF SUCH INFORMATION.								Approved by :			
ISOMETRIC NOTE:								Date :			
								LEGEND			
DESIGN TEMP.	deg C	65	OPE. TEMP.	deg C	-1AMB/-	PWHT	0	NOT REQUIRED	P&ID NO.	20-PED-PID-E-10016	
DESIGN PRESS.	kg/cm ² g	6	OPE. PRESS.	kg/cm ² g	-2.5/-	PAINT SYSTEM		-	G&W. NO.	CAA-CE-1-ED-00-PIP-LAY-E-0207003	
PT	%	-	RT	%	2	TEST PRESS.	kg/cm ² g	a	WBS	000207	
INSULATION	CODE	HC	INSUL THICK.	mm	30	TEST MEDIA		WATER			

 SHOP WELD

 FIELD WELD


 SOCKET WELD

 SCREWED JOINT

 PIPE SUPPORT

 LAGGED PIPE

 TRACED PIPE

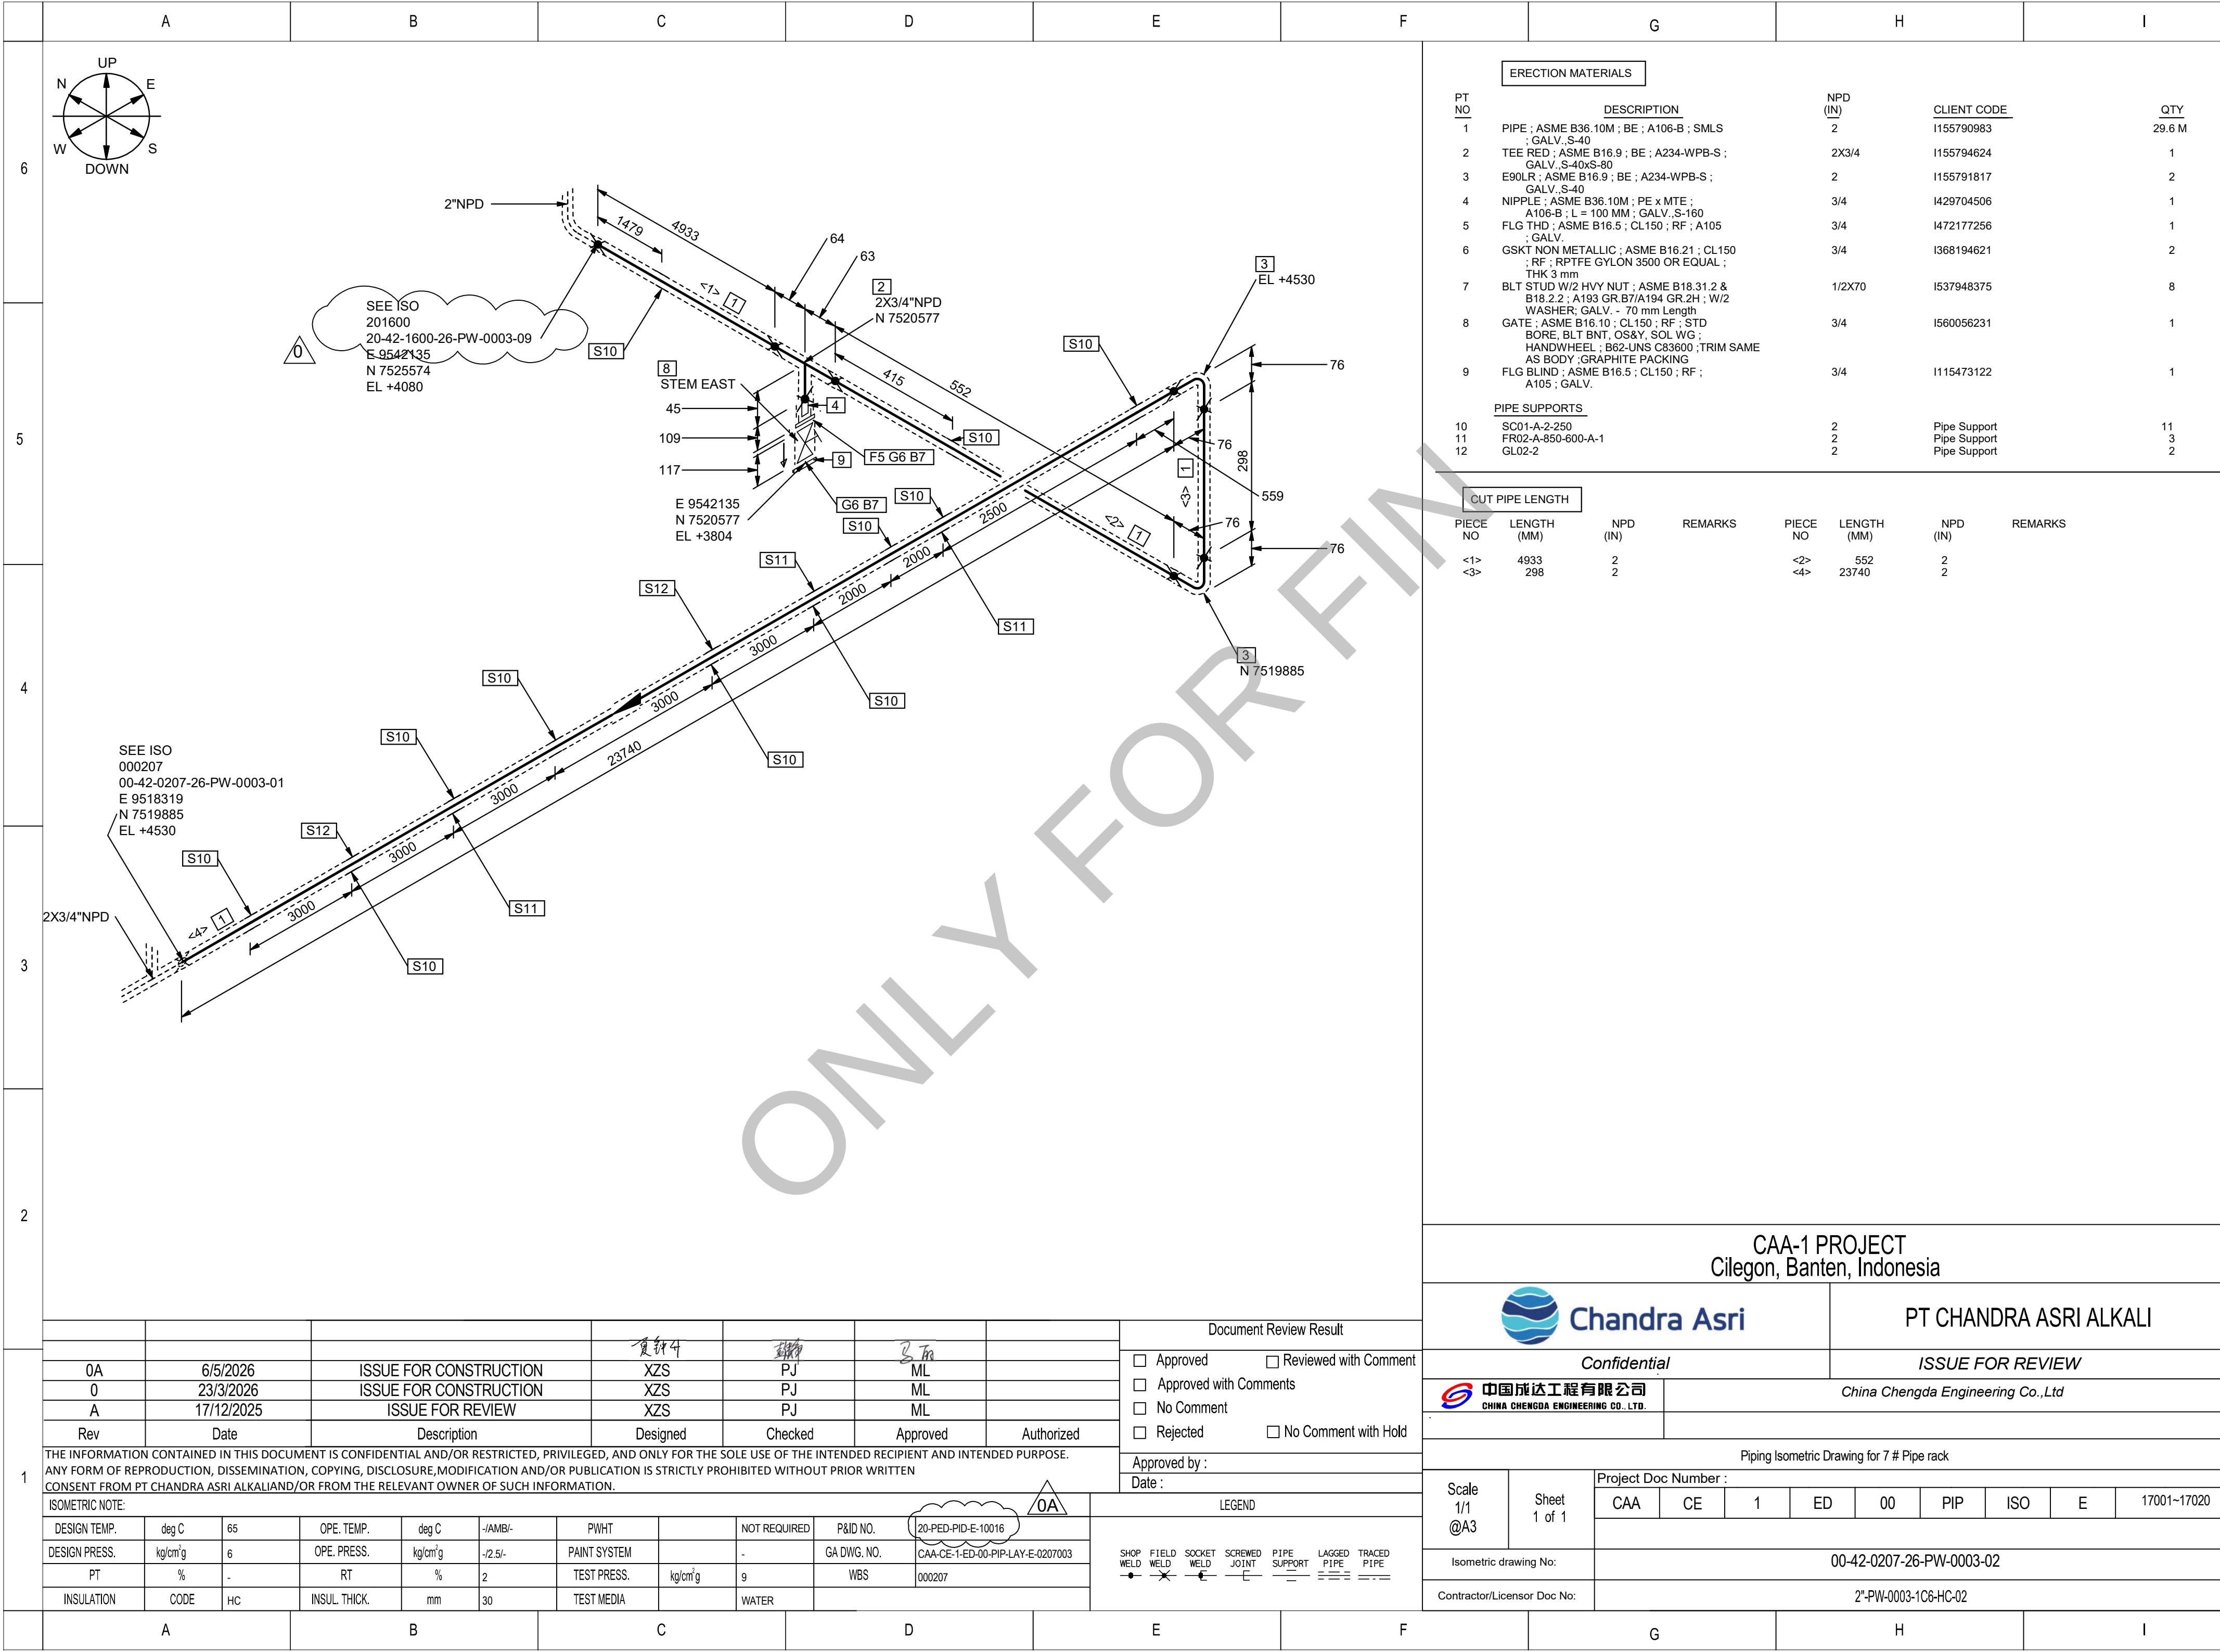

ERECTION MATERIALS				
PT NO	DESCRIPTION	NPD (IN)	CLIENT CODE	QTY
1	PIPE ; ASME B36.10M ; BE ; A106-B ; SMLS ; GALV., S-40	2	I155790983	29.6 M
2	TEE RED ; ASME B16.9 ; BE ; A234-WPB-S ; GALV., S-40xS-80	2X3/4	I155794624	1
3	E90LR ; ASME B16.9 ; BE ; A234-WPB-S ; GALV., S-40	2	I155791817	2
4	NIPPLE ; ASME B36.10M ; PE x MTE ; A106-B ; L = 100 MM ; GALV., S-160	3/4	I429704506	1
5	FLG THD ; ASME B16.5 ; CL150 ; RF ; A105 ; GALV.	3/4	I472177256	1
6	GSKT NON METALLIC ; ASME B16.21 ; CL150 ; RF ; RPTFE GYLON 3500 OR EQUAL ; THK 3 mm	3/4	I368194621	2
7	BLT STUD W/2 HVY NUT ; ASME B18.31.2 & B18.2.2 ; A193 GR.B7/A194 GR.2H ; W/2 WASHER ; GALV. - 70 mm Length	1/2X70	I537948375	8
8	GATE ; ASME B16.10 ; CL150 ; RF ; STD BORE, BLT BNT, OS&Y, SOL WG ; HANDWHEEL ; B62-UNS C83600 ; TRIM SAME AS BODY ; GRAPHITE PACKING	3/4	I560056231	1
9	FLG BLIND ; ASME B16.5 ; CL150 ; RF ; A105 ; GALV.	3/4	I115473122	1
PIPE SUPPORTS				
10	SC01-A-2-250	2	Pipe Support	11
11	FR02-A-850-600-A-1	2	Pipe Support	3
12	GL02-2	2	Pipe Support	2

CUT PIPE LENGTH							
PIECE NO	LENGTH (MM)	NPD (IN)	REMARKS	PIECE NO	LENGTH (MM)	NPD (IN)	REMARKS
<1>	4933	2		<2>	552	2	
<3>	298	2		<4>	23740	2	

Document Review Result						
☐ Approved ☐ Reviewed with Comment						
☐ Approved with Comments						
☐ No Comment						
☐ Rejected ☐ No Comment with Hold						
Approved by :						
Date :						
LEGEND						
SHOP WELD FIELD WELD SOCKET WELD SCREWED JOINT PIPE SUPPORT LAGGED PIPE TRACED PIPE						
THE INFORMATION CONTAINED IN THIS DOCUMENT IS CONFIDENTIAL AND/OR RESTRICTED, PRIVILEGED, AND ONLY FOR THE SOLE USE OF THE INTENDED RECIPIENT AND INTENDED PURPOSE. ANY FORM OF REPRODUCTION, DISSEMINATION, COPYING, DISCLOSURE, MODIFICATION AND/OR PUBLICATION IS STRICTLY PROHIBITED WITHOUT PRIOR WRITTEN CONSENT FROM PT CHANDRA ASRI ALKALI AND/OR FROM THE RELEVANT OWNER OF SUCH INFORMATION.						
ISOMETRIC NOTE:						
DESIGN TEMP.	deg C	65	OPE. TEMP.	deg C	-/AMB/-	PWHT
DESIGN PRESS.	kg/cm ² g	6	OPE. PRESS.	kg/cm ² g	-/2.5/-	PAINT SYSTEM
PT	%	-	RT	%	2	TEST PRESS.
INSULATION	CODE	HC	INSUL THICK.	mm	30	TEST MEDIA

CAA-1 PROJECT
Cilegon, Banten, Indonesia

PT CHANDRA ASRI ALKALI

ConfidentialISSUE FOR REVIEW


China Chengda Engineering Co., Ltd

Piping Isometric Drawing for 7 # Pipe rack

Scale 1/1 @A3Sheet 1 of 1Project Doc Number : CAA CE 1 ED 00 PIP ISO E 17001-17020

Isometric drawing No: 00-42-0207-26-PW-0003-02

Contractor/Licensors Doc No: 2"-PW-0003-1C6-HC-02

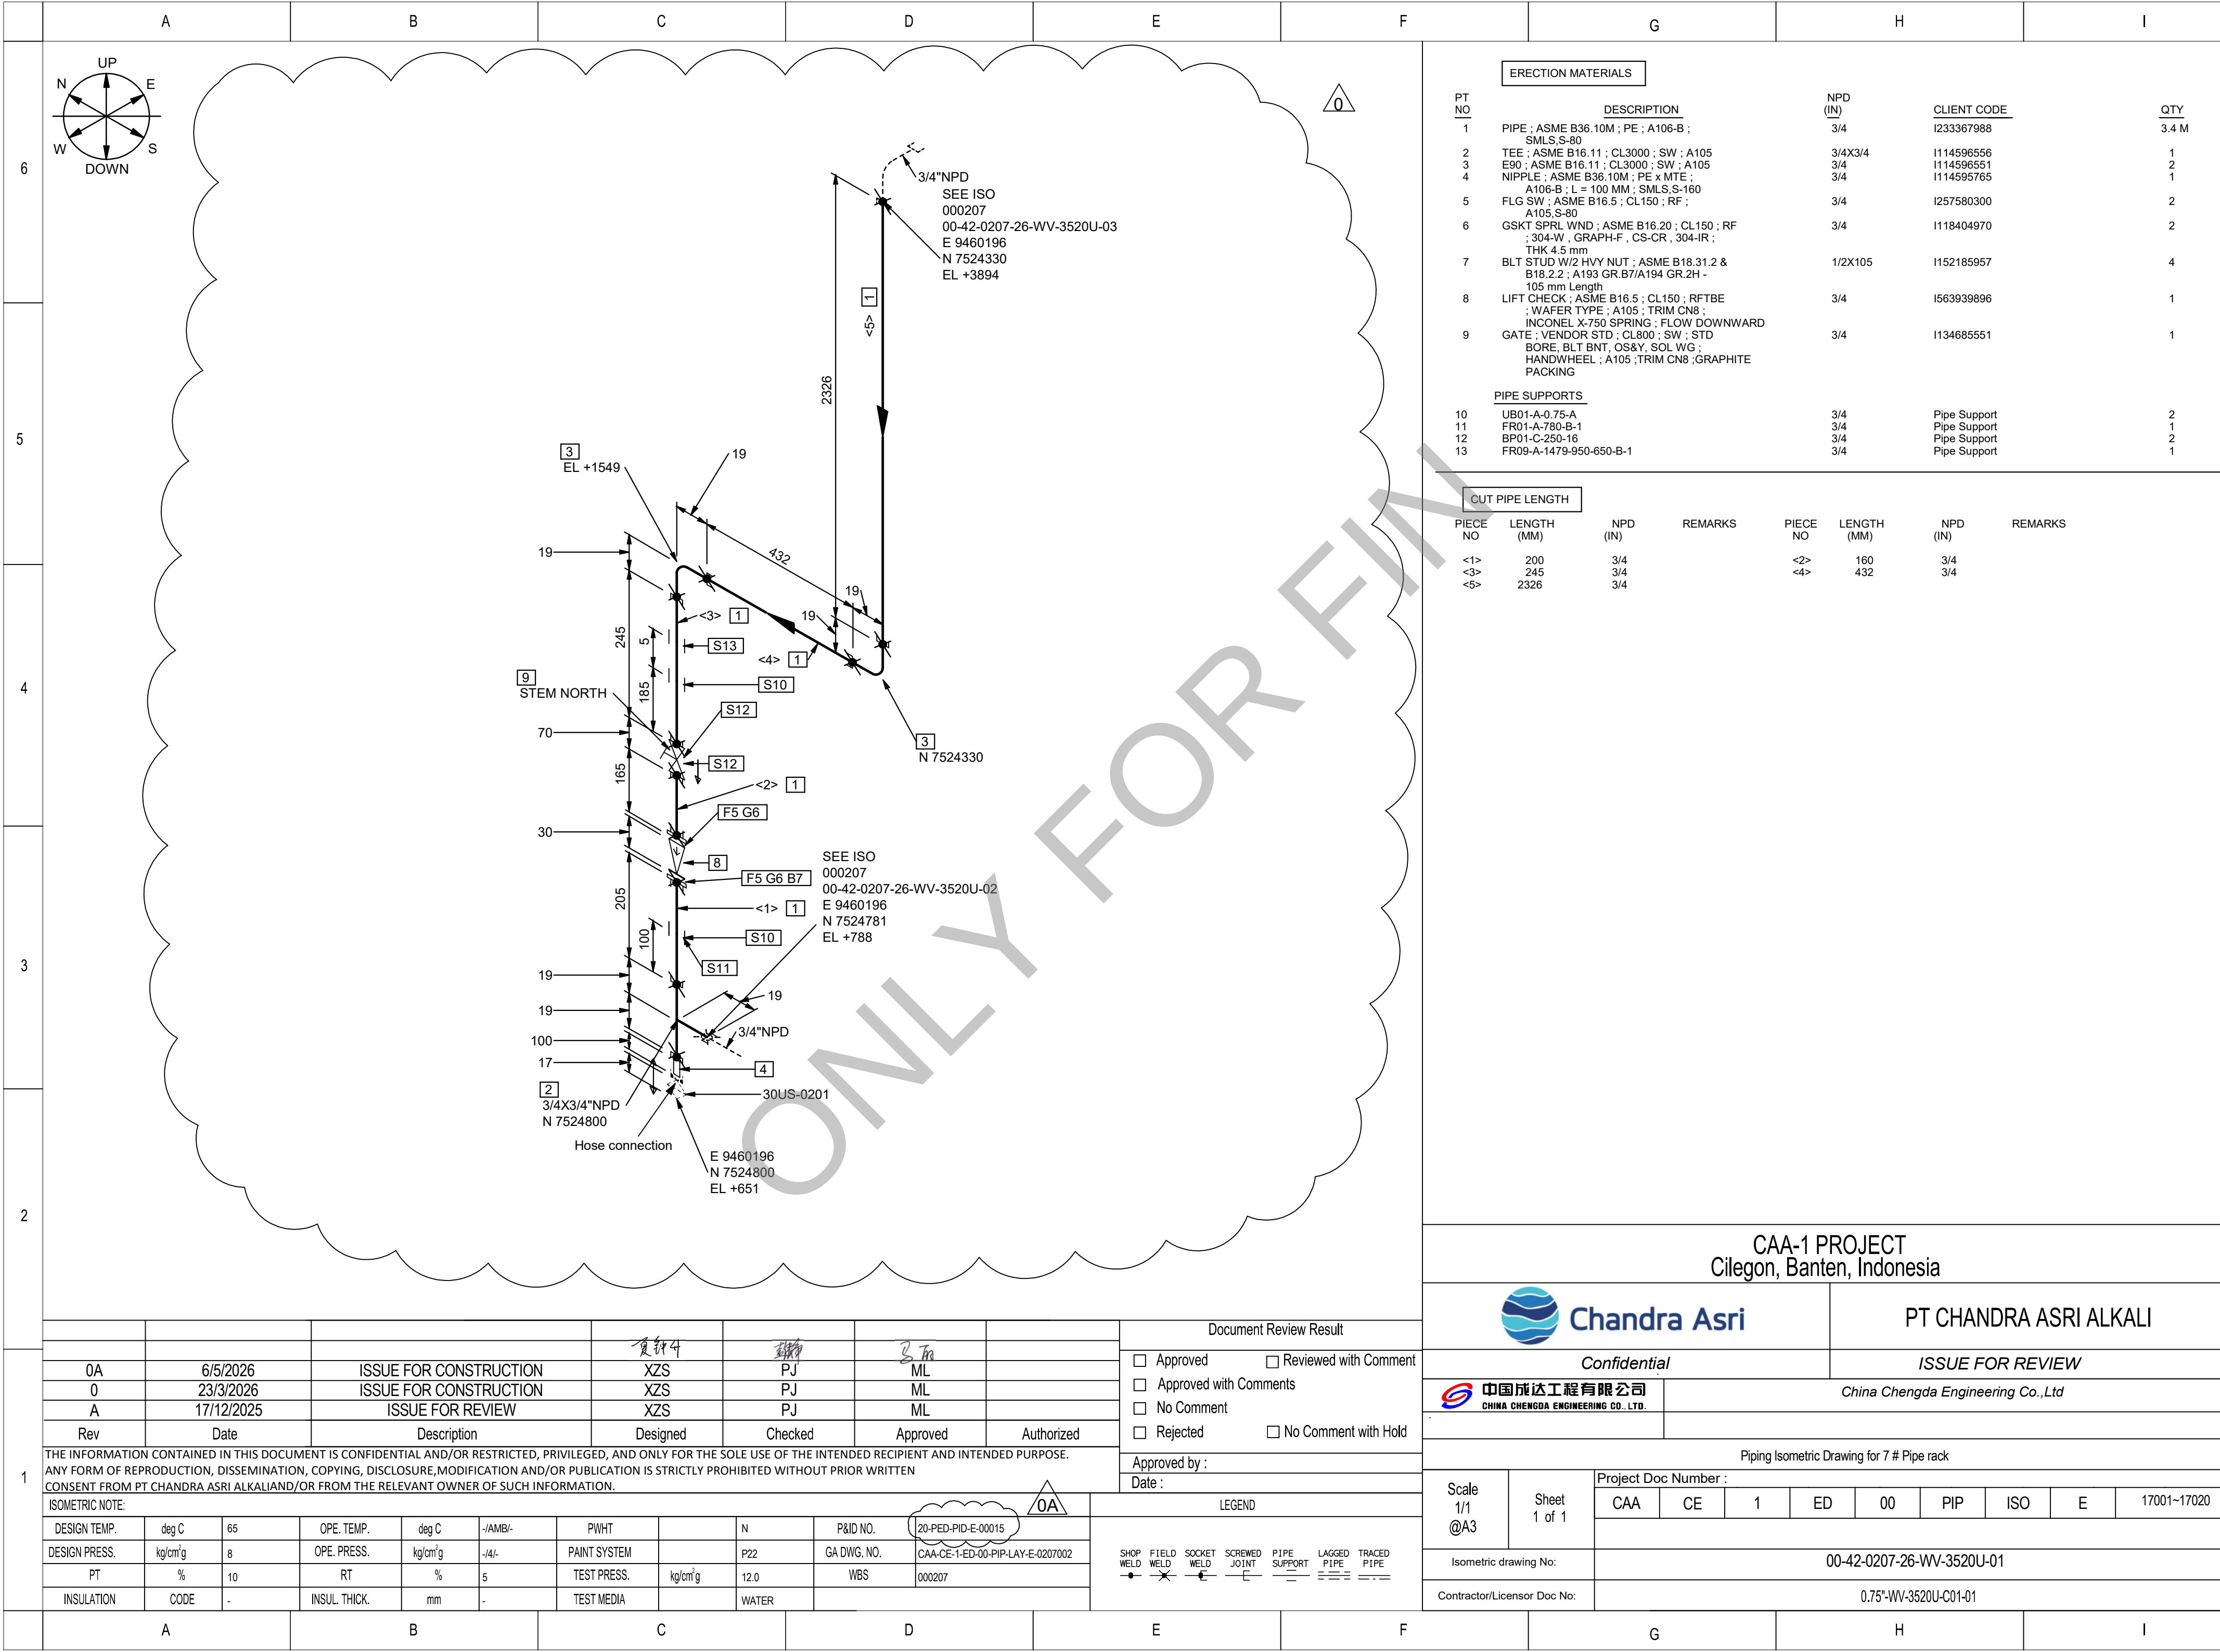

ERECTION MATERIALS				
PT NO	DESCRIPTION	NPD (IN)	CLIENT CODE	QTY
1	PIPE ; ASME B36.10M ; PE ; A106-B ; SMLS,S-80	3/4	I233367988	3.4 M
2	TEE ; ASME B16.11 ; CL3000 ; SW ; A105	3/4X3/4	I114596556	1
3	E90 ; ASME B16.11 ; CL3000 ; SW ; A105	3/4	I114596551	2
4	NIPPLE ; ASME B36.10M ; PE x MTE ; A106-B ; L = 100 MM ; SMLS,S-160	3/4	I114595765	1
5	FLG SW ; ASME B16.5 ; CL150 ; RF ; A105,S-80	3/4	I257580300	2
6	GSKT SPRL WND ; ASME B16.20 ; CL150 ; RF ; 304-W , GRAPH-F , CS-CR , 304-IR ; THK 4.5 mm	3/4	I118404970	2
7	BLT STUD W/2 HVY NUT ; ASME B18.31.2 & B18.2.2 ; A193 GR.B7/A194 GR.2H - 105 mm Length	1/2X105	I152185957	4
8	LIFT CHECK ; ASME B16.5 ; CL150 ; RFTBE ; WAFER TYPE ; A105 ; TRIM CN8 ; INCONEL X-750 SPRING ; FLOW DOWNWARD	3/4	I563939896	1
9	GATE ; VENDOR STD ; CL800 ; SW ; STD BORE, BLT BNT, OS&Y, SOL WG ; HANDWHEEL ; A105 ;TRIM CN8 ;GRAPHITE PACKING	3/4	I134685551	1
PIPE SUPPORTS				
10	UB01-A-0.75-A	3/4	Pipe Support	2
11	FR01-A-780-B-1	3/4	Pipe Support	1
12	BP01-C-250-16	3/4	Pipe Support	2
13	FR09-A-1479-950-650-B-1	3/4	Pipe Support	1

CUT PIPE LENGTH							
PIECE NO	LENGTH (MM)	NPD (IN)	REMARKS	PIECE NO	LENGTH (MM)	NPD (IN)	REMARKS
<1>	200	3/4		<2>	160	3/4	
<3>	245	3/4		<4>	432	3/4	
<5>	2326	3/4					

CAA-1 PROJECT
Cilegon, Banten, Indonesia

Chandra Asri

PT CHANDRA ASRI ALKALI

Confidential

ISSUE FOR REVIEW

中国成达工程有限公司
CHINA CHENGDA ENGINEERING CO., LTD.

China Chengda Engineering Co.,Ltd

Piping Isometric Drawing for 7 # Pipe rack

Scale
1/1
@A3

Sheet
1 of 1

Project Doc Number :
CAA CE 1 ED 00 PIP ISO E 17001-17020


Isometric drawing No:


00-42-0207-26-WV-3520U-01

Contractor/Licensor Doc No:

0.75"-WV-3520U-C01-01

Document Review Result						
☐ Approved	☐ Reviewed with Comment					
☐ Approved with Comments						
☐ No Comment						
☐ Rejected	☐ No Comment with Hold					
Approved by : Date :						
LEGEND						
SHOP WELD	FIELD WELD	SOCKET WELD	SCREWED JOINT	PIPE SUPPORT	LAGGED PIPE	TRACED PIPE
DESIGN TEMP.	deg C	65	OPE. TEMP.	deg C	-/AMB/-	PWHT
DESIGN PRESS.	kg/cm ² g	8	OPE. PRESS.	kg/cm ² g	-/4/-	PAINT SYSTEM
PT	%	10	RT	%	5	TEST PRESS.
INSULATION	CODE	-	INSUL THICK.	mm	-	TEST MEDIA

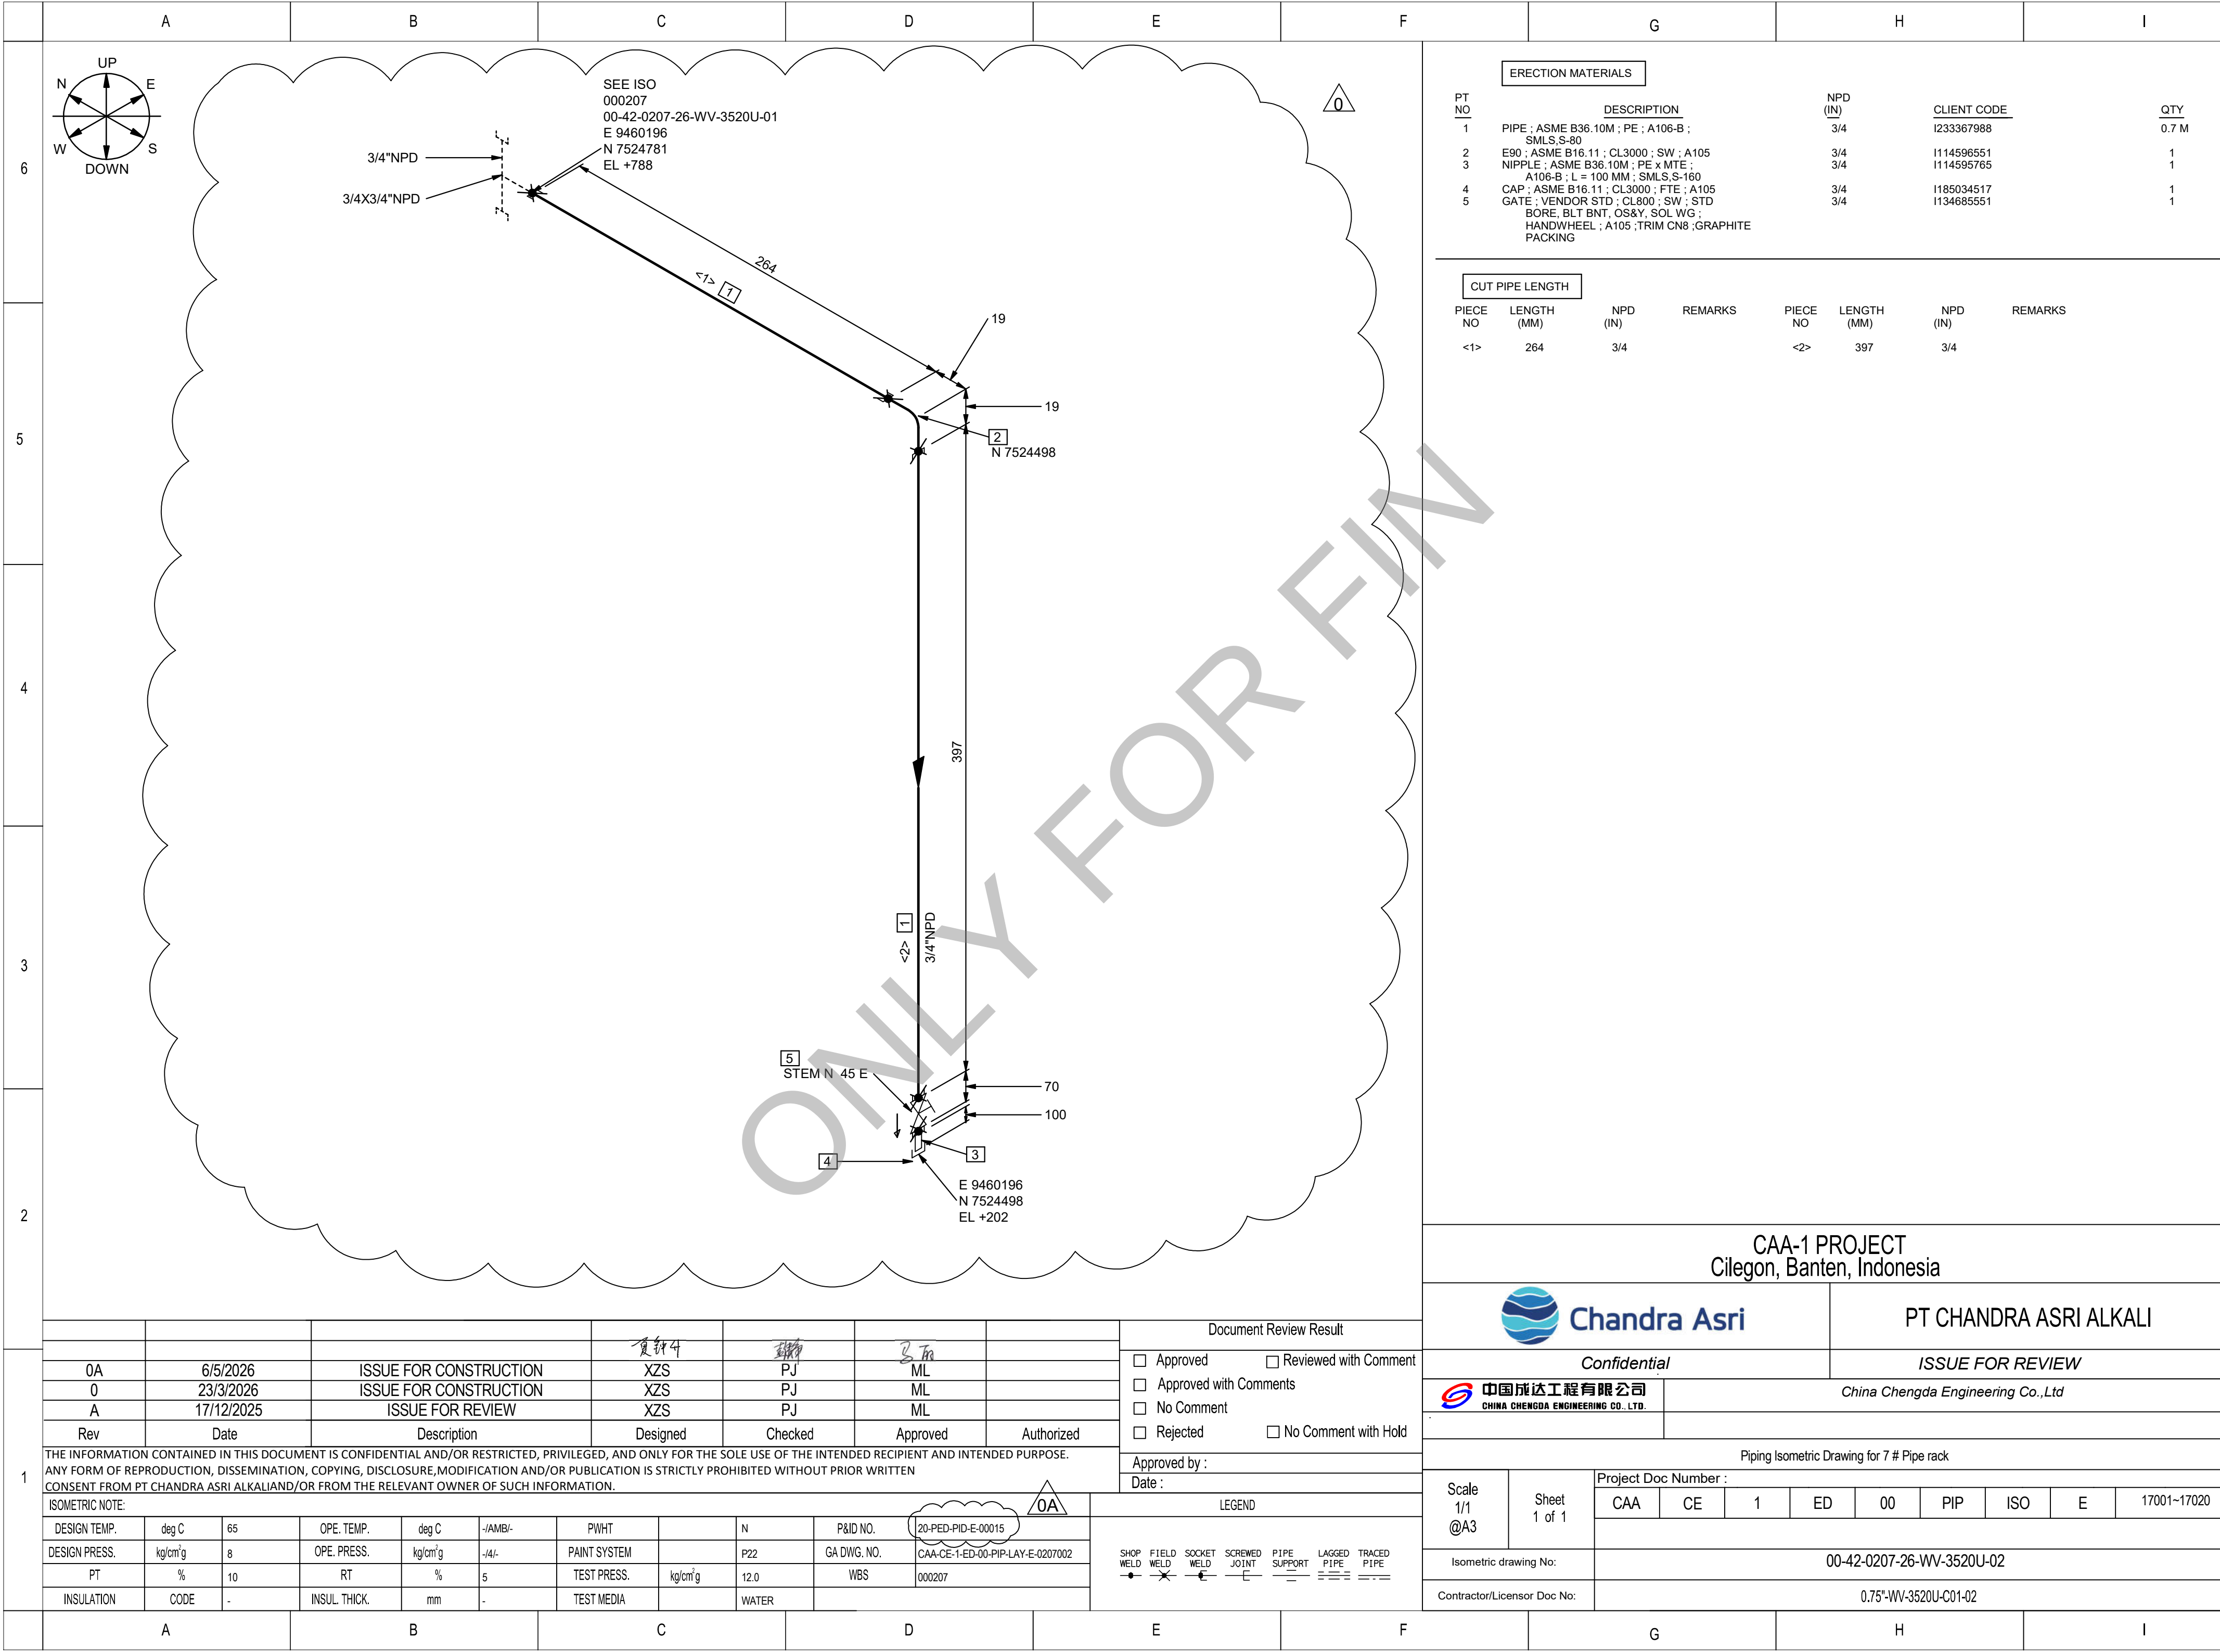

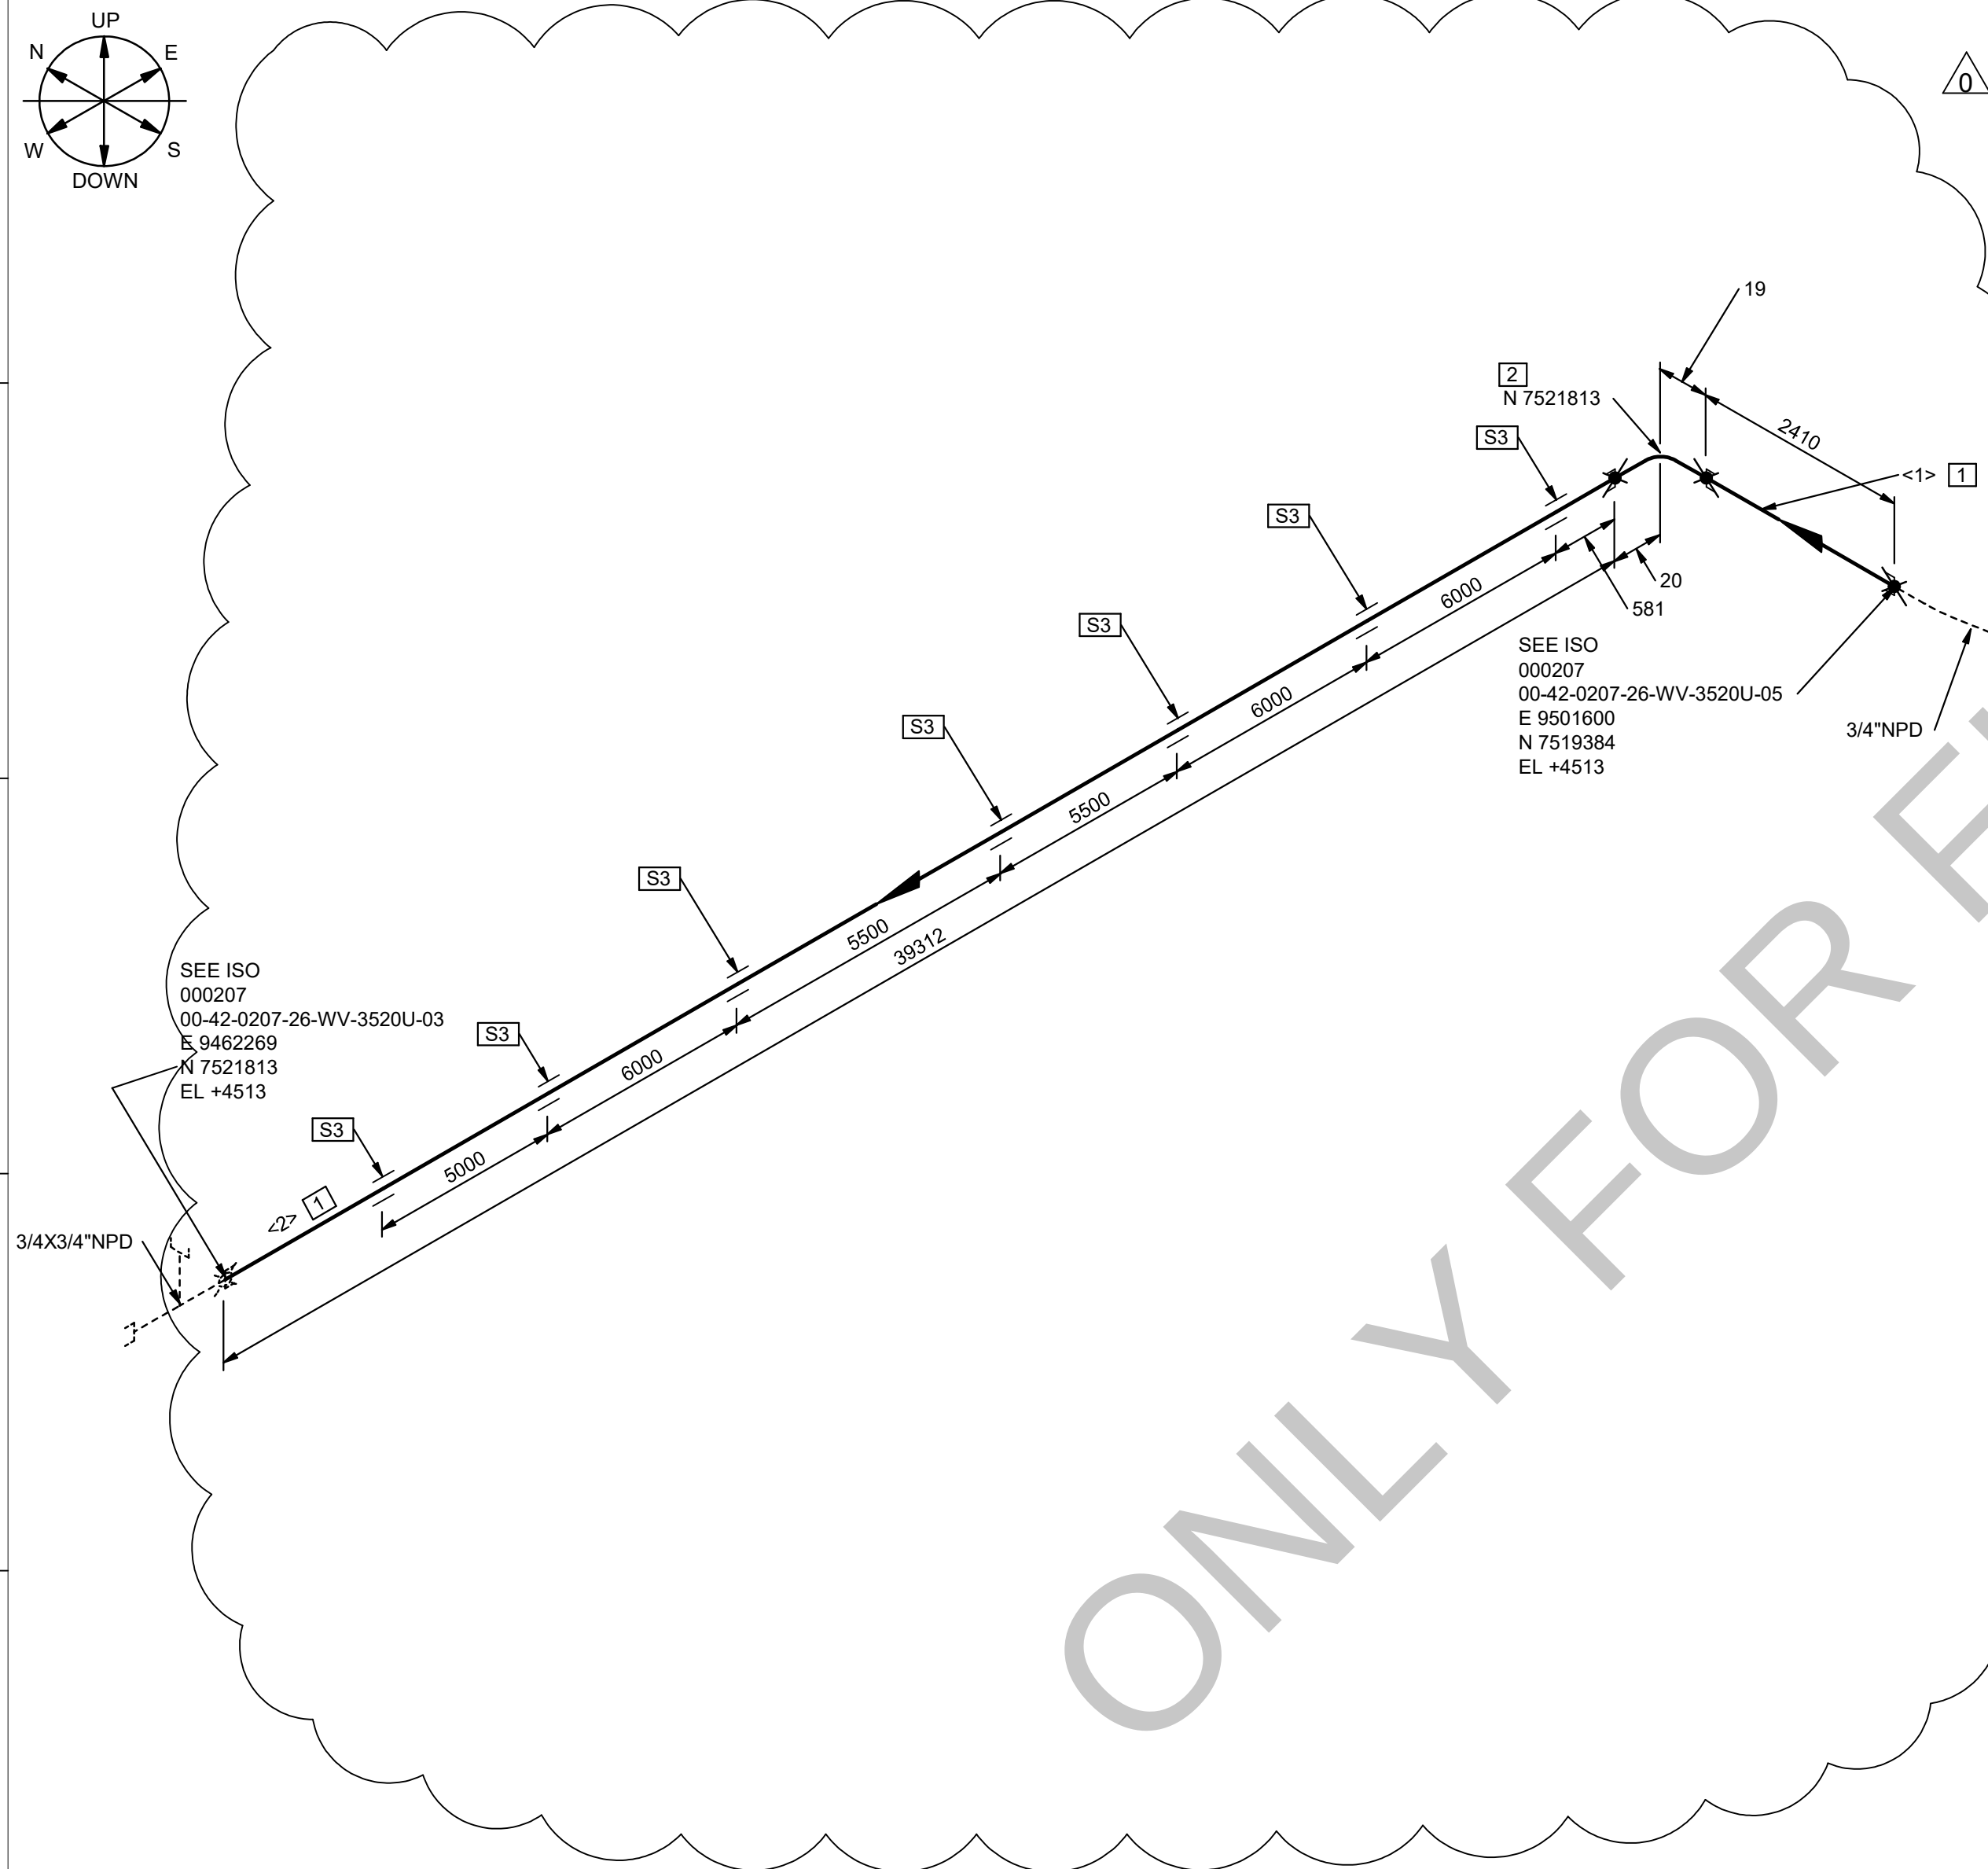

CUT PIPE LENGTH							
PIECE NO	LENGTH (MM)	NPD (IN)	REMARKS	PIECE NO	LENGTH (MM)	NPD (IN)	REMARKS
<1>	2410	3/4		<2>	39312	3/4	

CAA-1 PROJECT Cilegon, Banten, Indonesia										
 Chandra Asri					PT CHANDRA ASRI ALKALI					
Confidential					ISSUE FOR REVIEW					
 中国成达工程有限公司 CHINA CHENGDA ENGINEERING CO., LTD.			China Chengda Engineering Co.,Ltd							
Piping Isometric Drawing for 7 # Pipe rack										
Scale 1/1 @A3	Sheet 1 of 1	Project Doc Number :								
		CAA	CE	1	ED	00	PIP	ISO	E	17001~1
Isometric drawing No:		00-42-0207-26-WV-3520U-04								
Contractor/Licensor Doc No:		0.75"-WV-3520U-C01-04								

