
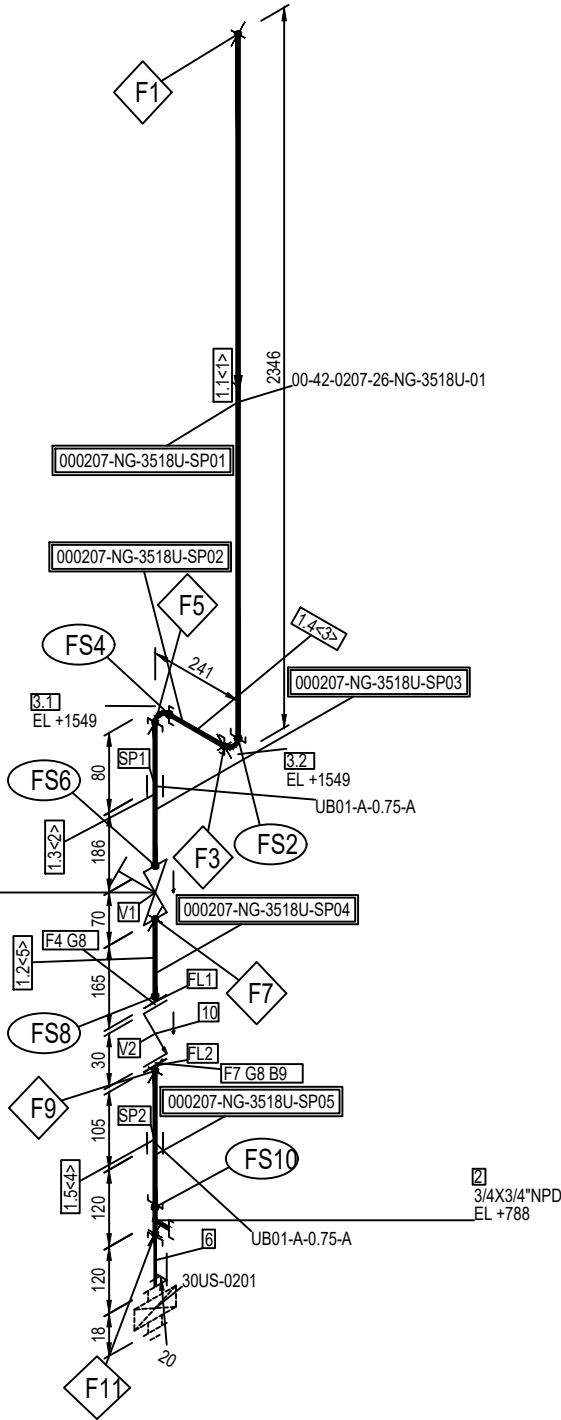


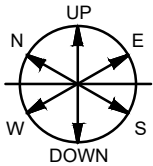

FABRICATION MATERIALS				
PT				NPD
NO	DESCRIPTION			(IN)
1	PIPE ; ASME B36.10M ; PE ; A106-B ; SMLS,S-80			3/4
2	TEE ; ASME B16.11 ; CL3000 ; SW ; A105			3/4X3/4
3	E90 ; ASME B16.11 ; CL3000 ; SW ; A105			3/4
4	FLG SW ; ASME B16.5 ; CL 150 ; RF ; A105,S-80			3/4
5	GATE ; VENDOR STD ; CL800 ; SW ; STD BORE, BLT BNT, OS&Y, SOL WG ; HANDWHEEL ; A105 ; TRIM CN8 ; GRAPHITE PACKING			3/4

ERECTION MATERIALS				
PT				NPD
NO	DESCRIPTION			(IN)
6	NIPPLE ; ASME B36.10M ; PE x MTE ; A106-B ; L = 100 MM ; SMLS,S-160			3/4
7	FLG SW ; ASME B16.5 ; CL 150 ; RF ; A105,S-80			3/4
8	GSKT SPRL WND ; ASME B16.20 ; CL 150 ; RF ; 304-W , GRAPH-F , CS-CR , 304-IR ; THK 4.5 mm			3/4
9	BLT STUD W/2 HVY NUT ; ASME B18.31.2 & B18.2.2 ; A193 GR.B7/A194 GR.2H - 105 mm Length			X105
10	LIFT CHECK ; ASME B16.5 ; CL 150 ; RFTBE ; WAFER TYPE ; A105 ; TRIM CN8 ; INCONEL X-750 SPRING ; FLOW DOWNWARD			3/4

PIPE SUPPORTS			
11	UB01-A-0.75-A	3/4	Pipe Support

WELD LIST					CUT PIPE LENGTH					
Joint No	Size	F/S	Weld Type	Material	No	Size	Length	No	Size	Length
F1	3/4"	FIELD	BW	1.1-*	1	3/4"	2326	2	3/4"	245
FS2	3/4"	SHOP	SW	3.2-1.1	3	3/4"	202	4	3/4"	200
F3	3/4"	FIELD	SW	1.4-3.2	5	3/4"	160			
FS4	3/4"	SHOP	SW	3.1-1.4						
F5	3/4"	FIELD	SW	1.3-3.1						
FS6	3/4"	SHOP	BW	5-1.3						
F7	3/4"	FIELD	BW	1.2-5						
FS8	3/4"	SHOP	SW	4-1.2						
F9	3/4"	FIELD	SW	1.5-7						
FS10	3/4"	SHOP	SW	2-1.5						
F11	3/4"	FIELD	SW	6-2						

SPOOL NUMBERS			
000207-NG-3518U-SP01	000207-NG-3518U-SP02		
000207-NG-3518U-SP03	000207-NG-3518U-SP04		
000207-NG-3518U-SP05			

CAA-1 PROJECT
Cilegon, Banten, Indonesia



Chandra Asri

PT CHANDRA ASRI ALKALI

Confidential

ISSUE FOR REVIEW



China Chengda Engineering Co.,Ltd

Scale
1/1
@A3

Sheet
1 of 1

Project Doc Number :

Isometric drawing No:
Contractor/Licensor Doc No:

00-42-0207-26-NG-3518U-01

0.75"-NG-3518U-C01-01

Document Review Result

- ☐ Approved
- ☐ Reviewed with Comment
- ☐ Approved with Comments
- ☐ No Comment
- ☐ Rejected
- ☐ No Comment with Hold

Approved by :

Date :

LEGEND

