
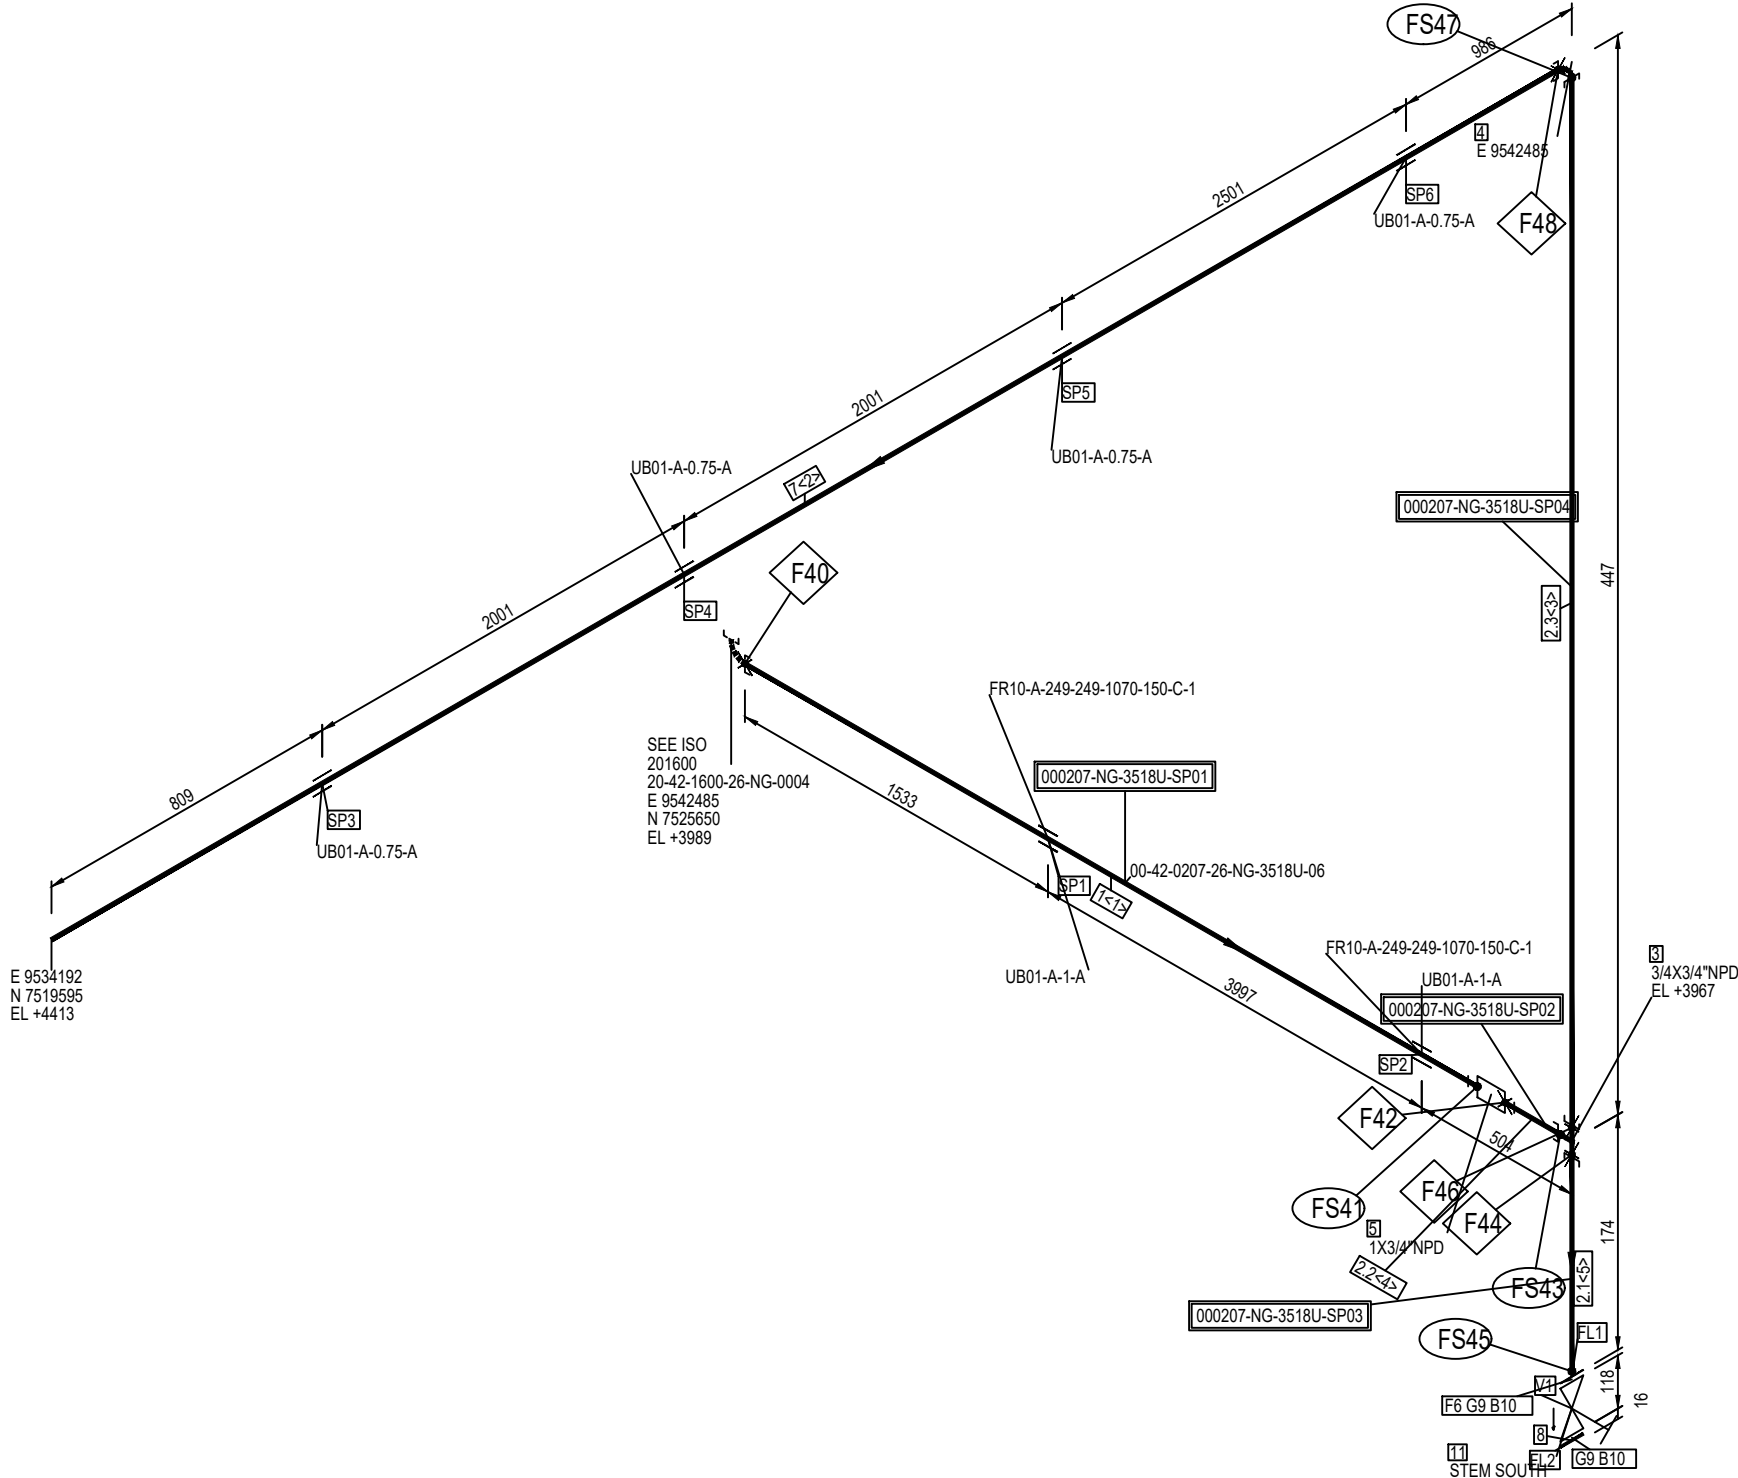


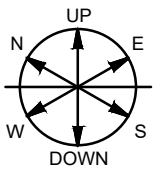

FABRICATION MATERIALS				
PT NO	DESCRIPTION	NPD (IN)	CLIENT CODE	QTY
1	PIPE ; ASME B36.10M ; PE ; A106-B ; SMLS,S-80	1	I233368017	5.9M
2	PIPE ; ASME B36.10M ; PE ; A106-B ; SMLS,S-80	3/4	I233367988	0.8M
3	TEE ; ASME B16.11 ; CL3000 ; SW ; A105	3/4X3/4	I114596556	1
4	E90 ; ASME B16.11 ; CL3000 ; SW ; A105	3/4	I114596551	1
5	CPLG RED ; ASME B16.11 ; CL3000 ; SW ; A105	1X3/4	I114596582	1
6	FLG SW ; ASME B16.5 ; CL150 ; RF ; A105,S-80	3/4	I257580300	1

ERECTION MATERIALS				
PT NO	DESCRIPTION	NPD (IN)	CLIENT CODE	QTY
7	PIPE ; ASME B36.10M ; PE ; A106-B ; SMLS,S-80	3/4	I233367988	8.3M
8	FLG BLIND ; ASME B16.5 ; CL150 ; RF ; A105	3/4	I114607605	1
9	GSKT SPRL WND ; ASME B16.20 ; CL150 ; RF ; 304-W , GRAPH-F , CS-CR , 304-IR ; THK 4.5 mm	3/4	I118404970	2
10	BLT STUD W/2 HVY NUT ; ASME B18.31.2 & B18.2.2 ; A193 GR.B7/A194 GR.2H - 70 mm Length	X70	I152185979	8
11	GATE ; ASME B16.10 ; CL150 ; RF ; STD BORE, BLT BNT, OS&Y, SOL WG ; HANDWHEEL ; A105 ; TRIM CN8 ; GRAPHITE PACKING	3/4	I137114087	1

PIPE SUPPORTS				
12	UB01-A-1-A	1	Pipe Support	2
13	UB01-A-0.75-A	3/4	Pipe Support	4
14	FR10-A-249-249-1070-150-C-1	1	Pipe Support	2

WELD LIST					CUT PIPE LENGTH					
Joint No	Size	F/S	Weld Type	Material	No	Size	Length	No	Size	Length
F40	1"	FIELD	SW	1-	1	1"	5854	2	3/4"	8274
S41	1"	SHOP	SW	5-1	3	3/4"	408	4	3/4"	150
F42	3/4"	FIELD	SW	2.2-5	5	3/4"	150			
S43	3/4"	SHOP	SW	3-2.2						
F44	3/4"	FIELD	SW	2.1-3						
S45	3/4"	SHOP	SW	6-2.1						
F46	3/4"	FIELD	SW	3-2.3						
S47	3/4"	SHOP	SW	2.3-4						
F48	3/4"	FIELD	SW	4-7						

SPOOL NUMBERS				
000207-NG-3518U-SP01	000207-NG-3518U-SP02			
000207-NG-3518U-SP03	000207-NG-3518U-SP04			

CAA-1 PROJECT
Cilegon, Banten, Indonesia



Chandra Asri

PT CHANDRA ASRI ALKALI

Confidential

ISSUE FOR REVIEW



China Chengda Engineering Co.,Ltd

Scale
1/1
@A3

Sheet
1 of 1

Project Doc Number :

Isometric drawing No:
Contractor/Licensor Doc No:

00-42-0207-26-NG-3518U-06
1"-NG-3518U-C01-06

Rev	Date	Description	Prepared	Checked	Approved	Authorized
1		THE INFORMATION CONTAINED IN THIS DOCUMENT IS CONFIDENTIAL AND/OR RESTRICTED, PRIVILEGED, AND ONLY FOR THE SOLE USE OF THE INTENDED RECIPIENT AND INTENDED PURPOSE. ANY FORM OF REPRODUCTION, DISSEMINATION, COPYING, DISCLOSURE, MODIFICATION AND/OR PUBLICATION IS STRICTLY PROHIBITED WITHOUT PRIOR WRITTEN CONSENT FROM PT CHANDRA ASRI ALKALI AND/OR FROM THE RELEVANT OWNER OF SUCH INFORMATION.				
ISOMATRIC NOTE:						
DESIGN TEMP.	deg C	65	OPE. TEMP.	deg C	-8/-	PWHT
DESIGN PREESS.	kg/cm ² g	12	OPE. PREESS.	kg/cm ² g	-8/-	PAINT SYSTEM
PT	%	10	RT	%	5	TEST PRESS.
INSULATION	CODE	-	INSUL. THICK.	mm	-	TEST MEDIA

Document Review Result						
☐ Approved	☐ Reviewed with Comment					
☐ Approved with Comments						
☐ No Comment						
☐ Rejected	☐ No Comment with Hold					
Approved by :						
Date :						
LEGEND						
SHOP WELD	FIELD WELD	SOCKET WELD	SCREWED JOINT	PIPE SUPPORT	LAGGED PIPE	TRACED PIPE
—●—	—X—	—E—	—E—	—E—	—E—	—E—