


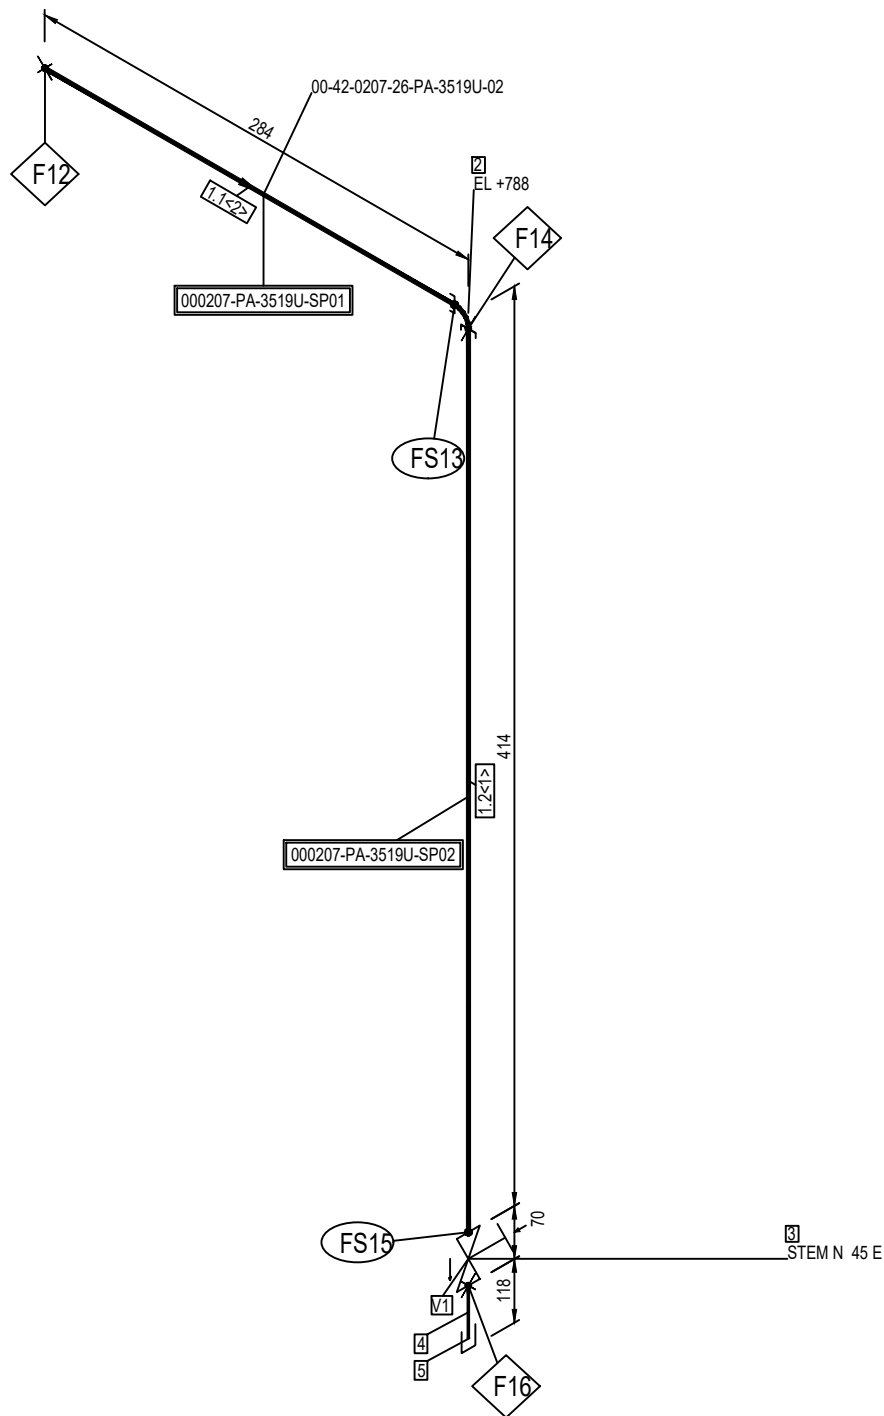

WELD LIST					CUT PIPE LENGTH					
Joint No	Size	F/S	Weld Type	Material	No	Size	Length	No	Size	Length
F12	3/4"	FIELD	BW	1.1-*	1	3/4"	394	2	3/4"	264
FS13	3/4"	SHOP	SW	1.1-2	3	3/4"	100			
F14	3/4"	FIELD	SW	2-1.2						
FS15	3/4"	SHOP	BW	1.2-3						
F16	3/4"	FIELD	BW	3-4						

CAA-1 PROJECT
Cilegon, Banten, Indonesia



PT CHANDRA ASRI ALKALI

Confidential

ISSUE FOR REVIEW



China Chengda Engineering Co.,Ltd

Scale
1/1
@A3

Sheet
1 of 1

Project Doc Number :

Isometric drawing No:

00-42-0207-26-PA-3519U-02

Document Review Result	
☐ Approved	☐ Reviewed with Comment
☐ Approved with Comments	
☐ No Comment	
☐ Rejected	☐ No Comment with Hold
Approved by :	
Date :	

LEGEND

SHOP WELD	FIELD WELD	SOCKET WELD	SCREWED JOINT	PIPE SUPPORT	LAGGED PIPE	TRACED PIPE