
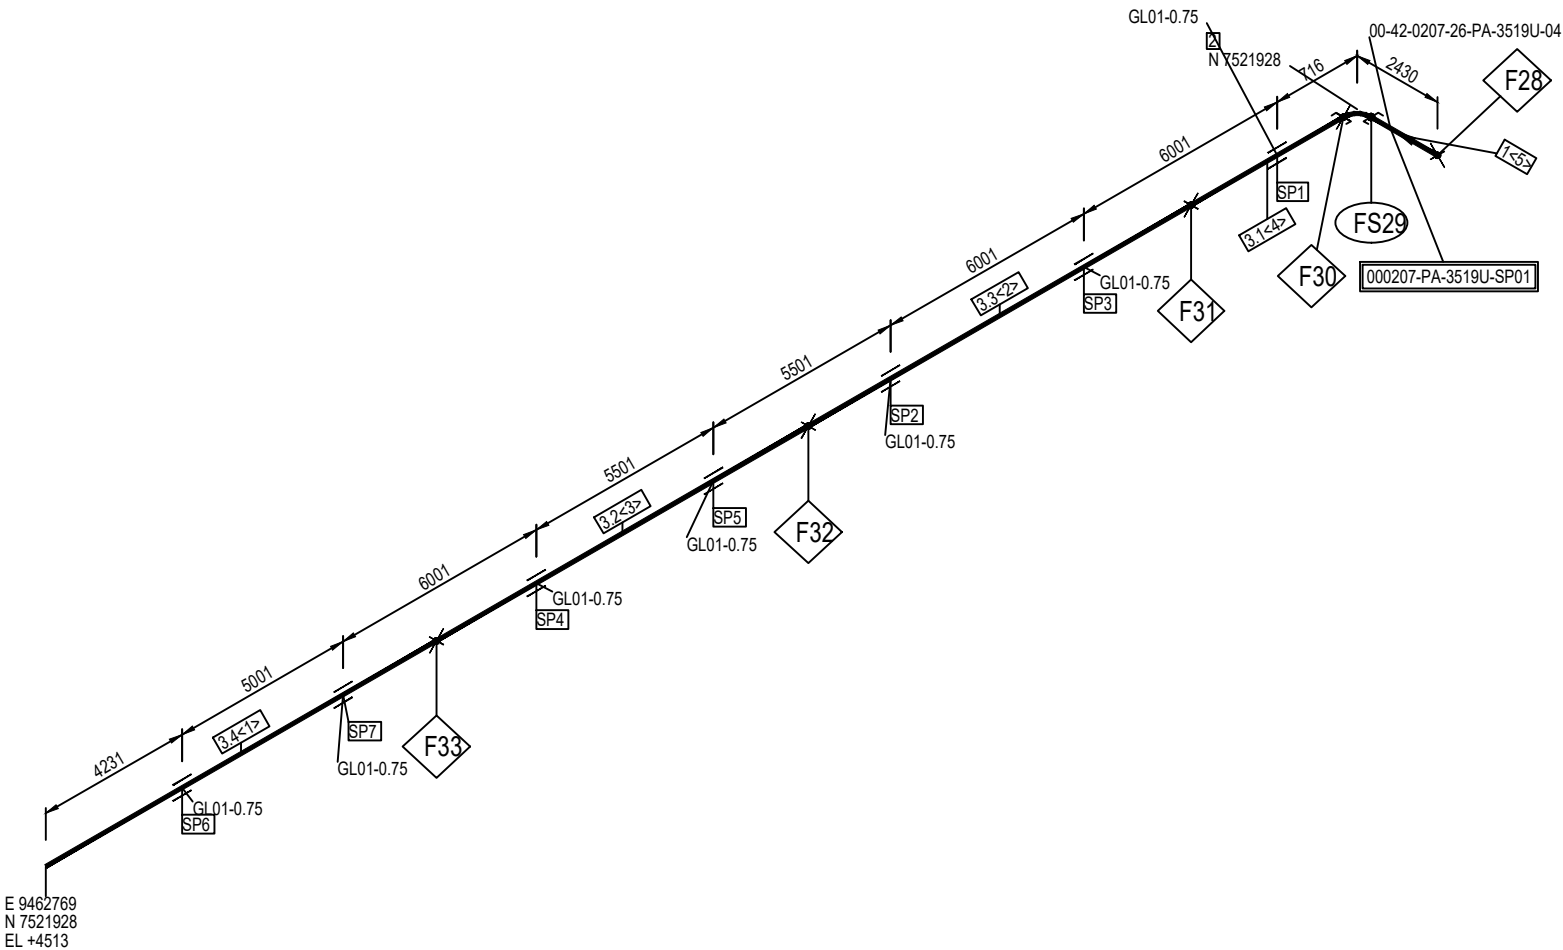


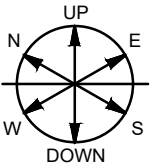

<u>FABRICATION MATERIALS</u>					
PT			NPD		
<u>NO</u>	<u>DESCRIPTION</u>		<u>(IN)</u>	<u>CLIENT CODE</u>	<u>QTY</u>
1	PIPE ; ASME B36.10M ; PE ; A106-B ; SMLS,S-80		3/4	I233367988	2.5M
2	E90 ; ASME B16.11 ; CL3000 ; SW ; A105		3/4	I114596551	1
<u>ERECTION MATERIALS</u>					
PT			NPD		
<u>NO</u>	<u>DESCRIPTION</u>		<u>(IN)</u>	<u>CLIENT CODE</u>	<u>QTY</u>
3	PIPE ; ASME B36.10M ; PE ; A106-B ; SMLS,S-80		3/4	I233367988	39.0M
<u>PIPE SUPPORTS</u>					
4	GL01-0.75		3/4	Pipe Support	7

WELD LIST					CUT PIPE LENGTH		
Joint No	Size	F/S	Weld Type	Material	No	Size	Length
F28	3/4"	FIELD	BW	1-*	1	3/4"	12000
FS29	3/4"	SHOP	SW	1-2	3	3/4"	12000
F30	3/4"	FIELD	SW	2-3.1	5	3/4"	2410
F31	3/4"	FIELD	BW	3.3-3.1			
F32	3/4"	FIELD	BW	3.2-3.3			
F33	3/4"	FIELD	BW	3.4-3.2			

SPOOL NUMBERS
000207-PA-3519U-SP01

CAA-1 PROJECT
Cilegon, Banten, Indonesia



Chandra Asri

PT CHANDRA ASRI ALKALI

Confidential

ISSUE FOR REVIEW



China Chengda Engineering Co.,Ltd

Scale
1/1
@A3

Sheet
1 of 1

Project Doc Number :

Isometric drawing No:
Contractor/Licensor Doc No:

00-42-0207-26-PA-3519U-04
0.75"-PA-3519U-1C2-04

Rev	Date	Description	Prepared	Checked	Approved	Authorized
THE INFORMATION CONTAINED IN THIS DOCUMENT IS CONFIDENTIAL AND/OR RESTRICTED, PRIVILEGED, AND ONLY FOR THE SOLE USE OF THE INTENDED RECIPIENT AND INTENDED PURPOSE. ANY FORM OF REPRODUCTION, DISSEMINATION, COPYING, DISCLOSURE, MODIFICATION AND/OR PUBLICATION IS STRICTLY PROHIBITED WITHOUT PRIOR WRITTEN CONSENT FROM PT CHANDRA ASRI ALKALI AND/OR FROM THE RELEVANT OWNER OF SUCH INFORMATION.						
ISOMATRIC NOTE:						
DESIGN TEMP.	deg C	65	OPE. TEMP.	deg C	-/AMB/-	PWHT
DESIGN PREESS.	kg/cm ² g	10.5	OPE. PREESS.	kg/cm ² g	-/7.5/-	PAINT SYSTEM
PT	%	-	RT	%	2	TEST PRESS.
INSULATION	CODE	-	INSUL. THICK.	mm	-	TEST MEDIA

Document Review Result						
☐ Approved	☐ Reviewed with Comment	☐ Approved with Comments	☐ No Comment	☐ Rejected	☐ No Comment with Hold	
Approved by :						
Date :						
LEGEND						
SHOP WELD	FIELD WELD	SOCKET WELD	SCREWED JOINT	PIPE SUPPORT	LAGGED PIPE	TRACED PIPE