


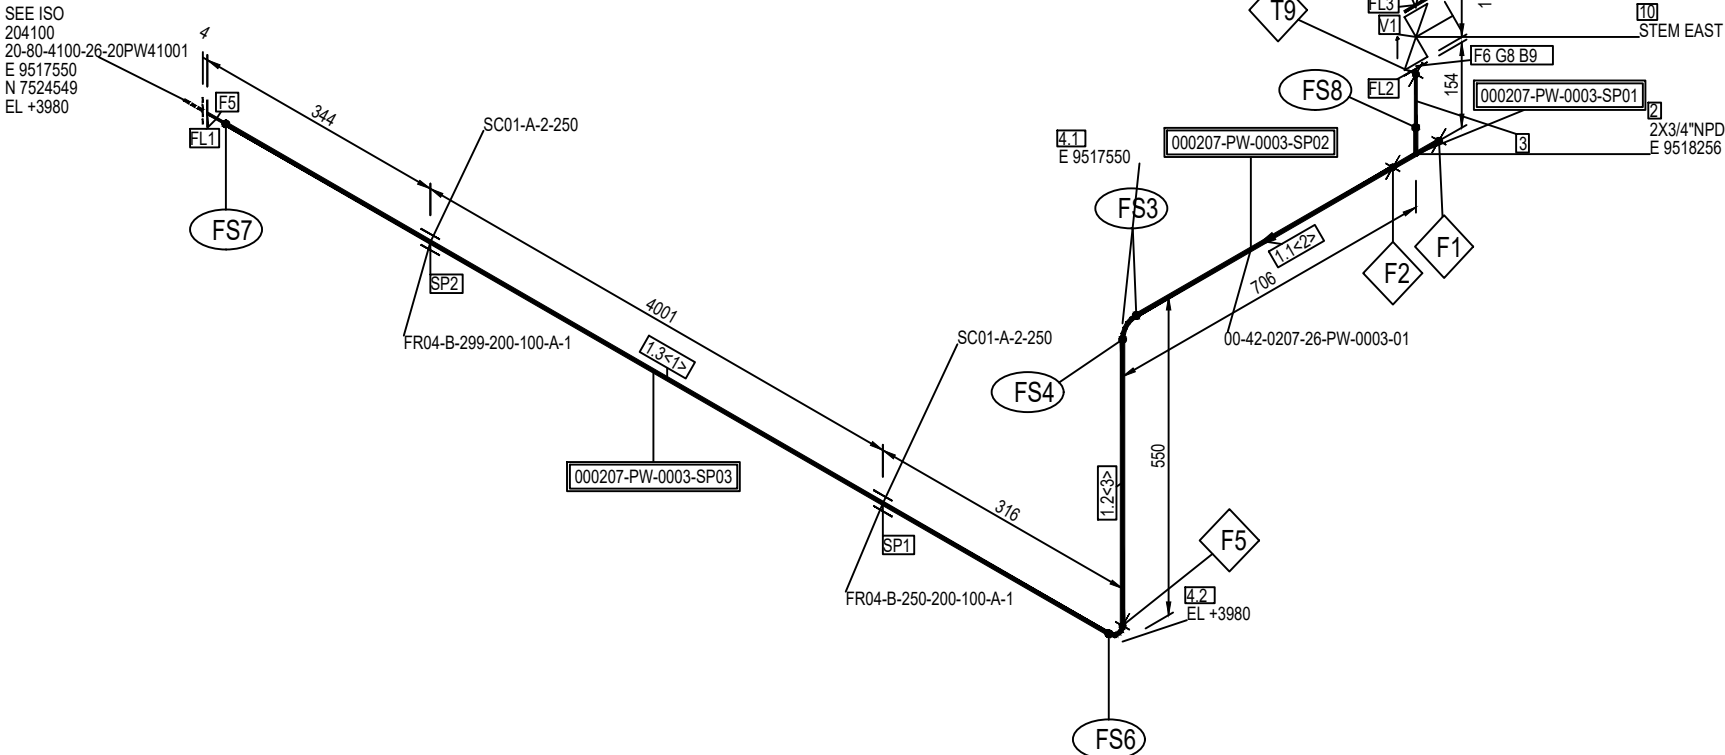

<u>ERECTION MATERIALS</u>				
PT NO	DESCRIPTION	NPD (IN)	CLIENT CODE	QTY
6	FLG THD ; ASME B16.5 ; CL150 ; RF ; A105 ; GALV.	3/4	I472177256	1
7	FLG BLIND ; ASME B16.5 ; CL150 ; RF ; A105 ; GALV.	3/4	I115473122	1
8	GSKT NON METALLIC ; ASME B16.21 ; CL150 ; RF ; RPTFE GYLON 3500 OR EQUAL ; THK 3 mm	3/4	I368194621	2
9	BLT STUD W/2 HVY NUT ; ASME B18.31.2 & B18.2.2 ; A193 GR.B7/A194 GR.2H ; W/2 WASHER; GALV. - 70 mm Length	X70	I537948375	8
10	GATE ; ASME B16.10 ; CL150 ; RF ; STD BORE, BLT BNT, OS&Y, SOL WG ; HANDWHEEL ; B62-UNS C83600 ;TRIM SAME AS BODY ;GRAPHITE PACKING	3/4	I560056231	1

WELD LIST					CUT PIPE LENGTH					
Joint No	Size	F/S	Weld Type	Material	No	Size	Length	No	Size	Length
F1	2"	FIELD	BW	2-*	1	2"	4575	2	2"	566
F2	2"	FIELD	BW	2-1.1	3	2"	398			
FS3	2"	SHOP	BW	1.1-4.1						
FS4	2"	SHOP	BW	4.1-1.2						
F5	2"	FIELD	BW	1.2-4.2						
FS6	2"	SHOP	BW	4.2-1.3						
FS7	2"	SHOP	SW	1.3-5						
FS8	3/4"	SHOP	BW	2-3						
T9	3/4"	FIELD	S	3-6						

CAA-1 PROJECT
Cilegon, Banten, Indonesia



PT CHANDRA ASRI ALKALI

Confidential

ISSUE FOR REVIEW



China Chengda Engineering Co., Ltd

Sheet
1 of 1

Project

Project Doc Number :

Isometric drawing No:

00-42-0207-26-PW-0003-01

Contractor/Licenser Doc No:

2"-PW-0003-1C6-HC-01

Document Review Result	
☐ Approved	☐ Reviewed with Comments
☐ Approved with Comments	
☐ No Comment	
☐ Rejected	☐ No Comment with Hold

LEGEND

SHOP WELD	FIELD WELD	SOCKET WELD	SCREWED JOINT	PIPE SUPPORT	LAGGED PIPE	TRACED PIPE