
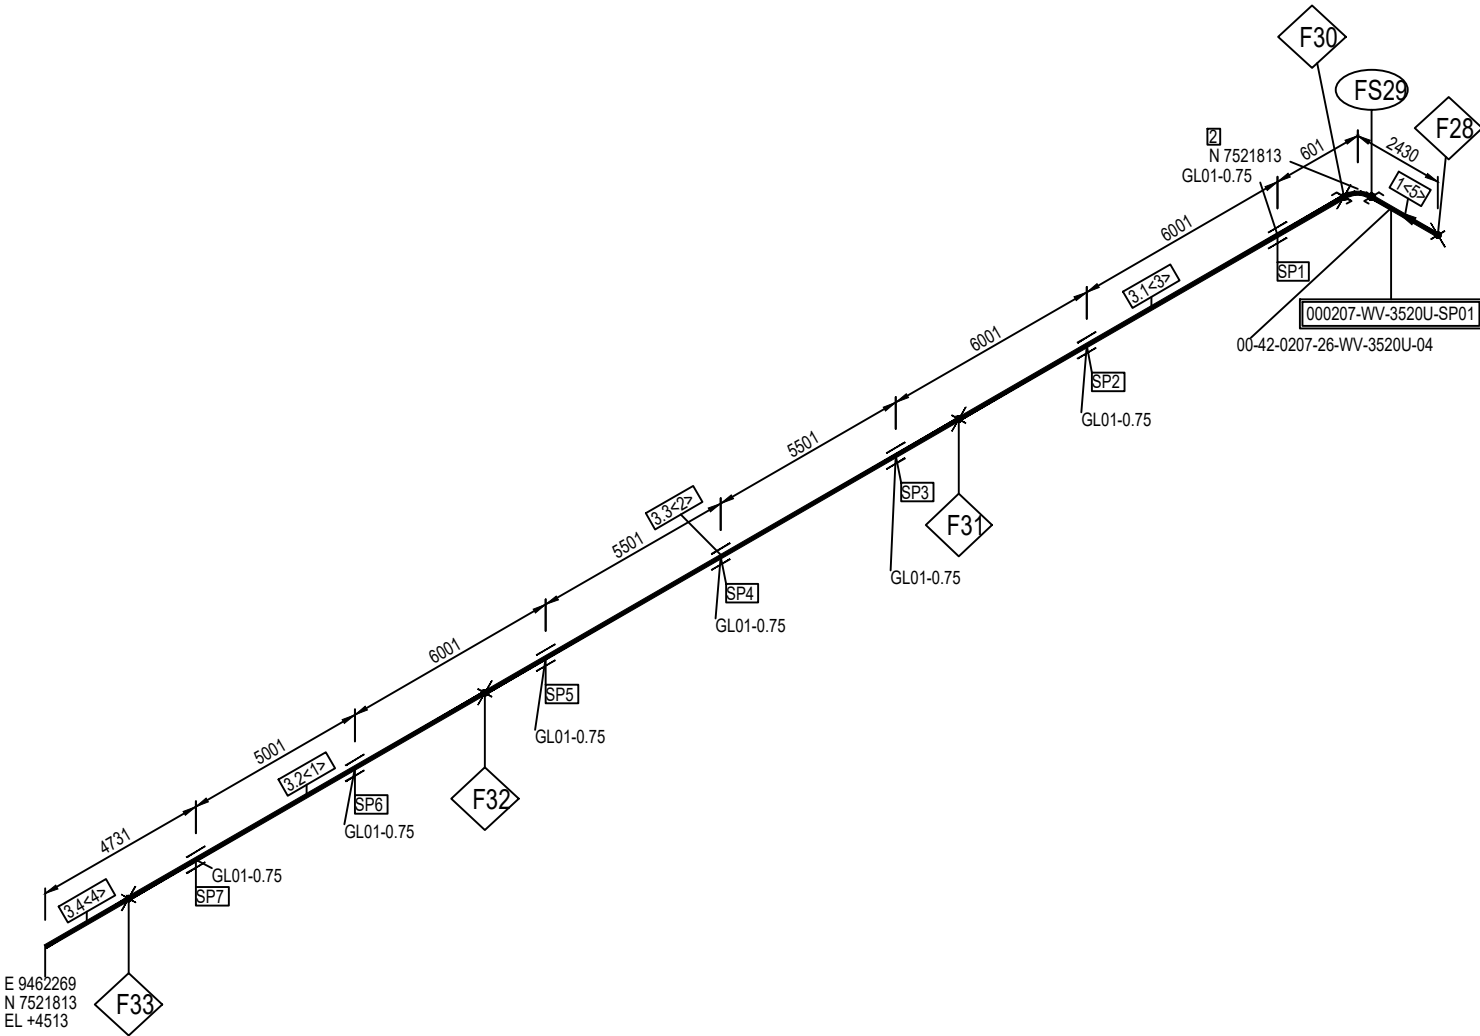


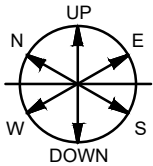

<u>FABRICATION MATERIALS</u>					
PT			NPD		
<u>NO</u>	<u>DESCRIPTION</u>		<u>(IN)</u>	<u>CLIENT CODE</u>	<u>QTY</u>
1	PIPE ; ASME B36.10M ; PE ; A106-B ; SMLS,S-80		3/4	I233367988	2.5M
2	E90 ; ASME B16.11 ; CL3000 ; SW ; A105		3/4	I114596551	1
<u>ERECTION MATERIALS</u>					
PT			NPD		
<u>NO</u>	<u>DESCRIPTION</u>		<u>(IN)</u>	<u>CLIENT CODE</u>	<u>QTY</u>
3	PIPE ; ASME B36.10M ; PE ; A106-B ; SMLS,S-80		3/4	I233367988	39.4M
<u>PIPE SUPPORTS</u>					
4	GL01-0.75		3/4	Pipe Support	7

WELD LIST					CUT PIPE LENGTH		
Joint No	Size	F/S	Weld Type	Material	No	Size	Length
F28	3/4"	FIELD	BW	1-*	1	3/4"	12000
FS29	3/4"	SHOP	SW	1-2	3	3/4"	12000
F30	3/4"	FIELD	SW	2-3.1	5	3/4"	2410
F31	3/4"	FIELD	BW	3.1-3.3			
F32	3/4"	FIELD	BW	3.3-3.2			
F33	3/4"	FIELD	BW	3.2-3.4			

SPOOL NUMBERS
000207-WV-3520U-SP01

CAA-1 PROJECT
Cilegon, Banten, Indonesia



Chandra Asri

PT CHANDRA ASRI ALKALI

Confidential

ISSUE FOR REVIEW



China Chengda Engineering Co.,Ltd

Scale
1/1
@A3

Sheet
1 of 1

Project Doc Number :

Isometric drawing No:

00-42-0207-26-WV-3520U-04

Contractor/Licensor Doc No:

0.75*WV-3520U-C01-04


Document Review Result

- ☐ Approved
- ☐ Reviewed with Comment
- ☐ Approved with Comments
- ☐ No Comment
- ☐ Rejected
- ☐ No Comment with Hold

Approved by :

Date :

LEGEND

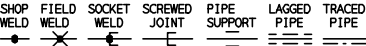

THE INFORMATION CONTAINED IN THIS DOCUMENT IS CONFIDENTIAL AND/OR RESTRICTED, PRIVILEGED, AND ONLY FOR THE SOLE USE OF THE INTENDED RECIPIENT AND INTENDED PURPOSE.
ANY FORM OF REPRODUCTION, DISSEMINATION, COPYING, DISCLOSURE, MODIFICATION AND/OR PUBLICATION IS STRICTLY PROHIBITED WITHOUT PRIOR WRITTEN
CONSENT FROM PT CHANDRA ASRI ALKALI AND/OR FROM THE RELEVANT OWNER OF SUCH INFORMATION.

ISOMATRIC NOTE:		DESIGN TEMP.		deg C		OPE. TEMP.		deg C		-/AMB/-		PWHT		N		P&ID NO.		PED-PIID-E-00015	
DESIGN PREESS.		kg/cm ² g		8		OPE. PREESS.		kg/cm ² g		-/4/-		PAINT SYSTEM		P22		GA DWG. NO.			
PT		%		10		RT		%		5		TEST PRESS.		kg/cm ² g		12.0		WBS	
INSULATION		CODE		-		INSUL. THICK.		mm		-		TEST MEDIA				000207			