
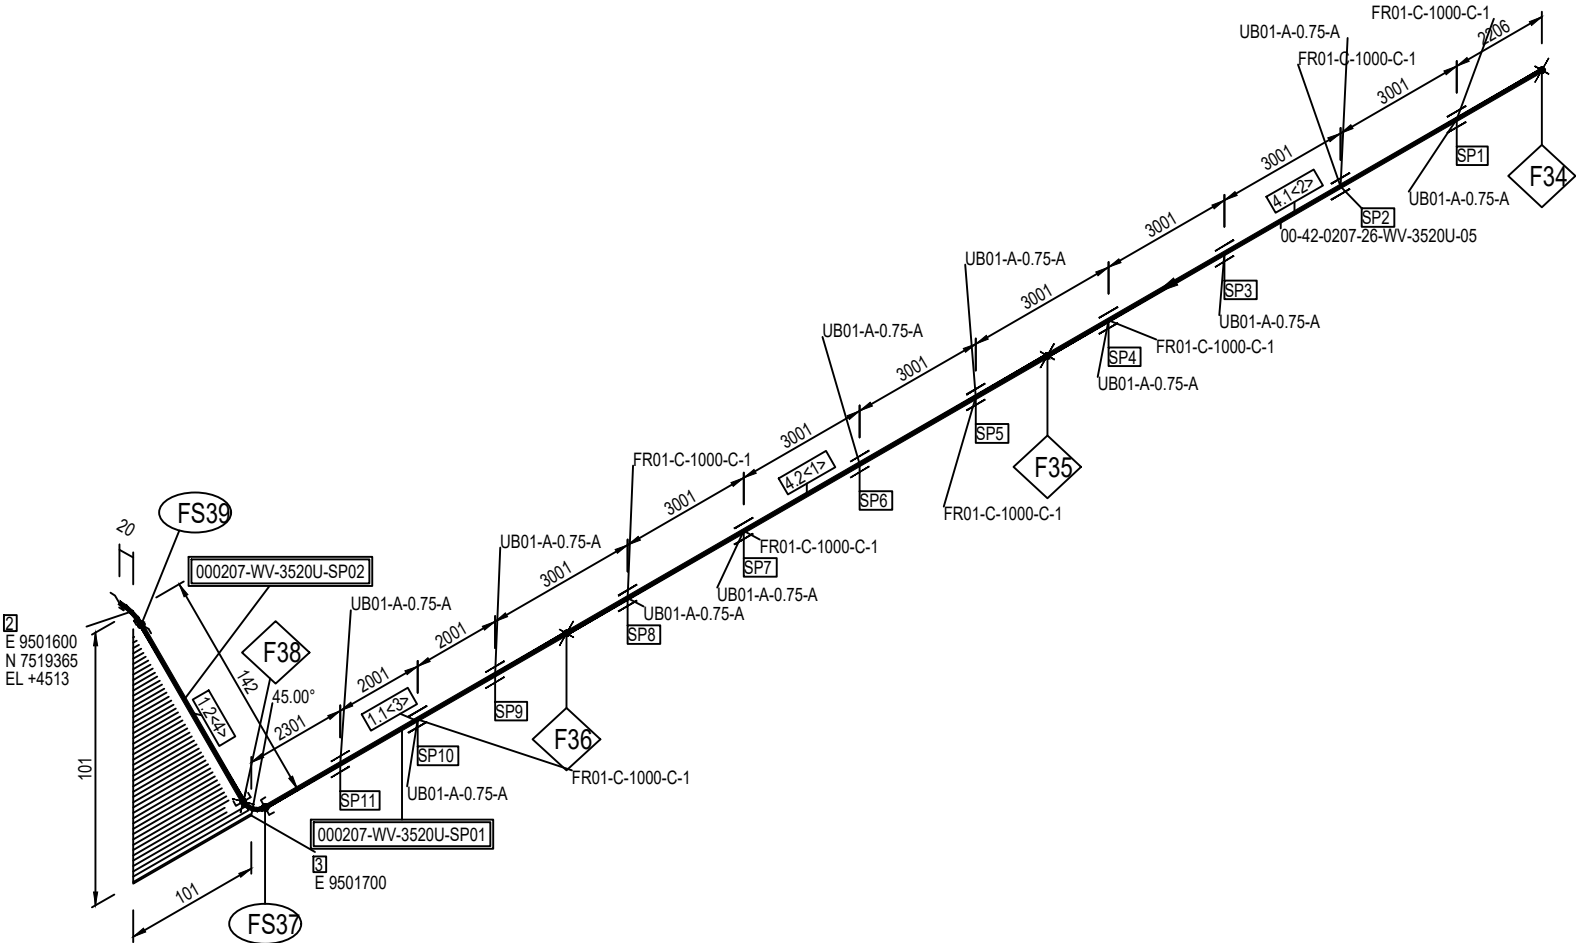


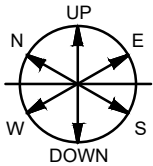

FABRICATION MATERIALS				
PT			NPD	
NO	DESCRIPTION		(IN)	CLIENT CODE QTY
1	PIPE ; ASME B36.10M ; PE ; A106-B ; SMLS,S-80		3/4	I233367988 8.7M
2	E90 ; ASME B16.11 ; CL3000 ; SW ; A105		3/4	I114596551 1
3	E45 ; ASME B16.11 ; CL3000 ; SW ; A105		3/4	I104320776 1
ERECTION MATERIALS				
PT			NPD	
NO	DESCRIPTION		(IN)	CLIENT CODE QTY
4	PIPE ; ASME B36.10M ; PE ; A106-B ; SMLS,S-80		3/4	I233367988 24.0M
PIPE SUPPORTS				
5	UB01-A-0.75-A		3/4	Pipe Support 11
6	FR01-C-1000-C-1		3/4	Pipe Support 7

WELD LIST					CUT PIPE LENGTH		
Joint No	Size	F/S	Weld Type	Material	No	Size	Length
F34	3/4"	FIELD	BW	4.1-*	1	3/4"	12000
F35	3/4"	FIELD	BW	4.1-4.2	2	3/4"	12000
F36	3/4"	FIELD	BW	4.2-1.1	3	3/4"	8493
FS37	3/4"	SHOP	SW	1.1-3	4	3/4"	110
F38	3/4"	FIELD	SW	3-1.2			
FS39	3/4"	SHOP	SW	1.2-2			

SPOOL NUMBERS
000207-WV-3520U-SP01 000207-WV-3520U-SP02

CAA-1 PROJECT
Cilegon, Banten, Indonesia



Chandra Asri

PT CHANDRA ASRI ALKALI

Confidential

ISSUE FOR REVIEW



China Chengda Engineering Co.,Ltd

Scale
1/1
@A3

Sheet
1 of 1

Project Doc Number :

Isometric drawing No:

00-42-0207-26-WV-3520U-05

Contractor/Licensor Doc No:

0.75"-WV-3520U-C01-05

Document Review Result

- ☐ Approved
- ☐ Reviewed with Comment
- ☐ Approved with Comments
- ☐ No Comment
- ☐ Rejected
- ☐ No Comment with Hold

Approved by :

Date :

LEGEND



Rev	Date	Description	Prepared	Checked	Approved	Authorized
THE INFORMATION CONTAINED IN THIS DOCUMENT IS CONFIDENTIAL AND/OR RESTRICTED, PRIVILEGED, AND ONLY FOR THE SOLE USE OF THE INTENDED RECIPIENT AND INTENDED PURPOSE. ANY FORM OF REPRODUCTION, DISSEMINATION, COPYING, DISCLOSURE, MODIFICATION AND/OR PUBLICATION IS STRICTLY PROHIBITED WITHOUT PRIOR WRITTEN CONSENT FROM PT CHANDRA ASRI ALKALI AND/OR FROM THE RELEVANT OWNER OF SUCH INFORMATION.						
ISOMATRIC NOTE:						
DESIGN TEMP.	deg C	65	OPE. TEMP.	deg C	-/AMB/-	PWHT
DESIGN PREESS.	kg/cm ² g	8	OPE. PREESS.	kg/cm ² g	-/4/-	PAINT SYSTEM
PT	%	10	RT	%	5	TEST PRESS.
INSULATION	CODE	-	INSUL. THICK.	mm	-	TEST MEDIA

P&ID NO. PED-PID-E-00015

GA DWG. NO.

WBS

000207